


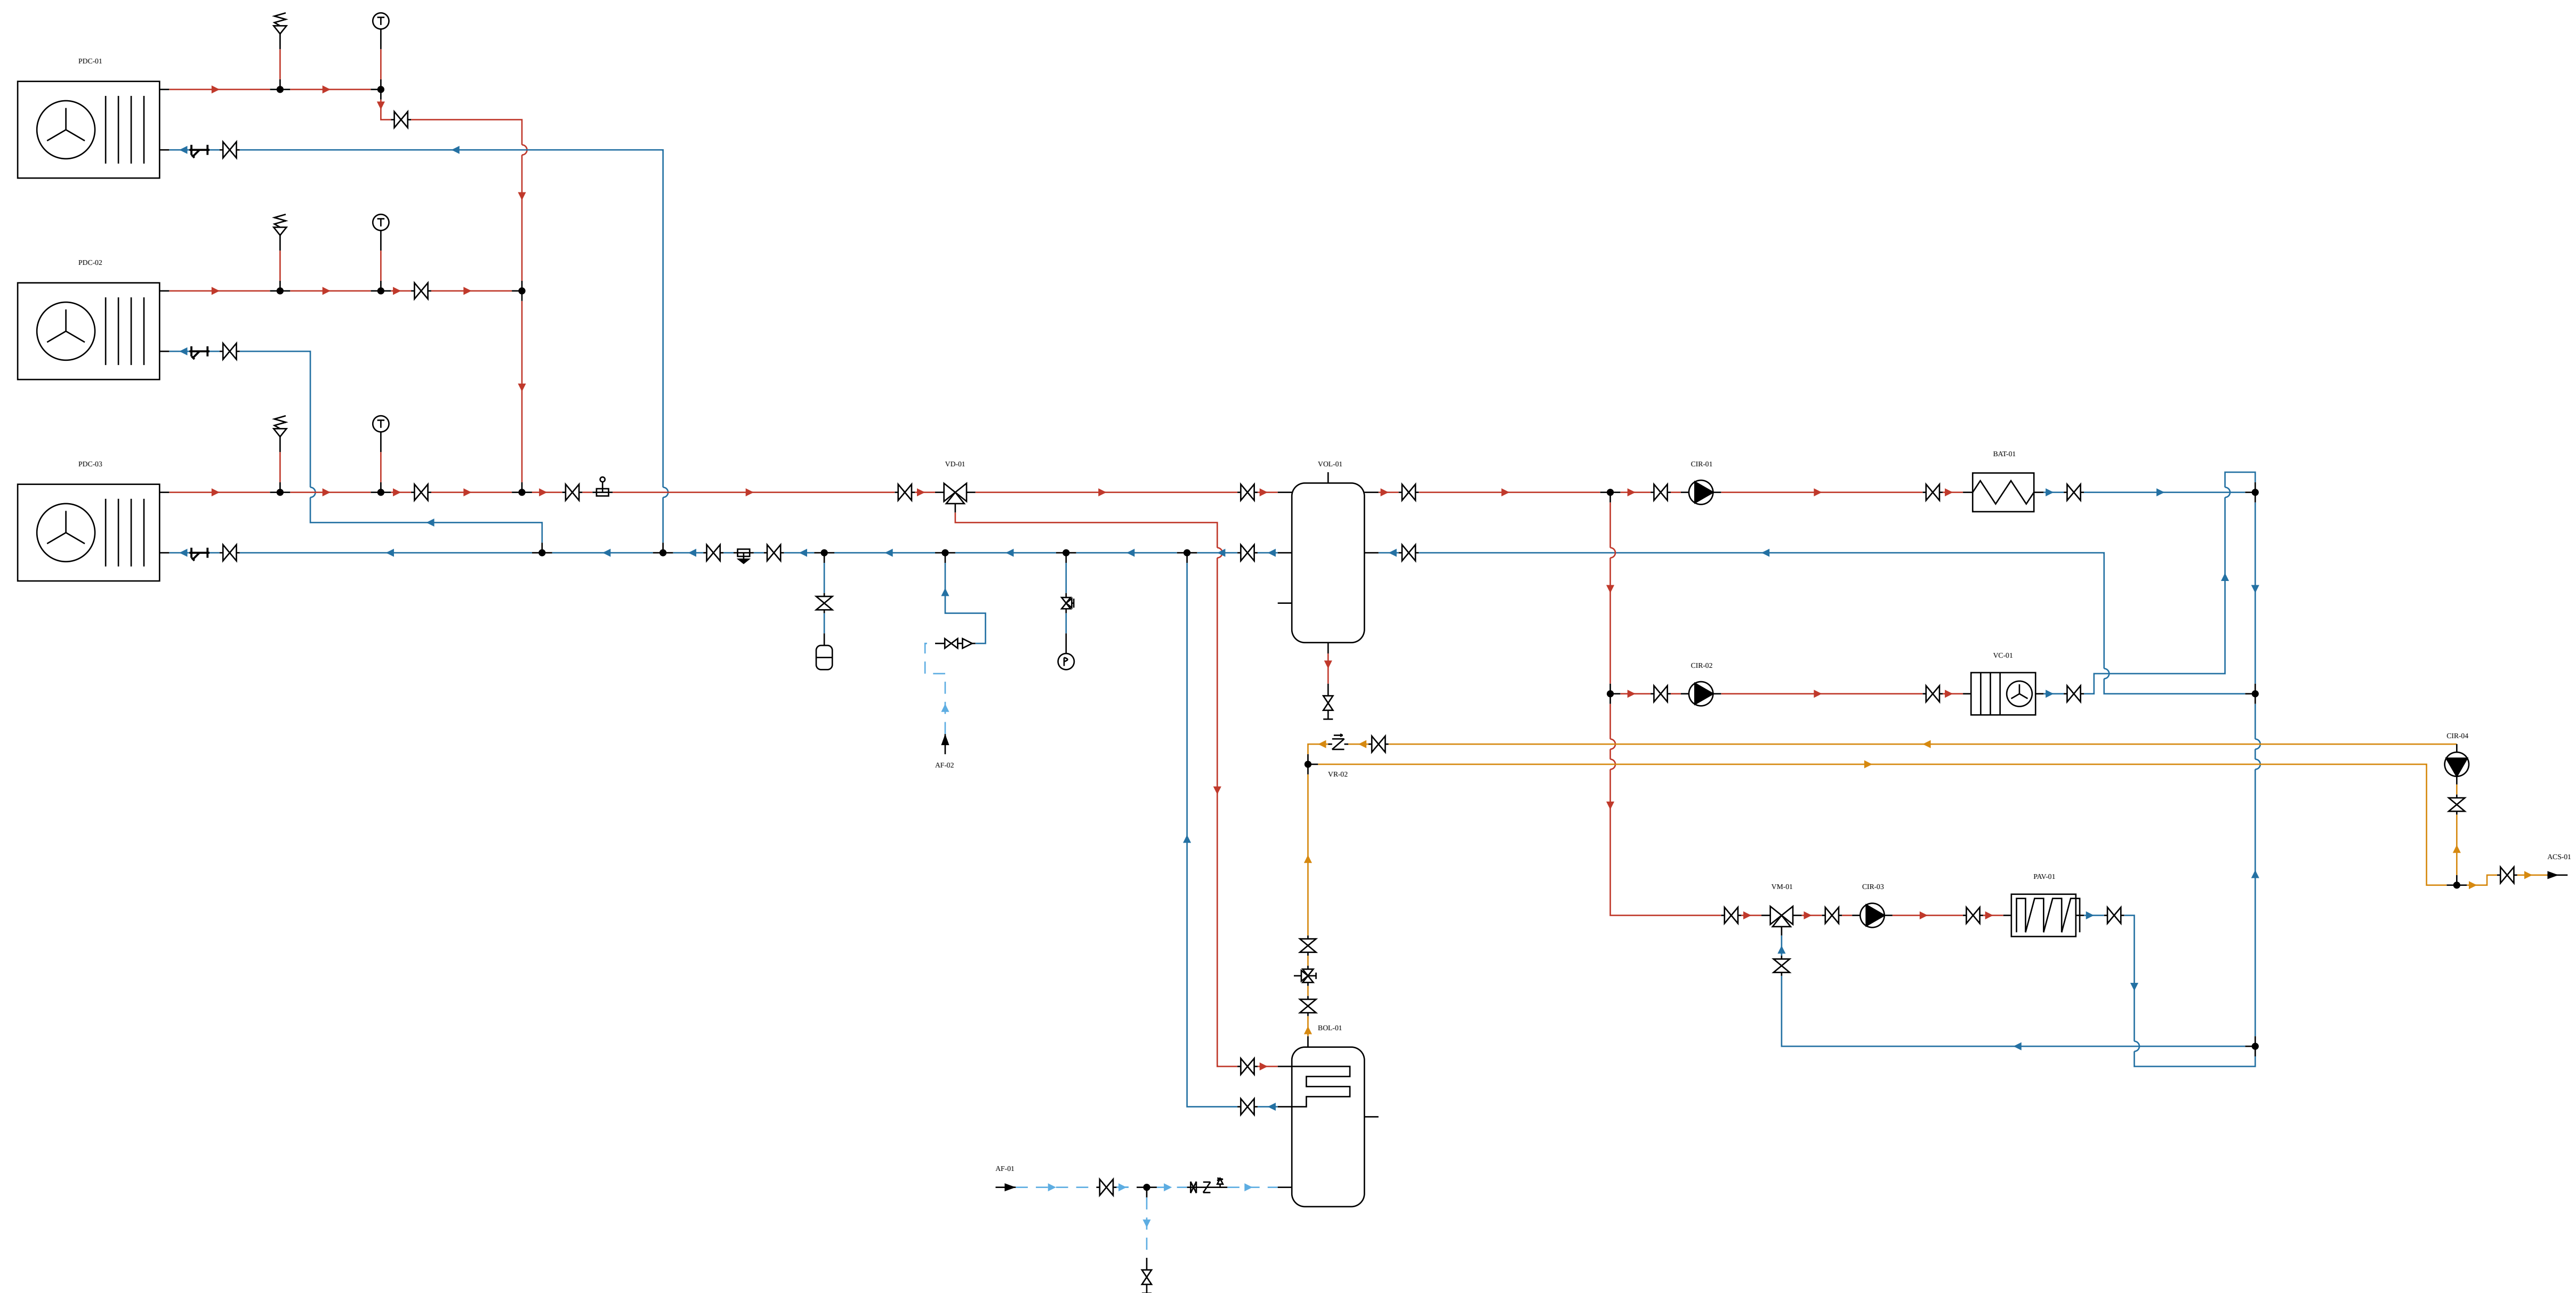

- | | |
|---|-------------------------------------|
|  | Interruttore di trattamento aria |
|  | Separatore d'aria |
|  | Vilano ventico a quattro attacchi |
|  | Bollitore ACS |
|  | Gruppo di sicurezza sanitario |
|  | Delugante |
|  | Valvola deviatrice a tre vie |
|  | Attacco di scarico |
|  | Vaso di espansione |
|  | Ventilcolettore |
|  | Pompa di riempimento |
|  | Gruppo di calore aria-acqua |
|  | Valvola miscelatrice a tre vie |
|  | Valvola miscelatrice termostatica |
|  | Contatto di fine |
|  | Manometro |
|  | Pompa di circolazione |
|  | Deviatore a T |
|  | Raccordo a T |
|  | Termometro |
|  | Pannello radiante |
|  | Valvola di tergilogo |
|  | Rilasciata prerompremento a tre vie |
|  | Valvola di intersezione |
|  | Valvola di sicurezza |

- Acqua fredda sanitaria — andata
- Acqua fredda sanitaria — ritorno
- Acqua calda sanitaria — andata
- Acqua calda sanitaria — ritorno
- Acqua di riscaldamento — andata
- Acqua di riscaldamento — ritorno