


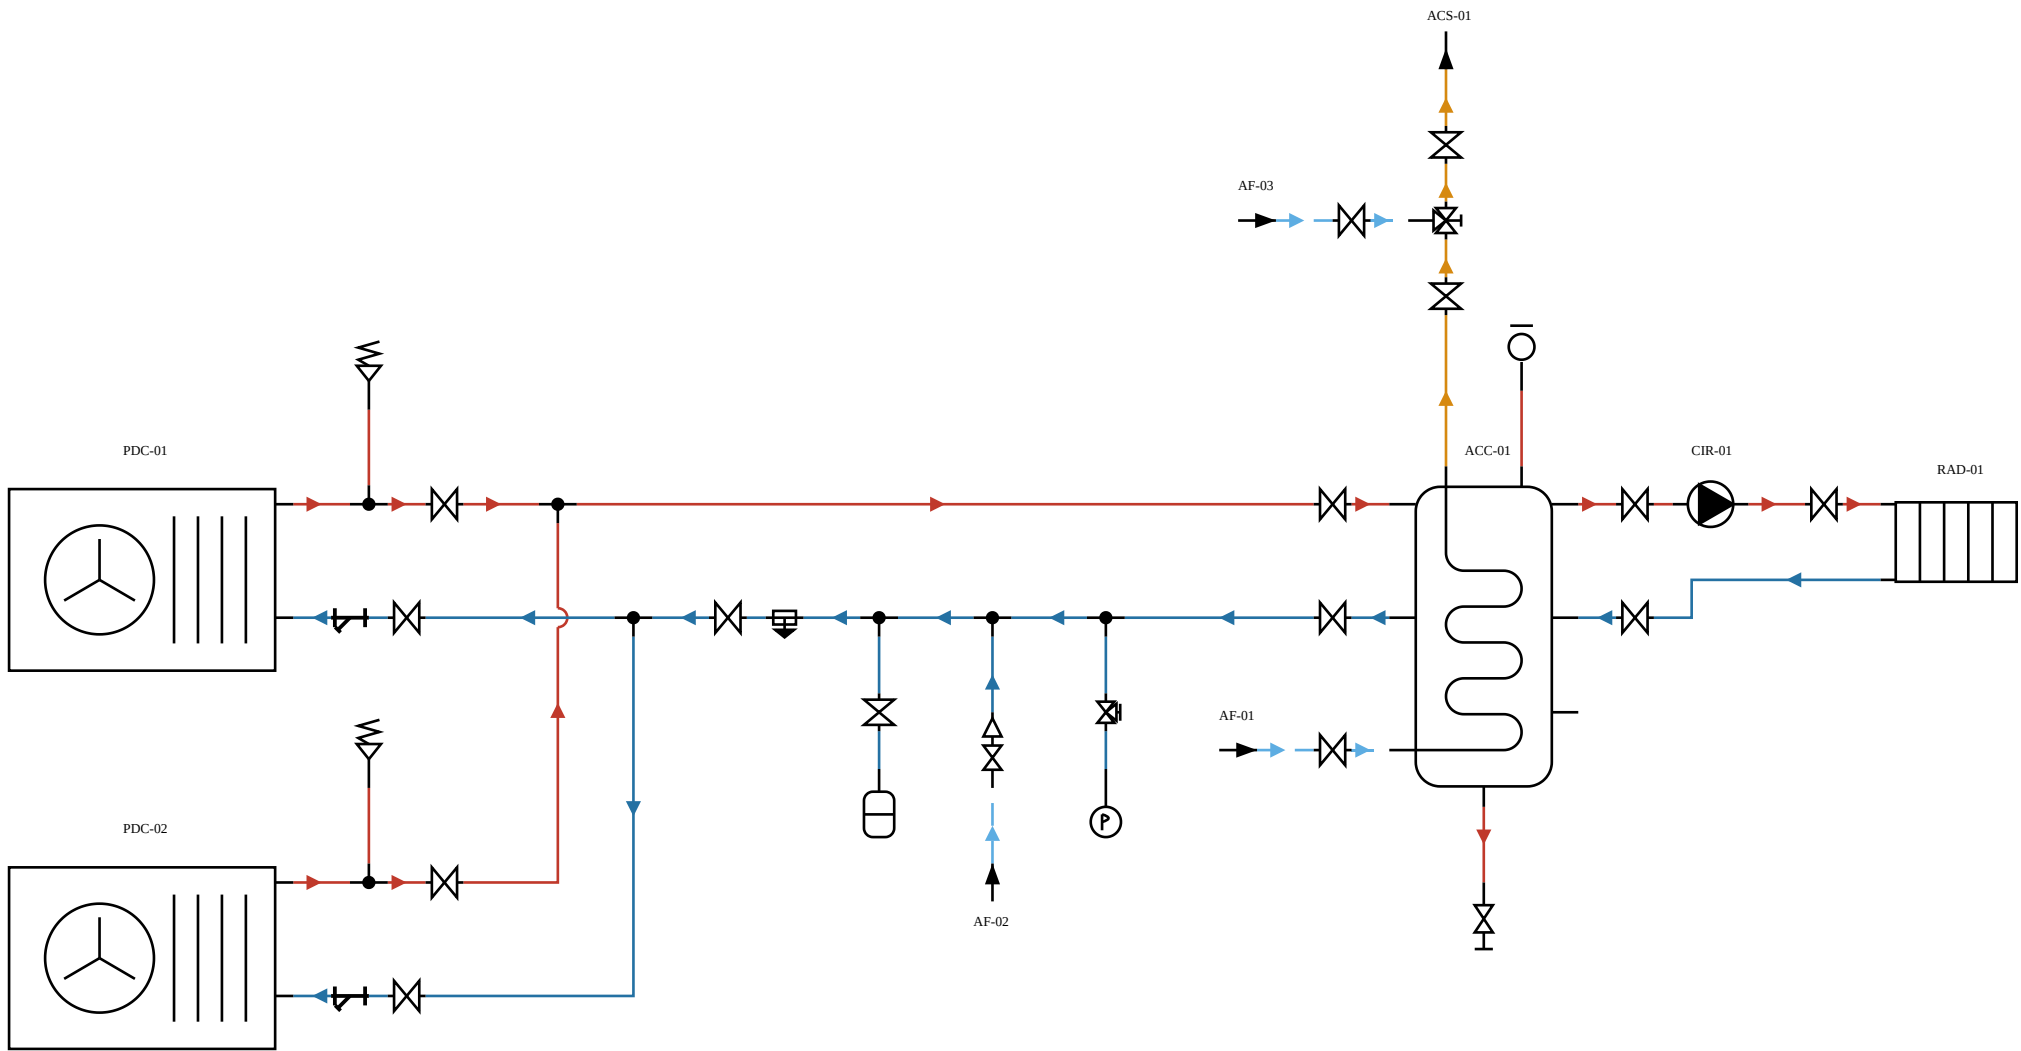

- Valvola di sfato aria
- Accumulo combinato
- Defangatore
- Attacco di scarico
- Vaso di espansione
- Gruppo di riempimento
- Pompa di calore aria-acqua
- Valvola miscelatrice termostatica
- Confine di rete
- Manometro
- Pompa di circolazione
- Radiatore
- Filtro a Y
- Derivazione a T
- Raccordo a T
- Rubinetto portamanometro a tre vie
- Valvola di intercettazione
- Valvola di sicurezza
- Acqua fredda sanitaria — andata
- Acqua calda sanitaria — andata
- Acqua di riscaldamento — andata
- Acqua di riscaldamento — ritorno

 VALORIZZAZIONE. EFFICIENTAMENTO. RIQUALIFICAZIONE.	COMMITTENTE Condominio di prova	PROGETTO Due pompe di calore in parallelo con accumulo combinato	SCALA —	DATA 06.08.2026	APPROVATO	TAVOLA T1
	INDIRIZZO Via di Prova 1, 00000 Comune di Prova (XX)	TITOLO TAVOLA Schema funzionale della centrale termica	REVISIONE Rev. 00	COMMESSA PROVA	VERIFICATO	
					DISEGNATO	