


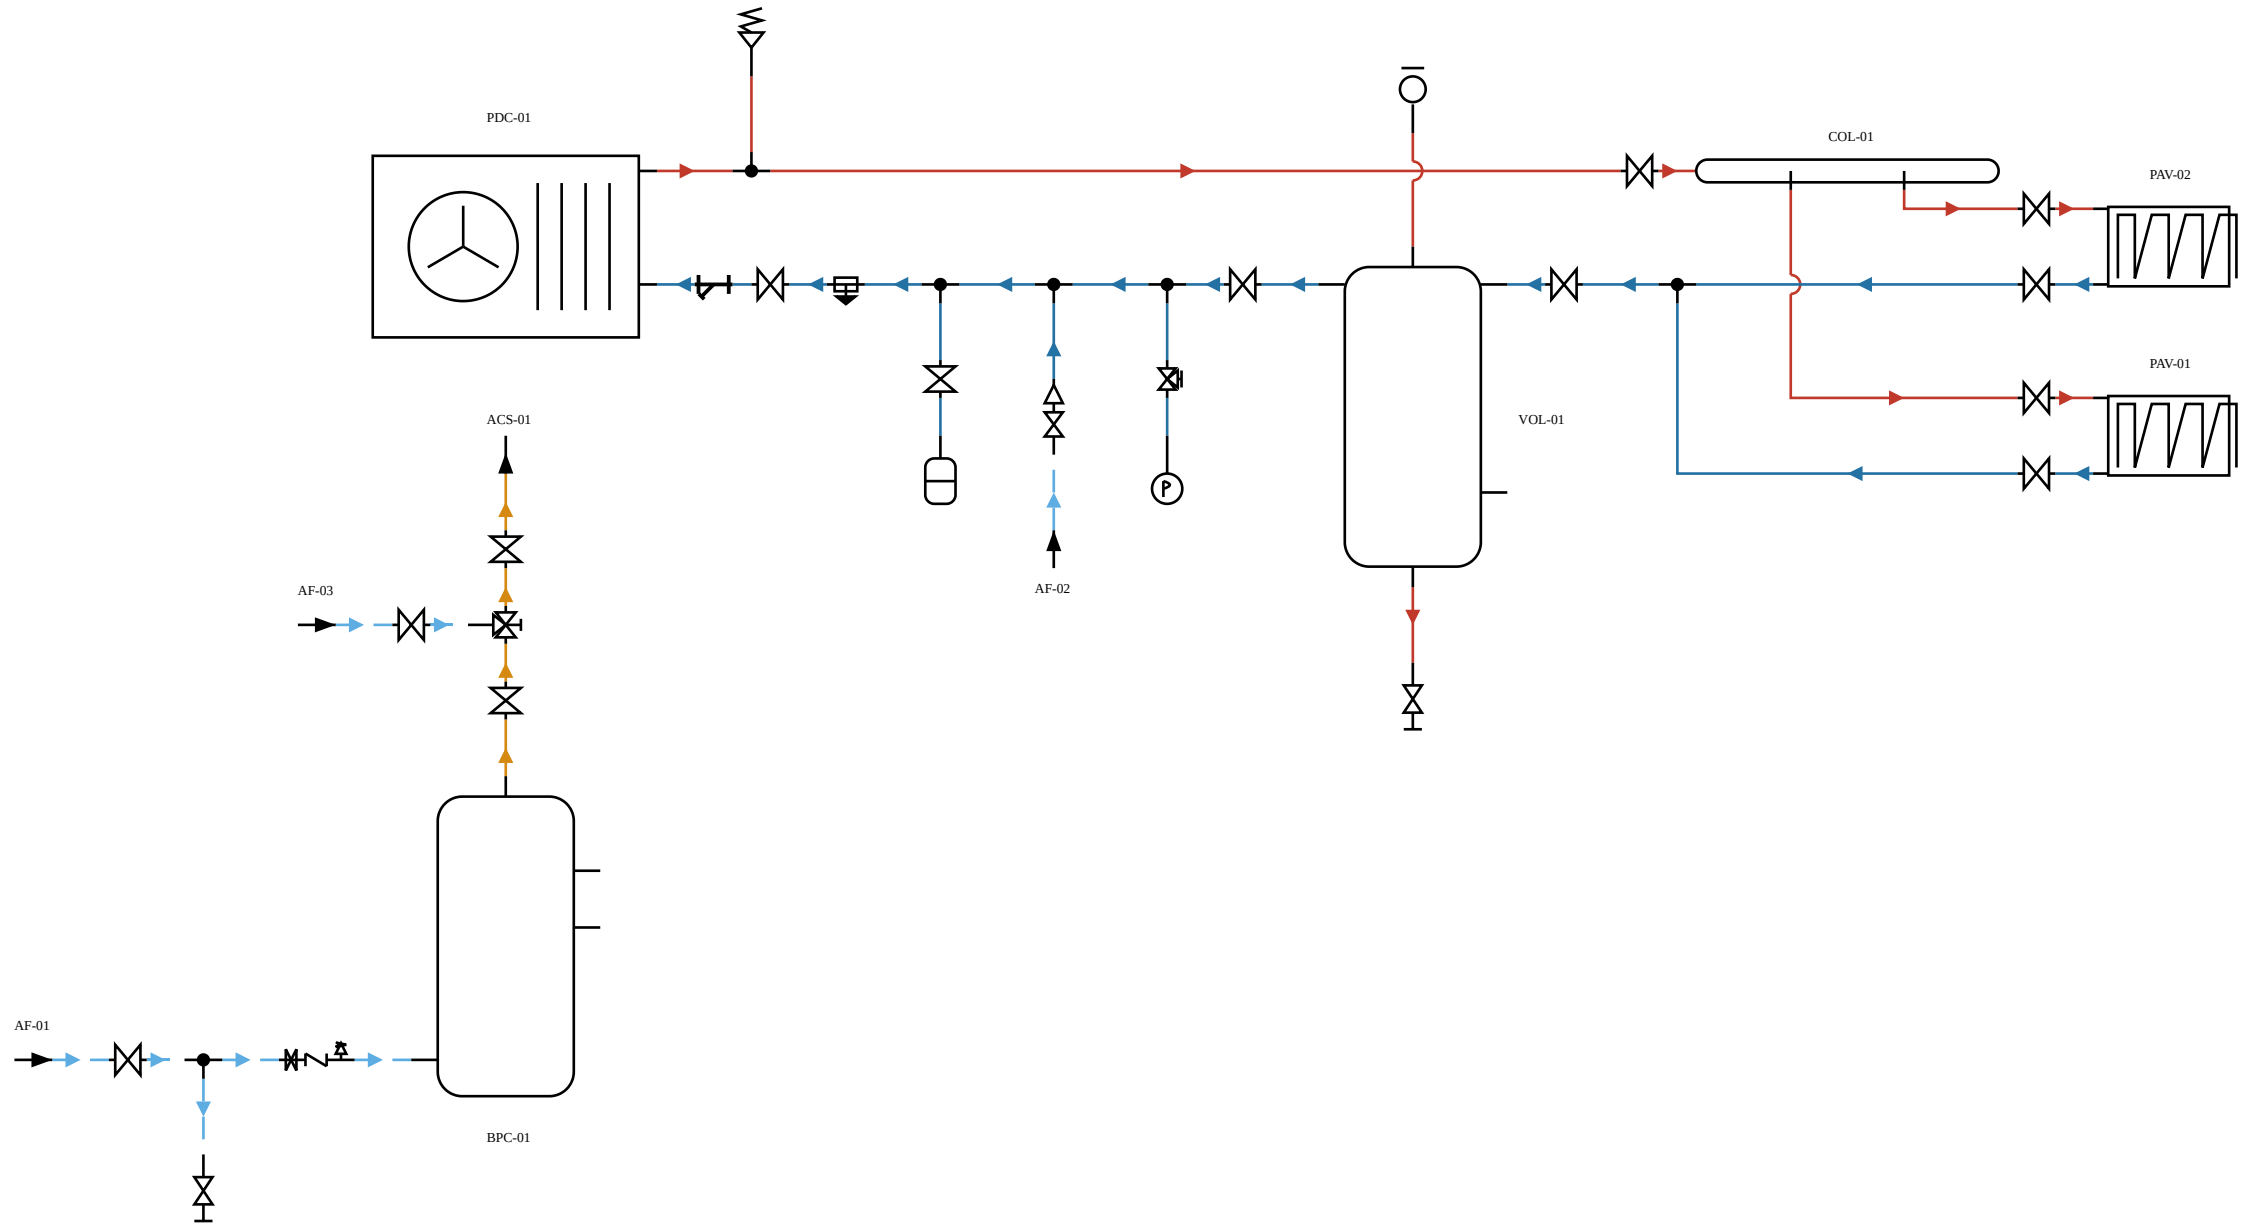

- Valvola di sfato aria
- Volano termico a due attacchi
- Boiler in pompa di calore
- Gruppo di sicurezza sanitario
- Defangatore
- Attacco di scarico
- Vaso di espansione
- Gruppo di riempimento
- Pompa di calore aria-acqua
- Valvola miscelatrice termostatica
- Confine di rete
- Manometro
- Filtro a Y
- Derivazione a T
- Raccordo a T
- Pannello radiante
- Rubinetto portamanometro a tre vie
- Valvola di intercettazione
- Valvola di sicurezza
- Collettore di zona

- Acqua fredda sanitaria — andata
- Acqua calda sanitaria — andata
- Acqua di riscaldamento — andata
- Acqua di riscaldamento — ritorno

 VALORIZZAZIONE. EFFICIENTAMENTO. RIQUALIFICAZIONE.	COMMITTENTE Condominio di prova	PROGETTO Pompa di calore diretta su pavimento radiante, ACS separata	SCALA —	DATA 06.08.2026	APPROVATO Ing. Nome Cognome
	INDIRIZZO Via di Prova 1, 00000 Comune di Prova (XX)	TITOLO TAVOLA Schema funzionale della centrale termica	REVISIONE Rev. 00	COMMESSA PROVA	VERIFICATO Ing. Nome Cognome
					DISEGNATO Ing. Nome Cognome

TAVOLA
T3