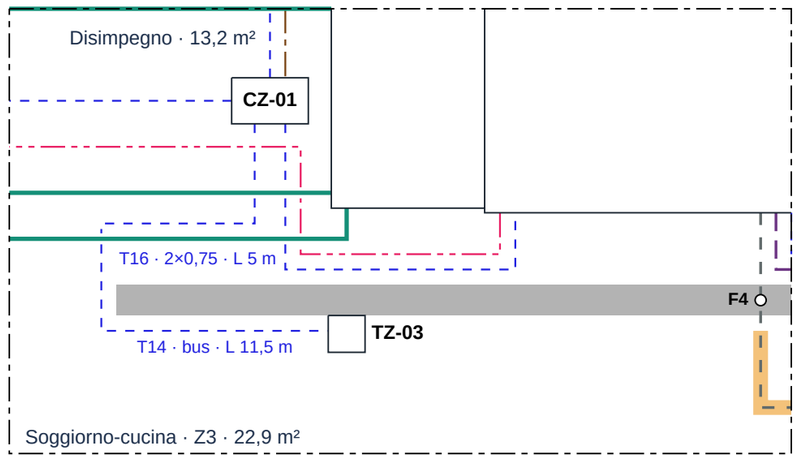


0 1 2 m

Scala 1:20

PIANTA DEI POSIZIONAMENTI E DEI TRACCIATI - DETTAGLIO A

Scala 1:20 su A3 · misure in metri

Percorsi indicativi, da verificare in sopralluogo.

LEGENDA

- Aria di mandata
- Refrigerante gas
- Refrigerante liquido
- Condensa
- Collegamento fra le unità
- Alimentazione elettrica
- Bus di comando
- Pezzo posato: ingombro e sigla
- Foratura (F1, F2…: elenco sotto)
- Fuori dal controsoffitto: da verificare

Tratte, lunghezze, forature e avvisi: tavola pianta.

NOTE

1. Quote: canali, linee frigo e condensa in controsoffitto; cavi e bus in traccia, salvo dove la tabella dice altro. Salite e discese stanno nell'aggiunta della regola.
2. Sigle e numeri di tratta come lo schema funzionale e la distinta.
3. Planimetria a parole del progettista: 11 × 8 m misure interne, muri perimetrali 30 cm fuori dal rettangolo interno, tramezze 10 cm.
4. Le tramezze del corridoio hanno le facce a y=3,4 e y=4,6 (corridoio libero 1,2 m): assi a 3,35 e 4,65.
5. Da confermare: ingombri di UI (1,10 × 0,73), plenum e ripresa; posizione dei termostati e del comando a filo; posizione del sezionatore e dell'allaccio allo scarico della cucina; la ripresa è disegnata accanto alla UI, ma sta sotto la UI.
6. La centrale di zona sta sopra il plenum: in pianta è disegnata accanto, a ovest, perché la pianta non sovrappone due pezzi.
7. T05 (ripresa) è un raccordo diretto sotto la UI: non ha tracciato.

novec
VALORIZZAZIONE. EFFICIENTAMENTO. RIQUALIFICAZIONE.

COMMITTENTE: DA DEFINIRE	PROGETTO: Canalizzato aria-aria in pompa di calore - appartamento al secondo piano	SCALA: 1:20	DATA: 29.10.2026	APPROVATO	TAVOLA: DA DEFINIRE.A
INDIRIZZO: DA DEFINIRE	TITOLO TAVOLA: Pianta dei posizionamenti e dei tracciati - dettaglio A	REVISIONE: Rev. 00	COMMESSA: DA DEFINIRE	VERIFICATO / DISEGNATO	