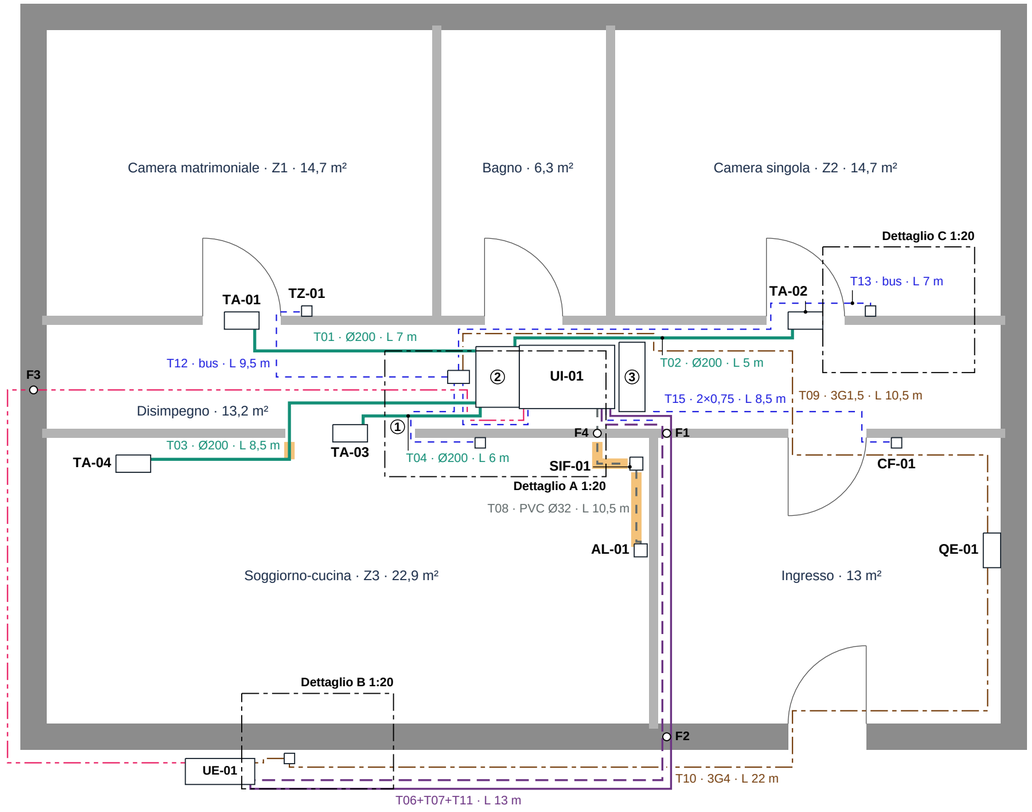


0 1 2 3 4 5 m

Scala 1:50

PIANTA DEI POSIZIONAMENTI E DEI TRACCIATI

Scala 1:50 su A2 · misure in metri

Percorsi indicativi, da verificare in sopralluogo.

LEGENDA

- Aria di mandata
- Refrigerante gas
- Refrigerante liquido
- Condensa
- Collegamento fra le unità
- Alimentazione elettrica
- Bus di comando
- Pezzo posato: ingombro e sigla
- Foratura (F1, F2…: elenco sotto)
- Fuori dal controsoffitto: da verificare
- ① Scritta in legenda (testo sotto)

TRATTE

Tratta	Fluido	Da	A	Dim.	L prog.	L mis.	L quot.
T01	Aria di mandata	PLZ-01	TA-01	Ø200	5	2,8	7
T02	Aria di mandata	PLZ-01	TA-02	Ø200	3	3,4	5
T03	Aria di mandata	PLZ-01	TA-04	Ø200	6	4,4	8,5
T04	Aria di mandata	PLZ-01	TA-03	Ø200	4	1,6	6
T06	Frigo, liquido	UI-01	UE-01	1/4"	9	10	12*
T07	Frigo, gas	UI-01	UE-01	5/8"	9	9,7	12*
T08	Condensa	UI-01	AL-01	PVC Ø32	8	1,9	10,5
T09	Alimentazione	QE-01	CZ-01	3G1,5	8	8,8	10,5
T10	Alimentazione	QE-01	UE-01	3G4	18	10,8	22
T11	Cavo UI-UE	UI-01	UE-01	4G1,5	10	12,8!	13
T12	Bus	CZ-01	TZ-01	bus	7	3	9,5
T13	Bus	CZ-01	TZ-02	bus	5	5,6	7
T14	Bus	CZ-01	TZ-03	bus	9	1,9	11,5
T15	Bus	UI-01	CF-01	2×0,75	6	3,9	8,5
T16	Bus	CZ-01	UI-01	2×0,75	2	1,4	5*

Passano per organi in linea: T08 per SIF-01; T10 per SZ-01. L prog. del progettista, si quota; L mis. sul disegno, un controllo (! oltre il 15 %); L quot. = (L + 1 m) × 1,15 per eccesso a 0,5 m, regola della distinta; * minimo (frigo 12 m, condensa 10 m, bus 5 m, ramo aria 2 m, il cavo fra le unita' segue le linee frigo + 1 m); ° sulla misura, L prog. manca.

AVVISI

– Misura oltre il 15 % di L prog.: T11 12,8 m su 10 (+28 %). Da verificare il percorso o il dato.
– Fuori dal controsoffitto (fascia arancio): T03 0,2 m; T08 1,45 m. Canalina o traccia, da verificare.
– Dettagli A 1:20, B 1:20, C 1:20 (zone incorniciate): tavole pianta-dettaglio-<lettera>, perche' a 1:50 le scritte non ci stanno.

FORATURE

F1 · T06 T07 · tramezza t-corridoio-sud · controsoffitto
F2 · T06 T07 · perimetrale m-sud · controsoffitto
F3 · T11 · perimetrale m-ovest · controsoffitto
F4 · T08 · tramezza t-corridoio-sud · controsoffitto
Fori per i pezzi a parete: TA-01, TA-02 nel muro t-corridoio-nord; TA-03 nel muro t-corridoio-sud.

SCRITTE IN LEGENDA

① T14 · bus · L 11,5 m
② PLZ-01
③ RA-01

NOTE

1. Quote: canali, linee frigo e condensa in controsoffitto; cavi e bus in traccia, salvo dove la tabella dice altro. Salite e discese stanno nell'aggiunta della regola.
2. Sigle e numeri di tratta come lo schema funzionale e la distinta.
3. Planimetria a parole del progettista: 11 × 8 m misure interne, muri perimetrali 30 cm fuori dal rettangolo interno, tramezze 10 cm.
4. Le tramezze del corridoio hanno le facce a y=3,4 e y=4,6 (corridoio libero 1,2 m): assi a 3,35 e 4,65.
5. Da confermare: ingombri di UI (1,10 × 0,73), plenum e ripresa; posizione dei termostati e del comando a filo; posizione del sezionatore e dell'allaccio allo scarico della cucina; la ripresa è disegnata accanto alla UI, ma sta sotto la UI.
6. La centrale di zona sta sopra il plenum: in pianta è disegnata accanto, a ovest, perché la pianta non sovrappone due pezzi.
7. T05 (ripresa) è un raccordo diretto sotto la UI: non ha tracciato.

novec — VALORIZZAZIONE. EFFICIENTAMENTO. RIQUALIFICAZIONE.	COMMITTENTE: DA DEFINIRE	PROGETTO: Canalizzato aria-aria in pompa di calore - appartamento al secondo piano	SCALA: 1:50	DATA: 29.10.2026	APPROVATO	TAVOLA: DA DEFINIRE
	INDIRIZZO: DA DEFINIRE	TITOLO TAVOLA: Pianta dei posizionamenti e dei tracciati	REVISIONE: Rev. 00	COMMESSA: DA DEFINIRE	VERIFICATO / DISEGNATO	