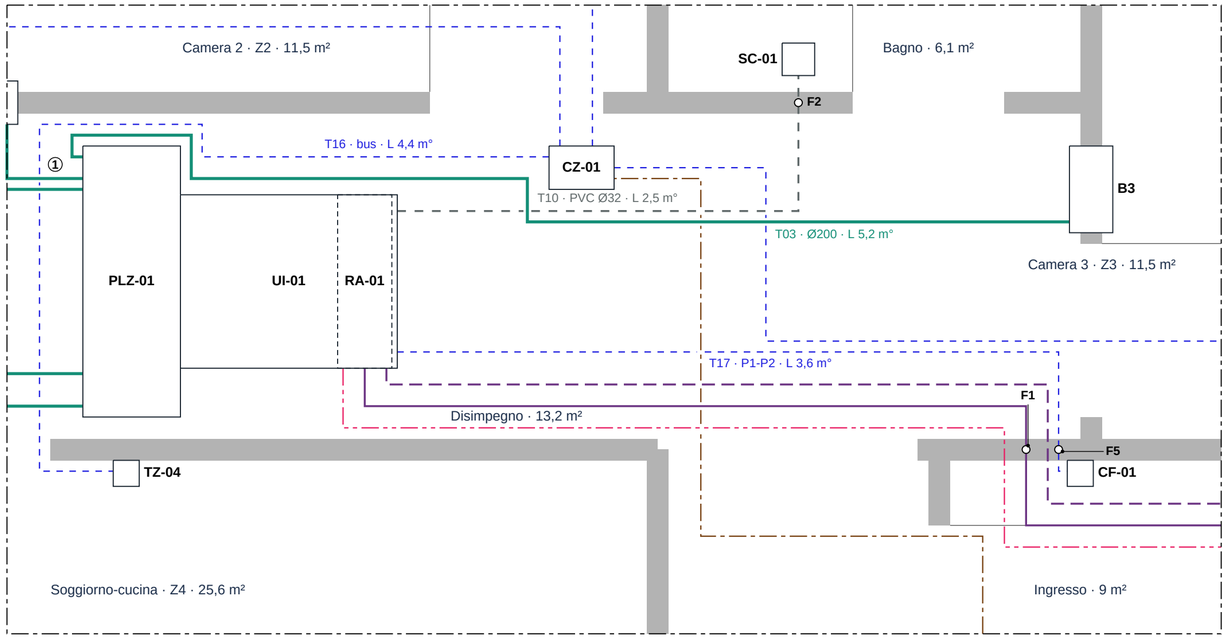


0 1 2 m

Scala 1:20

PIANTA DEI POSIZIONAMENTI E DEI TRACCIATI - DETTAGLIO A

Scala 1:20 su A2 · misure in metri

Percorsi indicativi, da verificare in sopralluogo.

LEGENDA

- Aria di mandata
- Refrigerante gas
- Refrigerante liquido
- Condensa
- Collegamento fra le unità
- Alimentazione elettrica
- Bus di comando
- Pezzo posato: ingombro e sigla
- Pezzo sotto un altro (altra quota)
- Zona esterna praticabile
- Foratura (F1, F2…: elenco sotto)
- ① Scritta in legenda (testo sotto)

Tratte, lunghezze, forature e avvisi: tavola appartamento-aria-aria.

SCRITTE IN LEGENDA

① T02 · Ø200 · L 0,6 m°

NOTE

1. Quote: canali, linee frigo e condensa in controsoffitto; cavi e bus in traccia, salvo dove la tabella dice altro. Salite e discese stanno nell'aggiunta della regola.
2. Sigle e numeri di tratta come lo schema funzionale e la distinta. Non controllati dal comando.
3. Ingombri da confermare (valori dichiarati, non del progettista ne' della scheda): CZ-01.
4. Sovrapposti, a quote diverse: RA-01 sotto UI-01.
5. Planimetria inventata per il caso di prova di REL-014: non è quella di nessun committente.
6. T06 (ripresa) è un raccordo diretto sotto la UI: non ha tracciato.
7. Il balcone è la sola zona esterna praticabile: il portoncino dà sul pianerottolo, e di lì le linee non passano.

novec — VALORIZZAZIONE. EFFICIENTAMENTO. RIQUALIFICAZIONE.	COMMITTENTE: Caso di prova (planimetria inventata)	PROGETTO: REL-014 - canalizzato aria-aria, pianta di prova	SCALA: 1:20	DATA: 29.10.2026	APPROVATO	TAVOLA: M.03.A
	INDIRIZZO: Nessun indirizzo: esempio	TITOLO TAVOLA: Pianta dei posizionamenti e dei tracciati - dettaglio A	REVISIONE: Rev. 00	COMMESSA: PROVA-REL-014	VERIFICATO DISEGNATO: Nove C	