


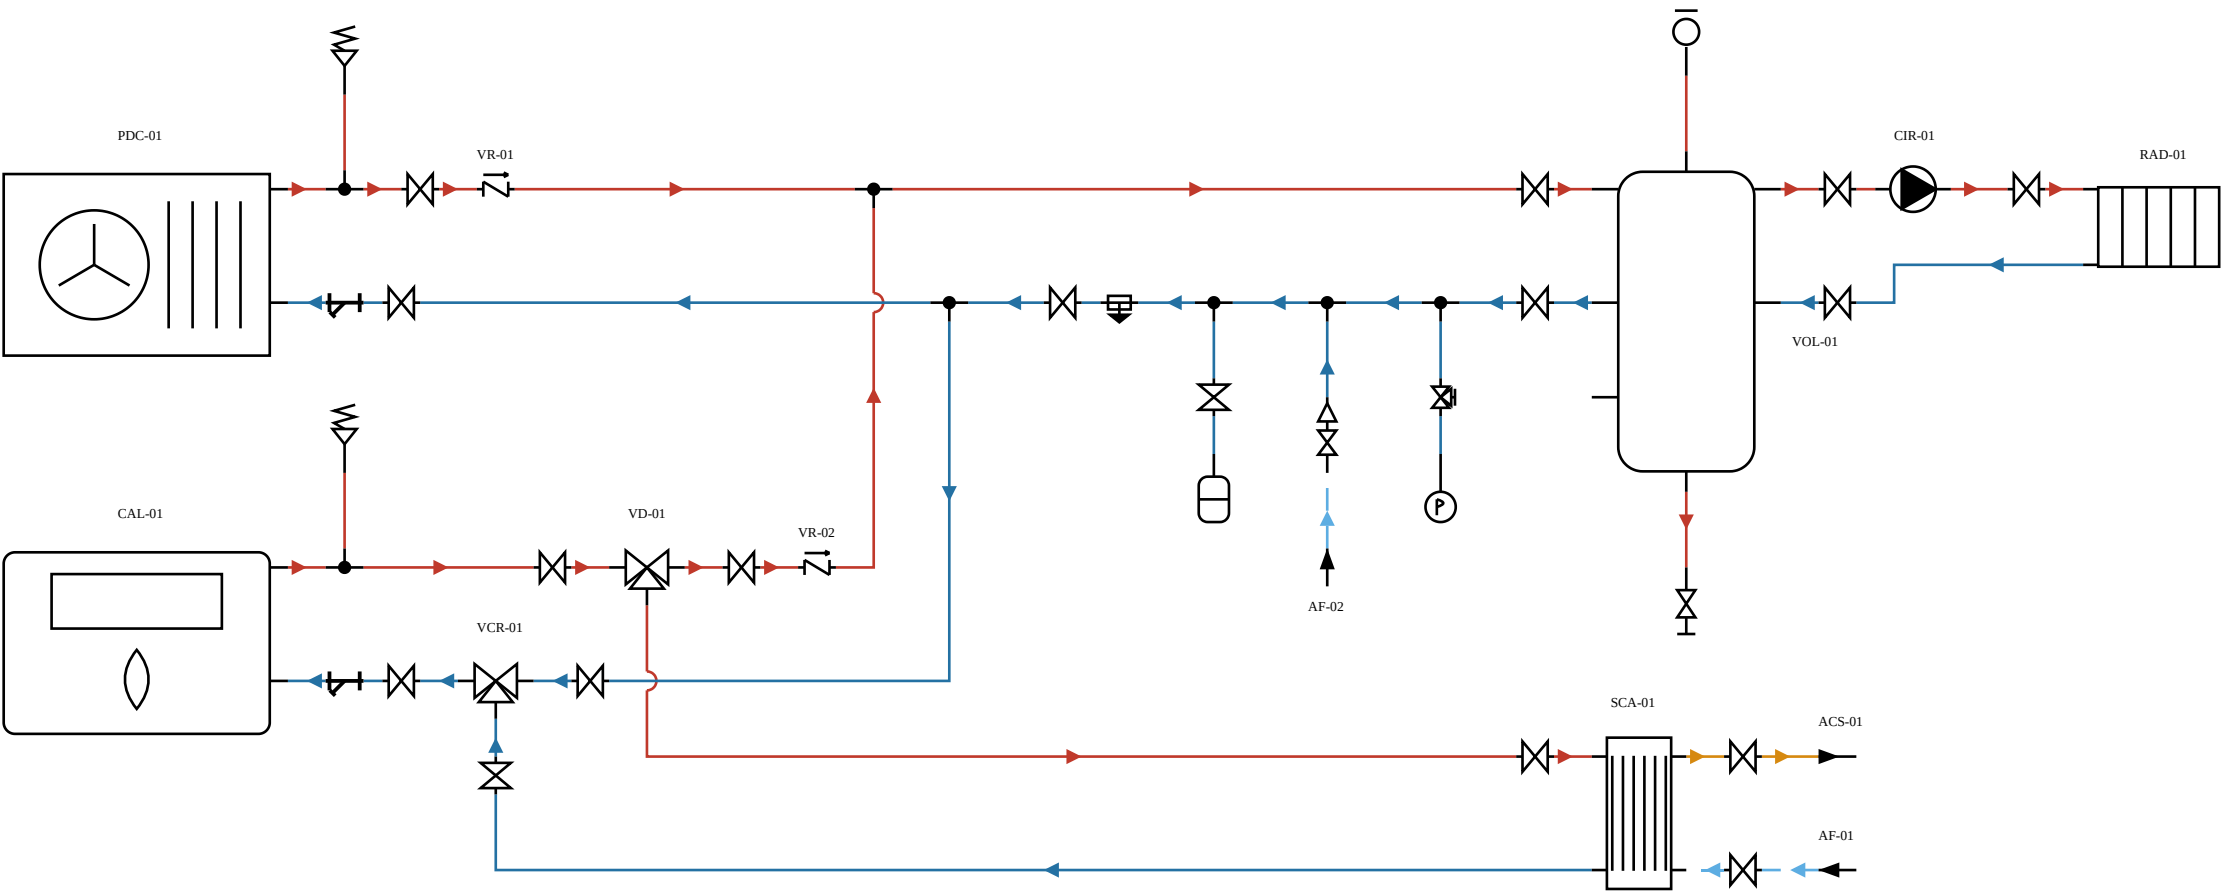

- Valvola di sfato aria
- Volano termico a quattro attacchi
- Defangatore
- Valvola deviatrice a tre vie
- Attacco di scarico
- Vaso di espansione
- Gruppo di riempimento
- Caldaia a condensazione
- Pompa di calore aria-acqua
- Confine di rete
- Scambiatore a piastre
- Manometro
- Pompa di circolazione
- Radiatore
- Filtro a Y
- Valvola commutatrice a tre vie
- Derivazione a T
- Raccordo a T
- Valvola di ritegno
- Rubinetto portamanometro a tre vie
- Valvola di intercettazione
- Valvola di sicurezza

- Acqua fredda sanitaria — andata
- Acqua calda sanitaria — andata
- Acqua di riscaldamento — andata
- Acqua di riscaldamento — ritorno