


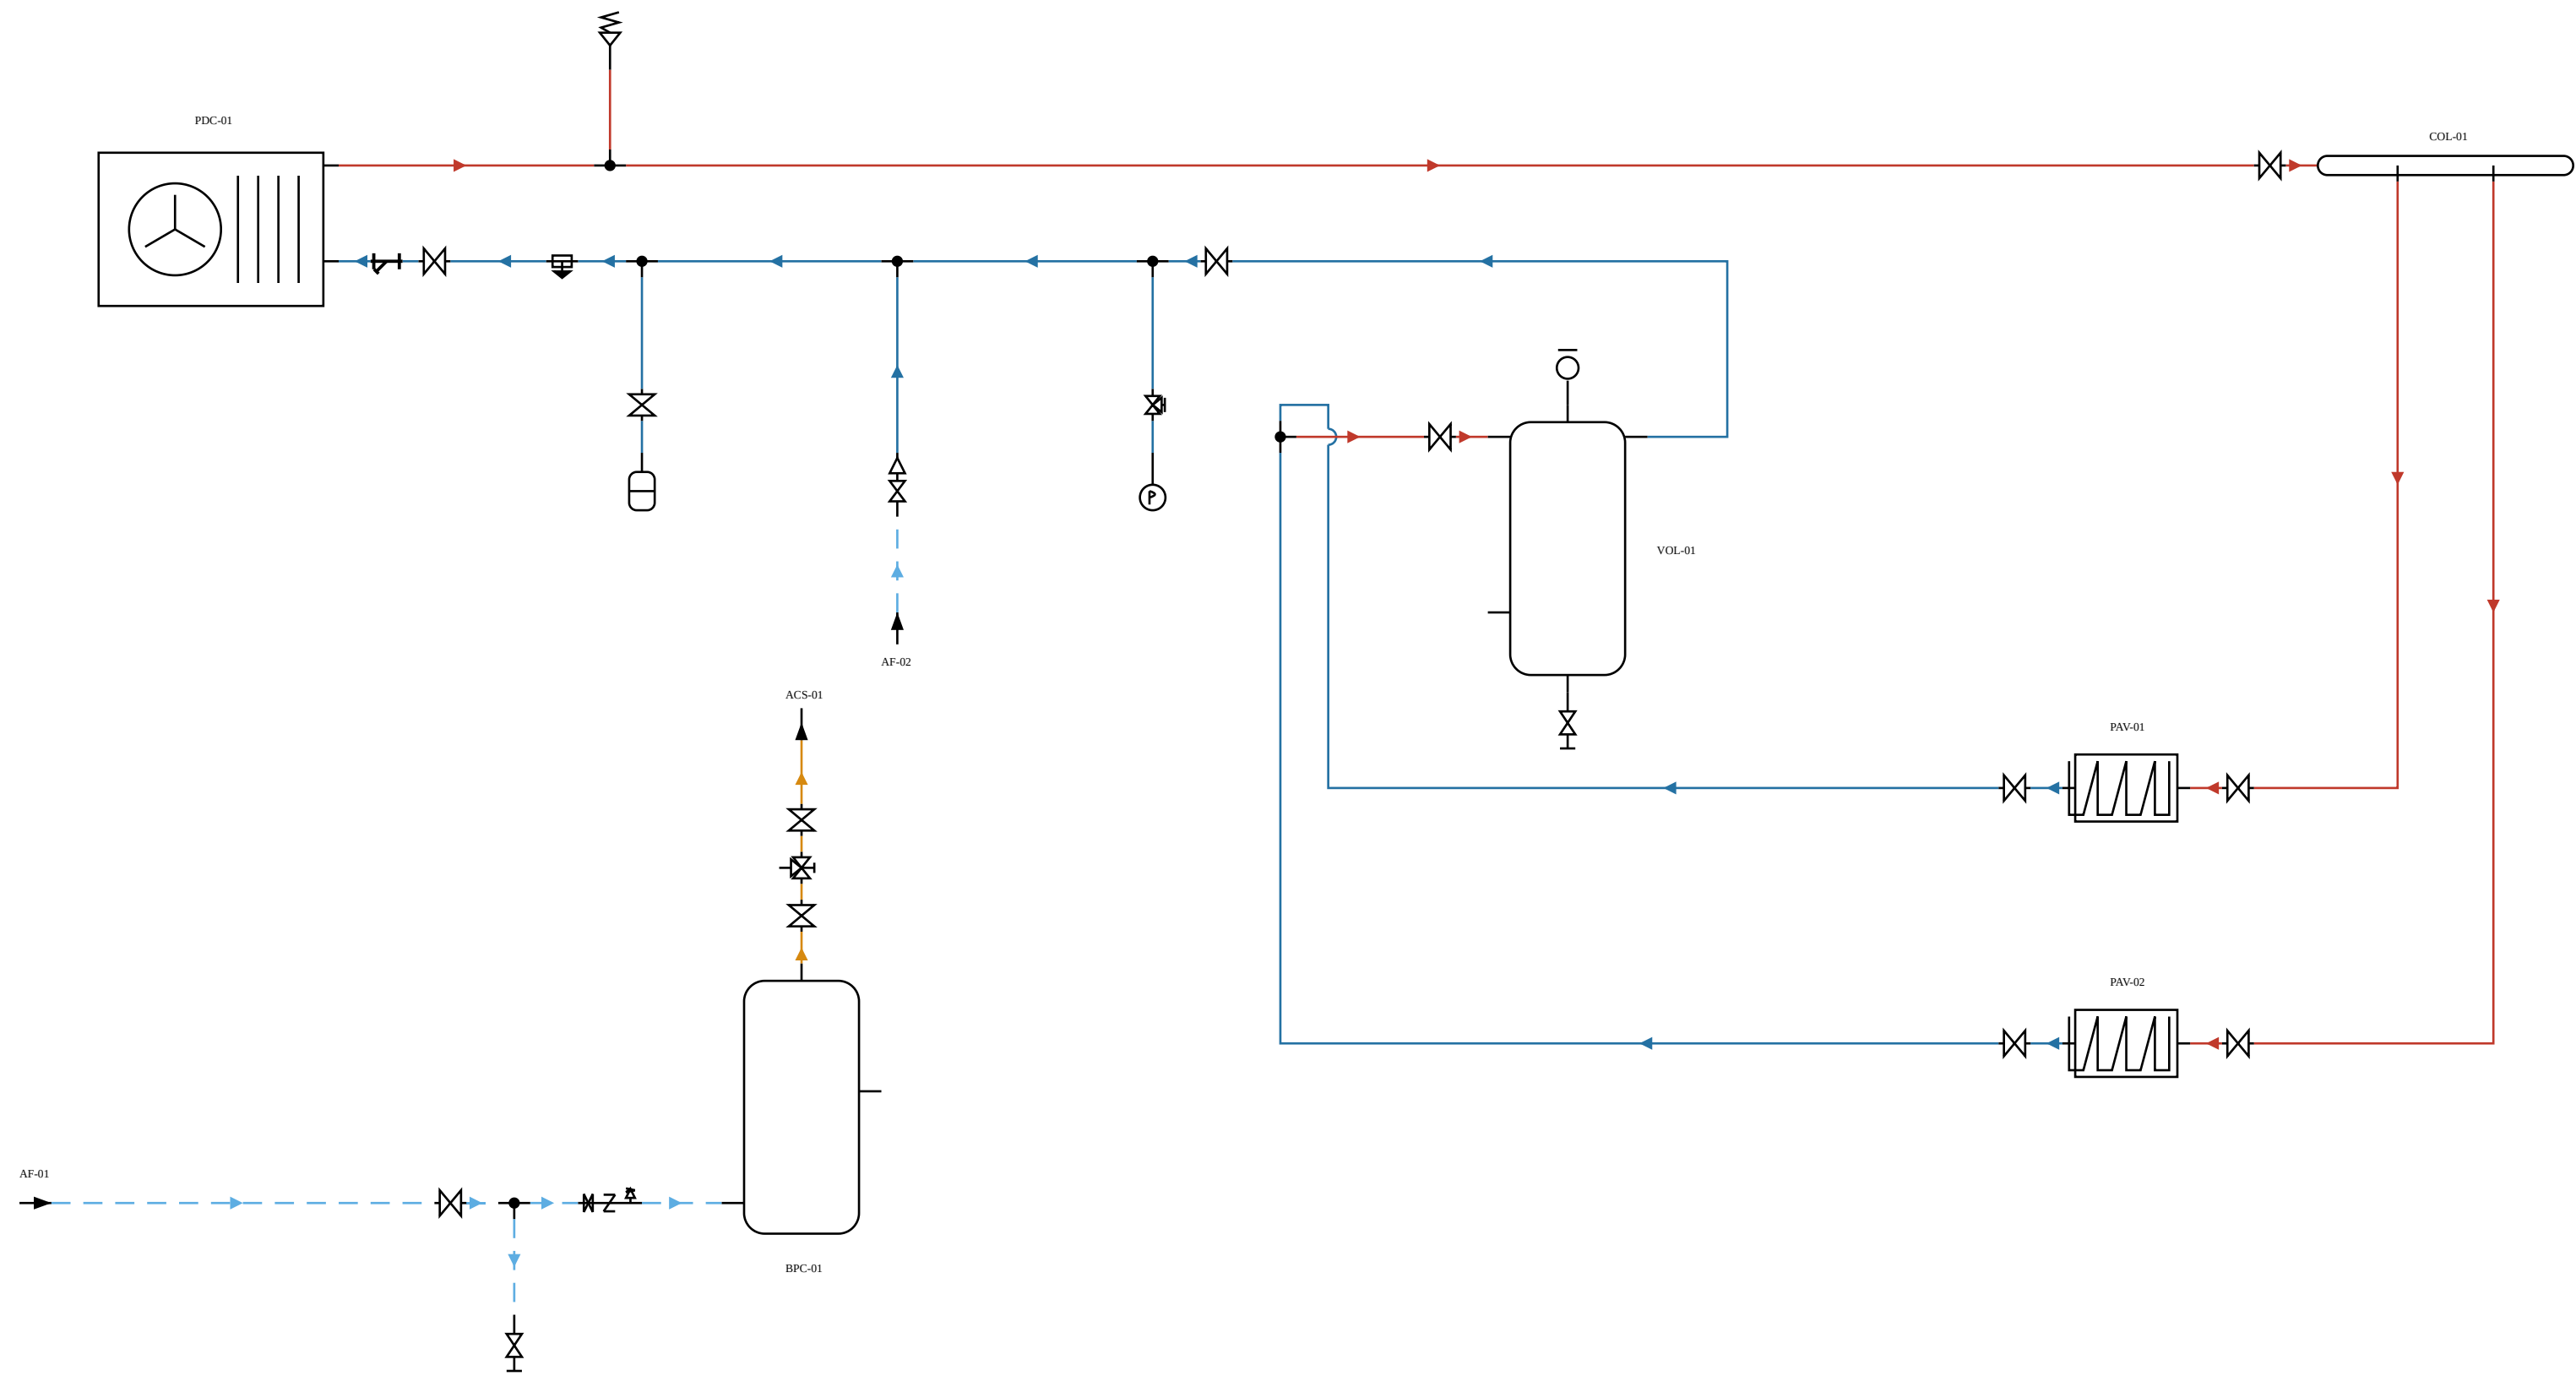

- Valvola di sfato aria
- Volano termico a due attacchi
- Boiler in pompa di calore
- Gruppo di sicurezza sanitario
- Defangatore
- Attacco di scarico
- Vaso di espansione
- Gruppo di riempimento
- Pompa di calore aria-acqua
- Valvola miscelatrice termostatica
- Confine di rete
- Manometro
- Filtro a Y
- Derivazione a T
- Raccordo a T
- Pannello radiante
- Rubinetto portamanometro a tre vie
- Valvola di intercettazione
- Valvola di sicurezza
- Collettore di zona

- Acqua fredda sanitaria — andata
- Acqua fredda sanitaria — ritorno
- Acqua calda sanitaria — andata
- Acqua calda sanitaria — ritorno
- Acqua di riscaldamento — andata
- Acqua di riscaldamento — ritorno