


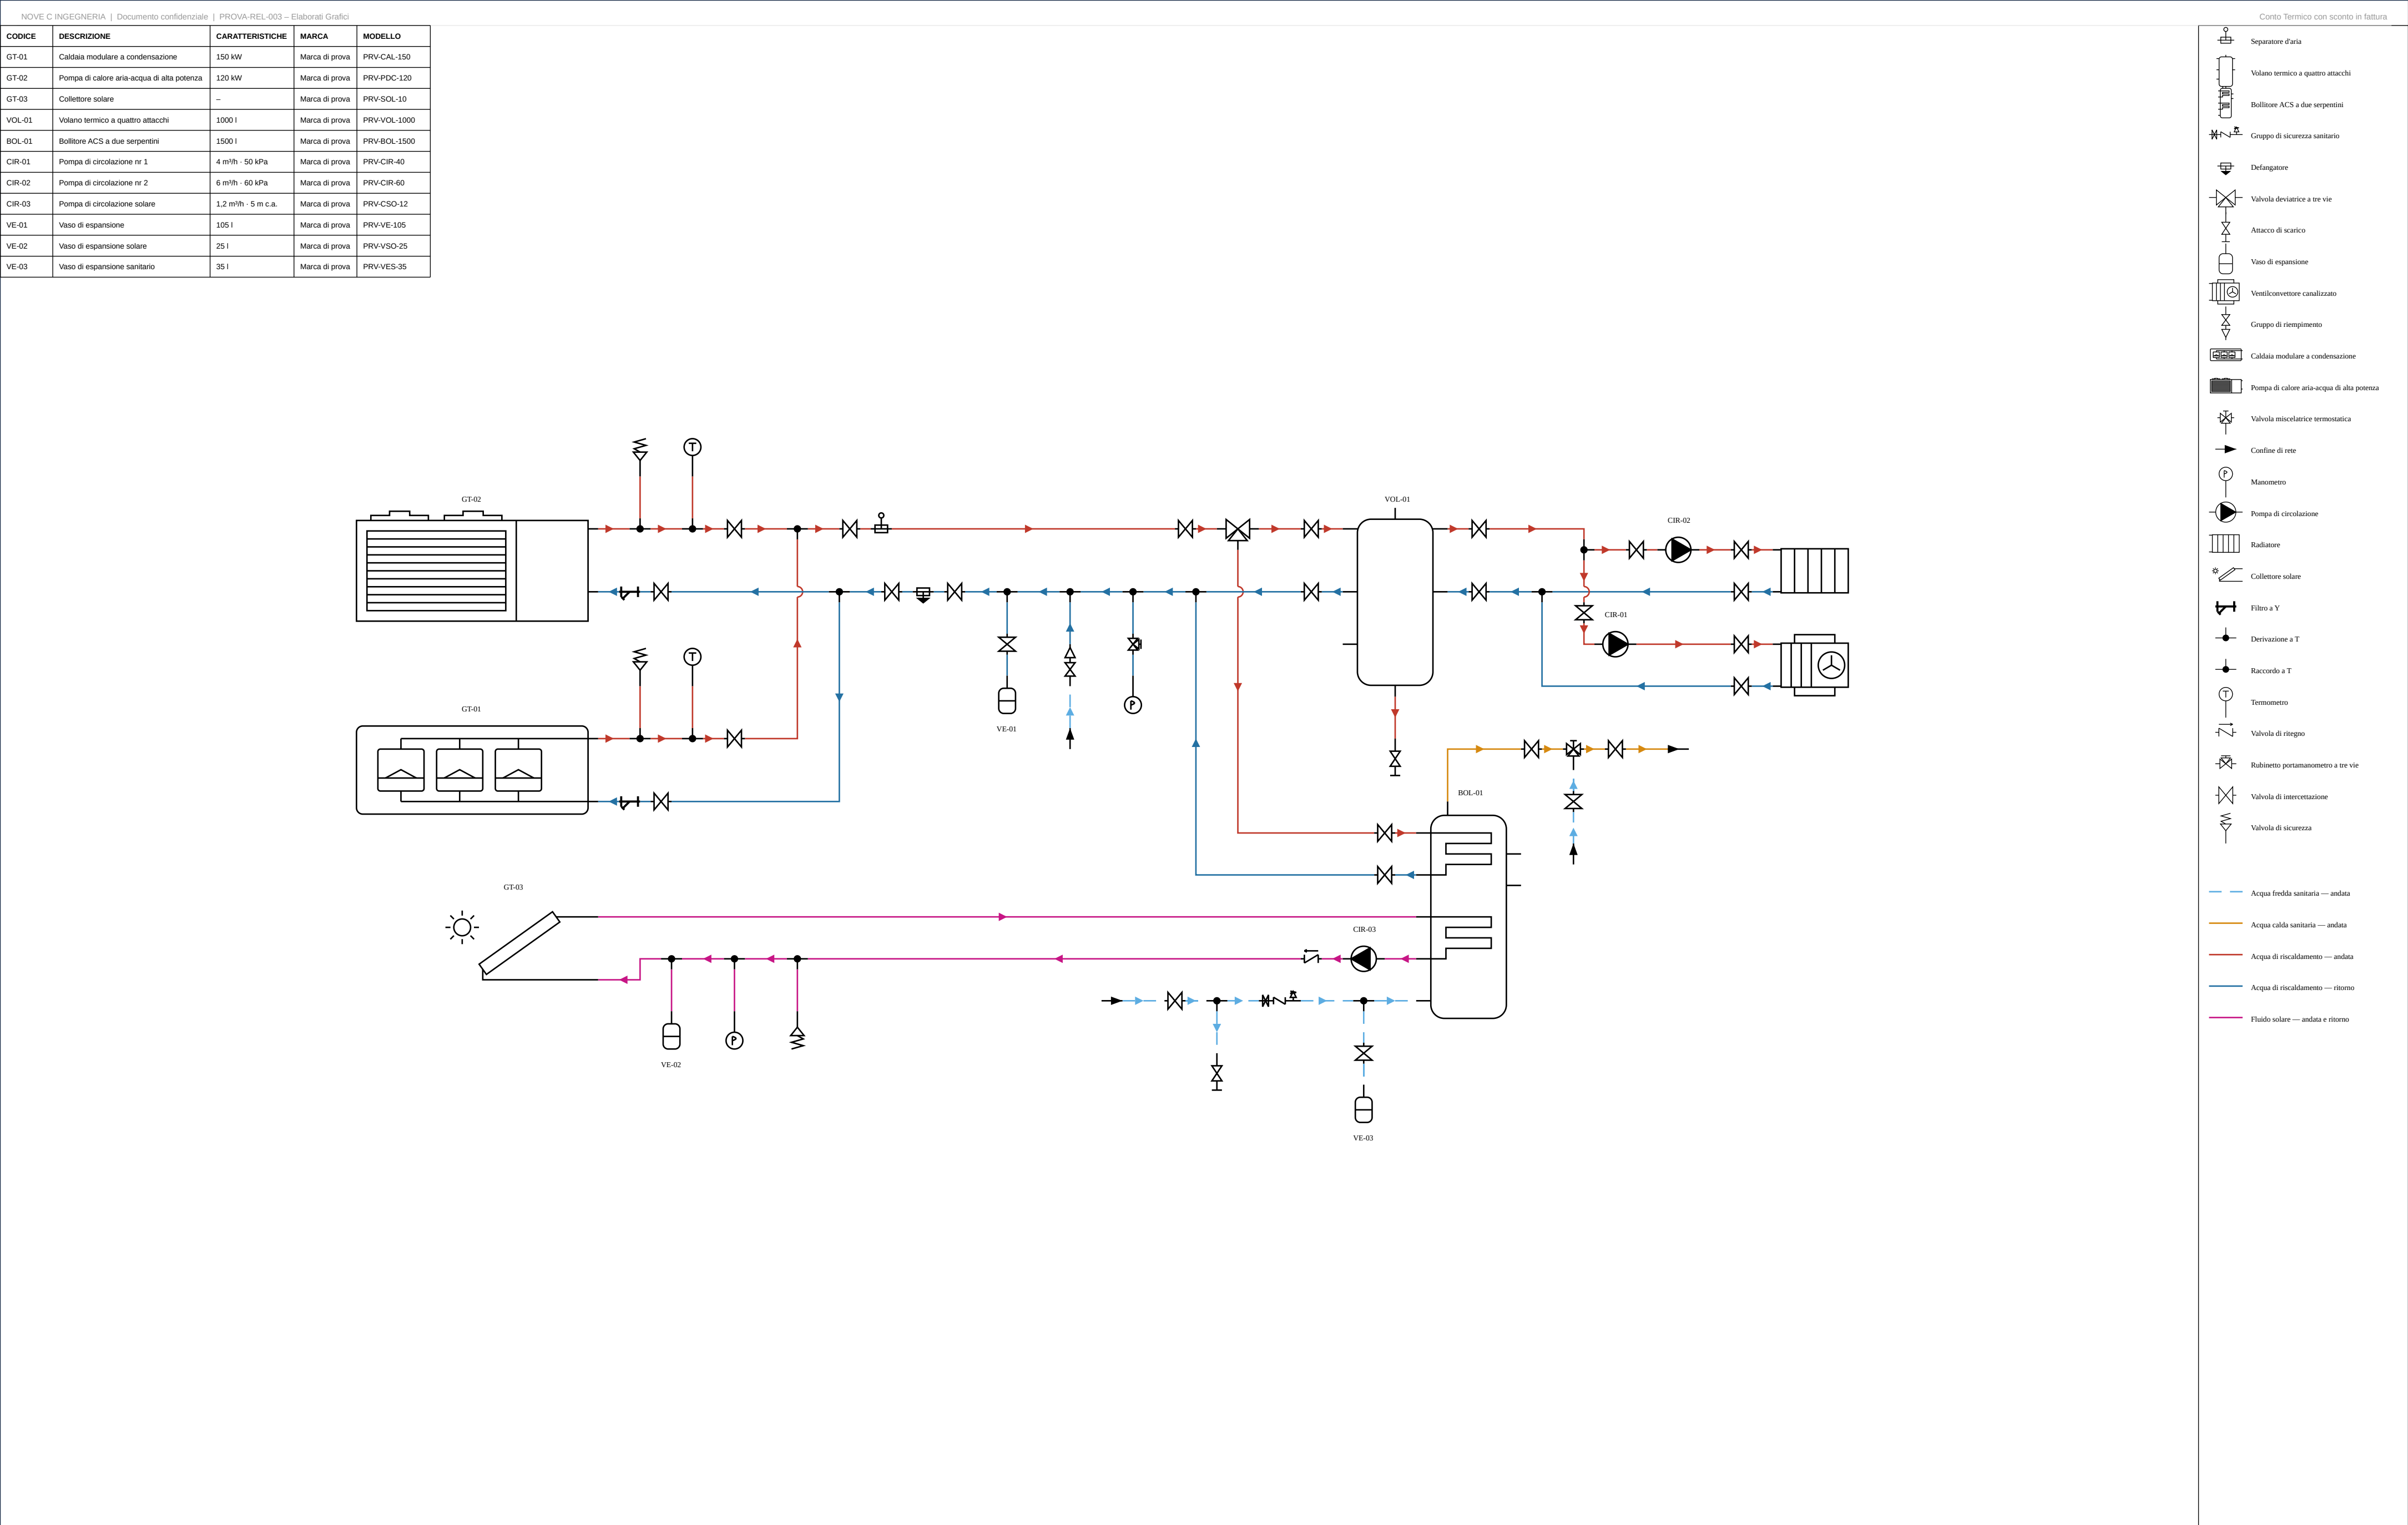

— Acqua fredda sanitaria — andata

— Acqua calda sanitaria — andata

— Acqua di riscaldamento — andata

— Acqua di riscaldamento — ritorno

— Fluido solare — andata e ritorno

VALORIZZAZIONE. EFFICIENTAMENTO. RIQUALIFICAZIONE.

COMMITTENTE

Condominio di prova

INDIRIZZO

Via di Prova 1, 00000 Comune di Prova (XX)

PROGETTO

Centrale ibrida condominiale con pompa di calore di alta potenza, caldaia modulare e solare termico

TITOLO TAVOLA

Schema funzionale della centrale termica

SCALA

—

DATA

26.09.2026

APPROVATO

VERIFICATO

COMMESSA

PROVA-REL-003

REVISIONE

Rev. 00

DISEGNATO

TAVOLA

T6