


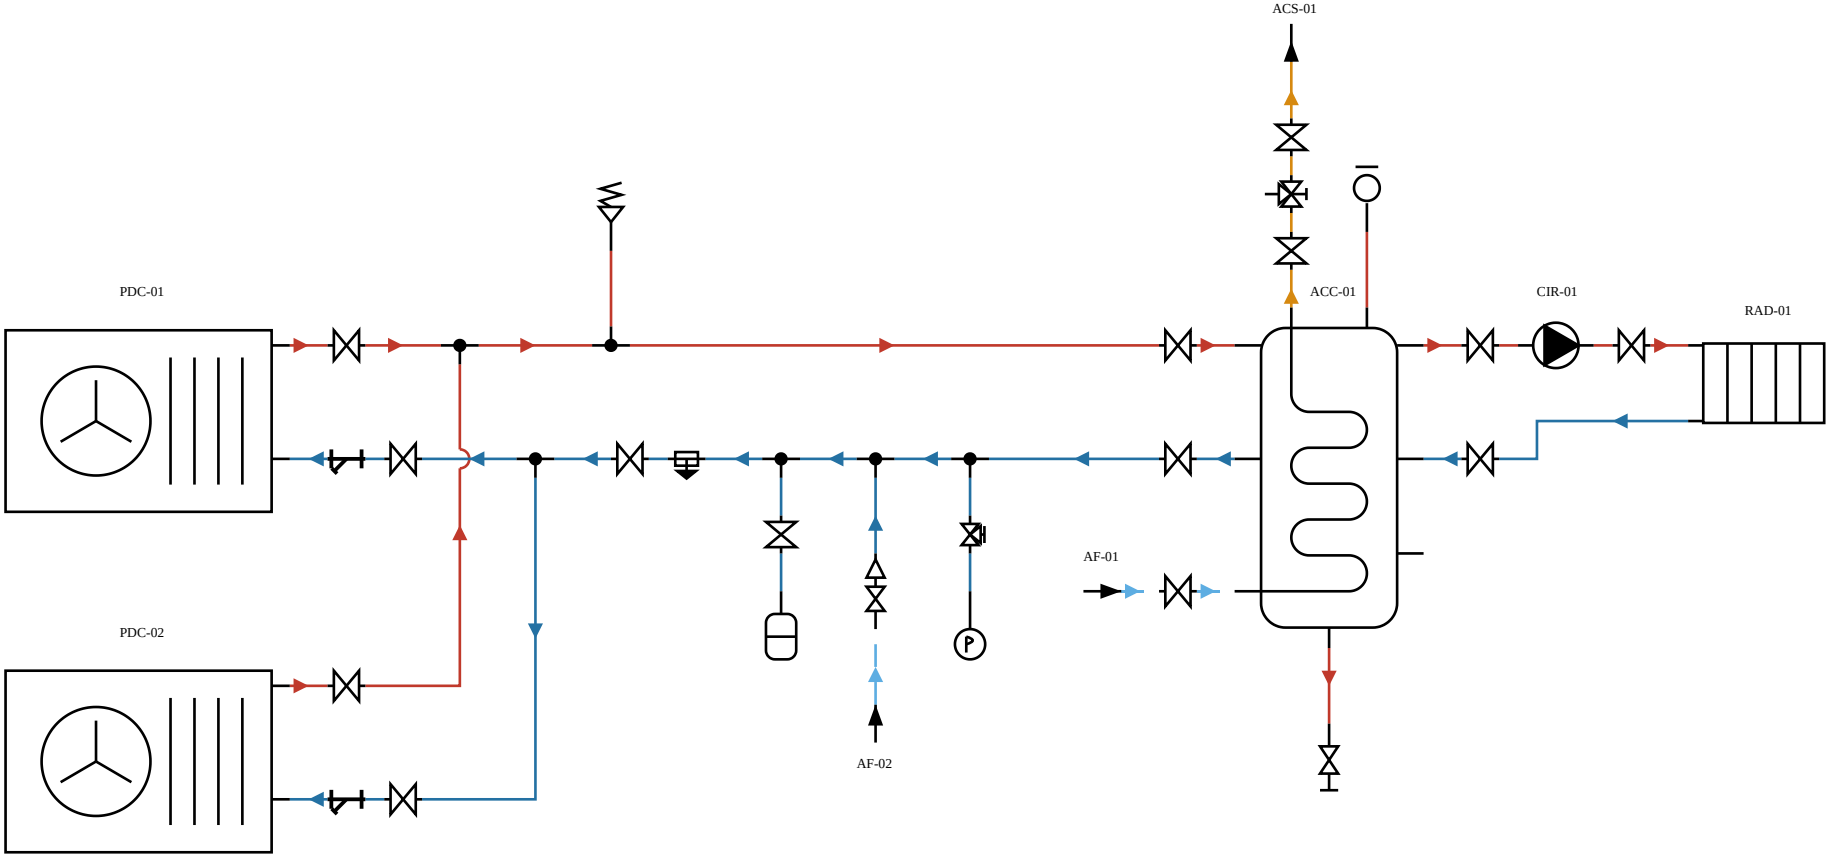

- Valvola di sfato aria
- Accumulo combinato
- Defangatore
- Attacco di scarico
- Vaso di espansione
- Gruppo di riempimento
- Pompa di calore aria-acqua
- Valvola miscelatrice termostatica
- Confine di rete
- Manometro
- Pompa di circolazione
- Radiatore
- Filtro a Y
- Derivazione a T
- Raccordo a T
- Rubinetto portamanometro a tre vie
- Valvola di intercettazione
- Valvola di sicurezza
- Acqua fredda sanitaria — andata
- Acqua calda sanitaria — andata
- Acqua di riscaldamento — andata
- Acqua di riscaldamento — ritorno