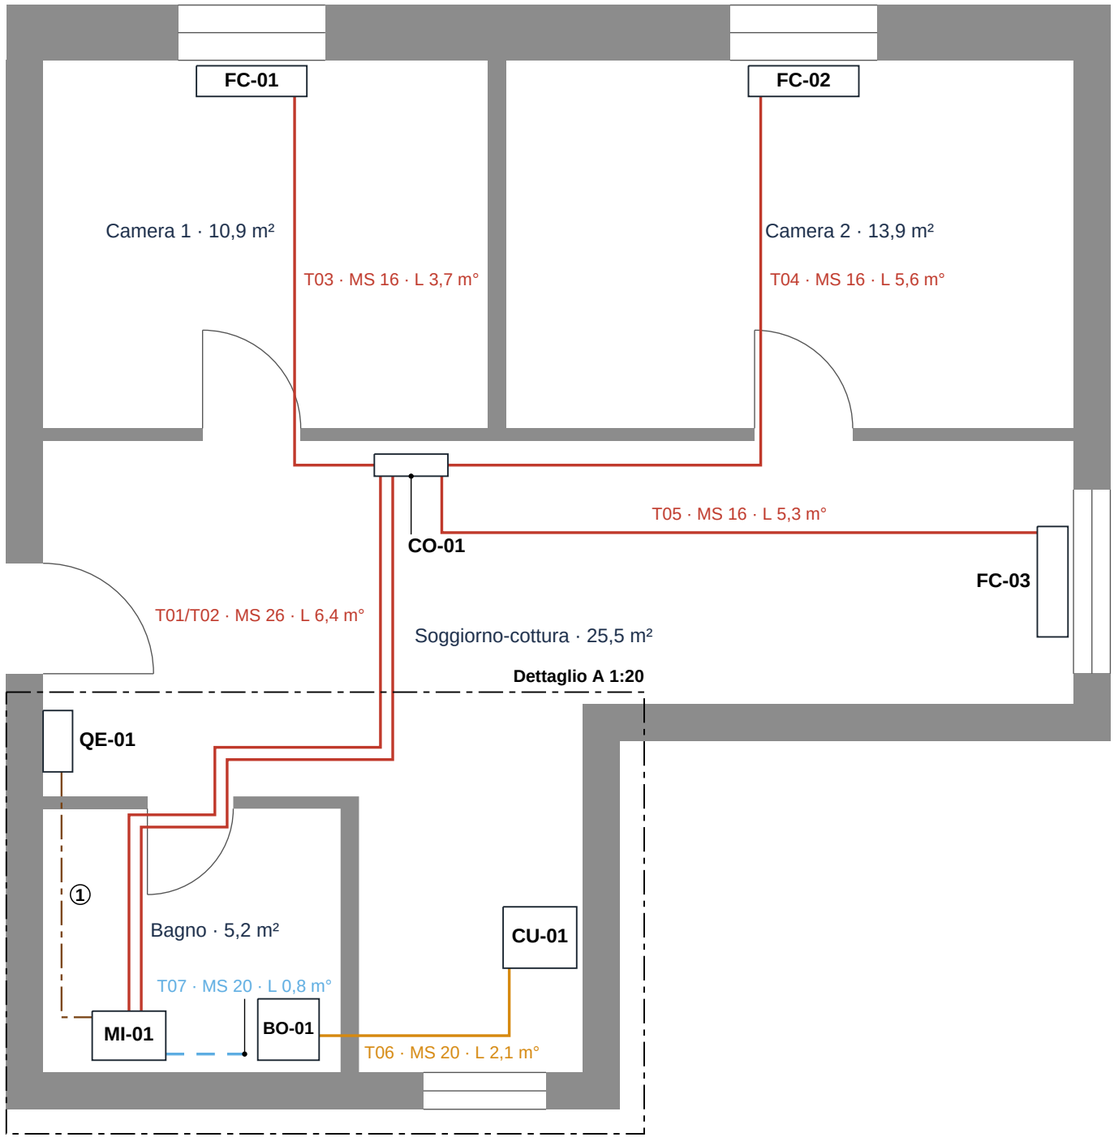


0 1 2 3 4 5 m

Scala 1:50

PIANTA DEI POSIZIONAMENTI E DEI TRACCIATI

Scala 1:50 su A3 · misure in metri

Percorsi indicativi, da verificare in sopralluogo.

LEGENDA

- Acqua fredda sanitaria
- Acqua calda sanitaria
- Acqua di riscaldamento
- Alimentazione elettrica
- Pezzo posato: ingombro e sigla
- ① Scritta in legenda (testo sotto)

TRATTE

Tratta	Fluido	Da	A	Dim.	L prog.	L mis.	L quot.
T01	Acqua risc.	MI-01	CO-01	MS 26	—	6,4	9°
T02	Acqua risc.	MI-01	CO-01	MS 26	—	6,4	9°
T03	Acqua risc.	CO-01	FC-01	MS 16	—	3,7	5,5°
T04	Acqua risc.	CO-01	FC-02	MS 16	—	5,6	8°
T05	Acqua risc.	CO-01	FC-03	MS 16	—	5,3	7,5°
T06	ACS	BO-01	CU-01	MS 20	—	2,1	4°
T07	AFS	MI-01	BO-01	MS 20	—	0,8	2,5°
T08	Alimentazione	QE-01	MI-01	3G2,5	—	2,2	4°

L prog. del progettista, si quota; L mis. sul disegno, un controllo (! oltre il 15 %); L quot. = (L + 1 m) × 1,15 per eccesso a 0,5 m, regola della distinta; * minimo (frigo 12 m, condensa 10 m, bus 5 m, ramo aria 2 m, il cavo fra le unita' segue le linee frigo + 1 m); ° sulla misura, L prog. manca.

AVVISI

– Senza L prog., quotate sulla misura (°): tutte le tratte. Da riportare nel grafo, o da chiedere.
– Dettagli A 1:20 (zone incorniciate): tavole sagome-muri-dettaglio-<lettera>.

SCRITTE IN LEGENDA

① T08 · 3G2,5 · L 2,2 m°

NOTE

1. Quote: canali, linee frigo e condensa in controsoffitto; cavi e bus in traccia, salvo dove la tabella dice altro. Salite e discese stanno nell'aggiunta della regola.
2. Sigle e numeri di tratta come lo schema funzionale e la distinta. Non controllati dal comando.
3. Caso di prova anonimo (REL-026, B-2): planimetria inventata, un appartamento a L con muri di spessori diversi.
4. Il retino dei muri sta sulle sagome vere (sagome_muri); i muri asse-spessore restano per l'instradamento.

novec
VALORIZZAZIONE. EFFICIENTAMENTO. RIQUALIFICAZIONE.

COMMITTENTE: Caso di prova (planimetria inventata)	PROGETTO: REL-026 - le sagome dei muri	SCALA: 1:50	DATA: 13.11.2026	APPROVATO	TAVOLA	
INDIRIZZO: Nessun indirizzo: esempio	TITOLO TAVOLA: Pianta dei posizionamenti e dei tracciati	REVISIONE: Rev. 00	COMMESSA: PROVA-REL-026	VERIFICATO		M.03
				DISEGNATO: Nove C		