


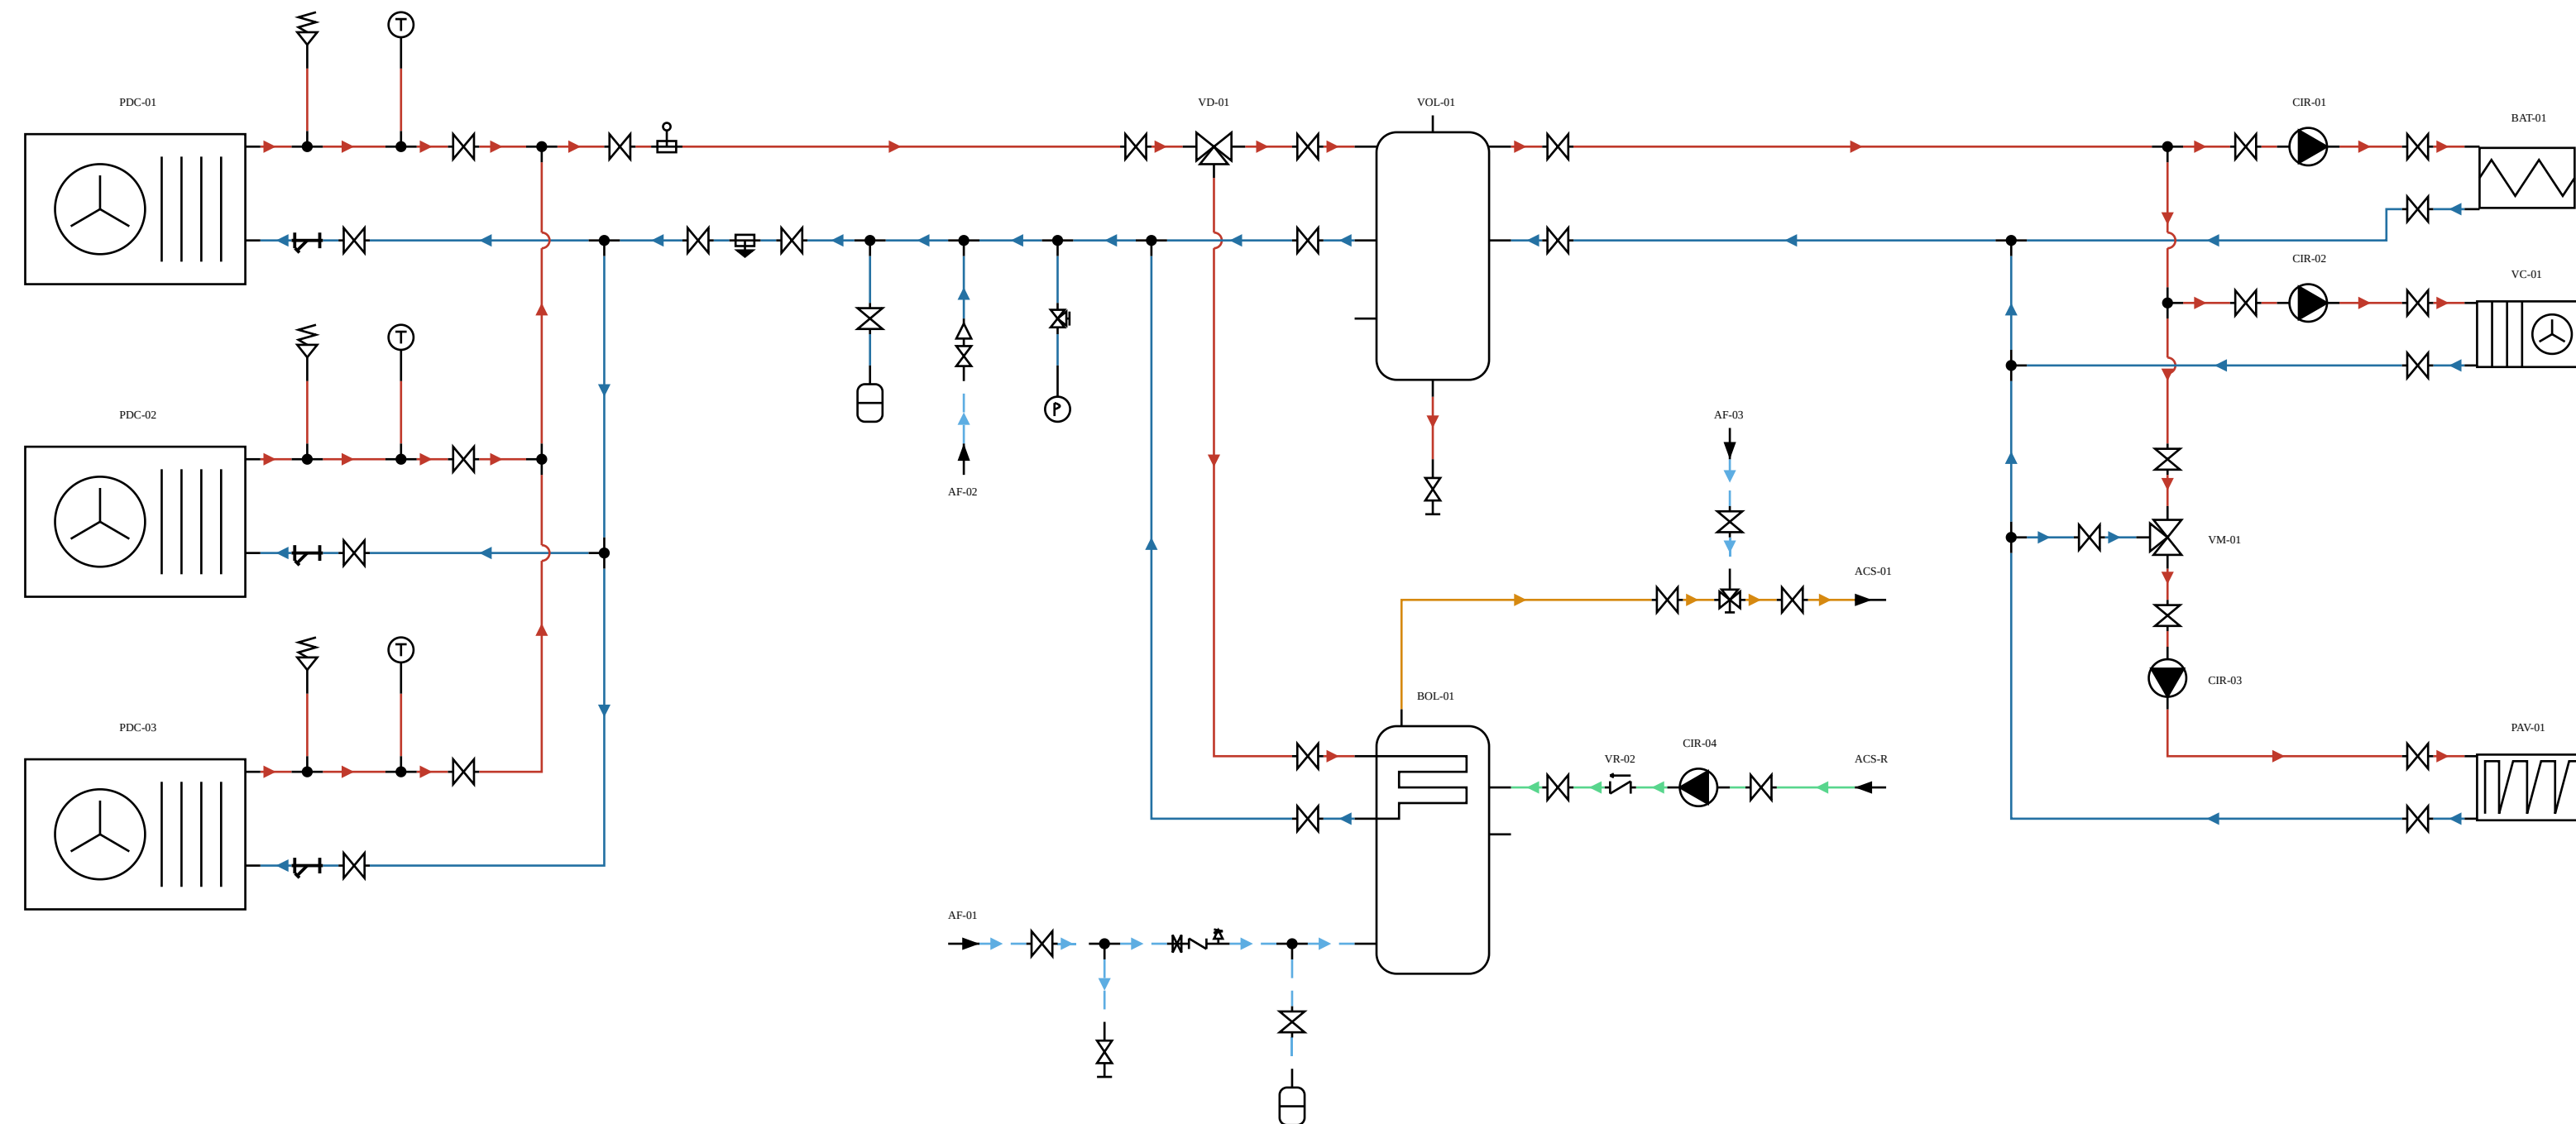

- | | |
|--|------------------------------------|
| | Batteria di trattamento aria |
| | Separatore d'aria |
| | Valvano termico a quattro attacchi |
| | Bollitore ACS |
| | Gruppo di sicurezza sanitario |
| | Defangatore |
| | Valvola deviatrice a tre vie |
| | Attacco di scarico |
| | Vaso di espansione |
| | Ventilconvettore |
| | Gruppo di riempimento |
| | Pompa di calore aria-acqua |
| | Valvola miscelatrice a tre vie |
| | Valvola miscelatrice termostatica |
| | Confine di rete |
| | Manometro |
| | Pompa di circolazione |
| | Filtro a Y |
| | Derivazione a T |
| | Raccordo a T |
| | Termometro |
| | Pannello radiante |
| | Valvola di ritegno |
| | Rubinetto portamanometro a tre vie |
| | Valvola di intercettazione |
| | Valvola di sicurezza |

- Acqua fredda sanitaria — andata
- Acqua calda sanitaria — andata
- Acqua calda sanitaria — ricircolo
- Acqua di riscaldamento — andata
- Acqua di riscaldamento — ritorno