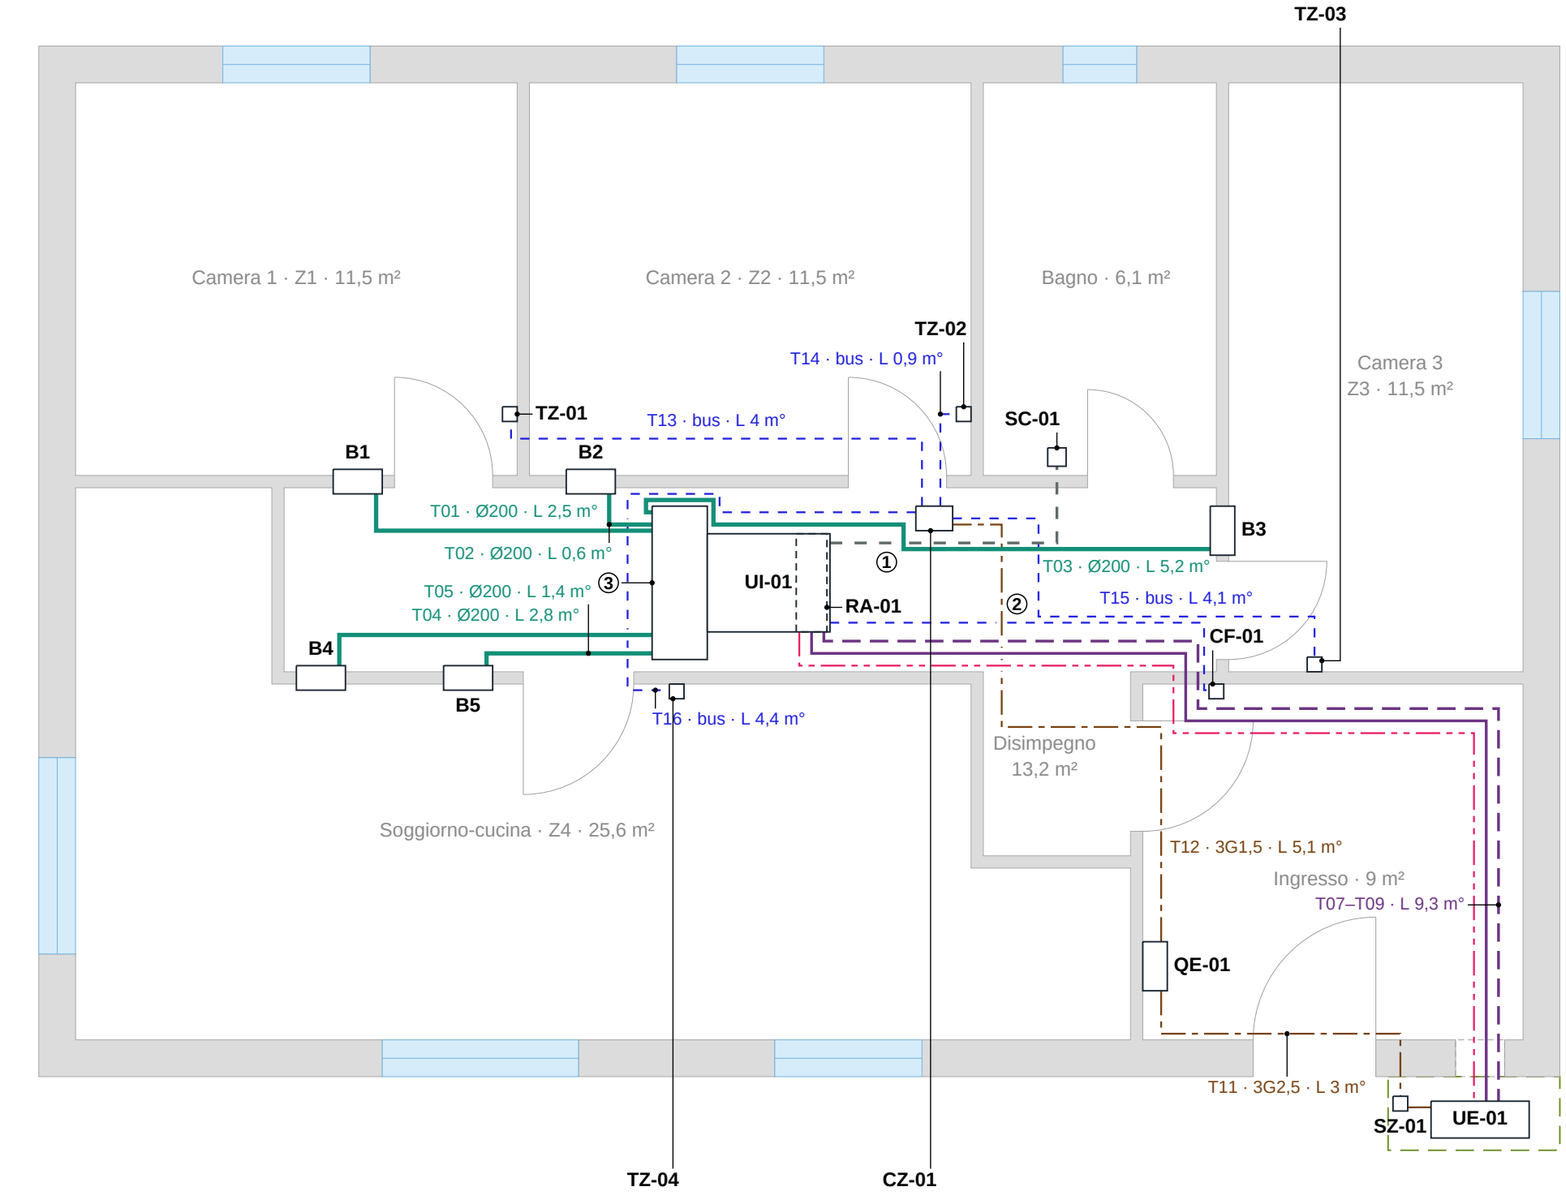


PIANTA DEI POSIZIONAMENTI E DEI TRACCIATI

Scala 1:50 su A3 · misure in metri

Percorsi indicativi, da verificare in sopralluogo.

LEGENDA

- Aria di mandata
- Refrigerante gas
- Refrigerante liquido
- Condensa
- Collegamento fra le unità
- Alimentazione elettrica
- Bus di comando
- Pezzo posato: ingombro e sigla
- Pezzo sotto un altro (altra quota)
- Zona esterna praticabile
- ① Scritta in legenda (testo sotto)

TRATTE

Tratta	Fluido	Da	A	Dim.	L prog.	L mis.	L quot.
T01	Aria di mandata	PLZ-01	B1	Ø200	—	2,5	4,5°
T02	Aria di mandata	PLZ-01	B2	Ø200	—	0,6	2°
T03	Aria di mandata	PLZ-01	B3	Ø200	—	5,2	7,5°
T04	Aria di mandata	PLZ-01	B4	Ø200	—	2,8	4,5°
T05	Aria di mandata	PLZ-01	B5	Ø200	—	1,4	3°
T07	Frigo, liquido	UI-01	UE-01	6,35	—	9,3	12°
T08	Frigo, gas	UI-01	UE-01	12,7	—	9,3	12°
T09	Cavo UI-UE	UI-01	UE-01	4G1,5	—	9,3	13*°
T10	Condensa	UI-01	SC-01	PVC Ø32	—	2,5	10*°
T11	Alimentazione	QE-01	UE-01	3G2,5	—	3	5°
T12	Alimentazione	QE-01	CZ-01	3G1,5	—	5,1	7,5°
T13	Bus	CZ-01	TZ-01	bus	—	4	6°
T14	Bus	CZ-01	TZ-02	bus	—	0,9	5*°
T15	Bus	CZ-01	TZ-03	bus	—	4,1	6°
T16	Bus	CZ-01	TZ-04	bus	—	4,4	6,5°
T17	Bus	UI-01	CF-01	P1-P2	—	3,6	5,5°

Passano per organi in linea: T11 per SZ-01. L prog. del progettista, si quota; L mis. sul disegno, un controllo (! oltre il 15 %); L quot. = (L + 1 m) × 1,15 per eccesso a 0,5 m, regola della distinta; * minimo (frigo 12 m, condensa 10 m, bus 5 m, ramo aria 2 m, il cavo fra le unita' segue le linee frigo + 1 m); ° sulla misura, L prog. manca.

AVVISI

– Senza L prog., quotate sulla misura (°): tutte le tratte. Da riportare nel grafo, o da chiedere.

SCRITTE IN LEGENDA

① T10 · PVC Ø32 · L 2,5 m°
② T17 · P1-P2 · L 3,6 m°
③ PLZ-01

NOTE

1. Quote: canali, linee frigo e condensa in controsoffitto; cavi e bus in traccia, salvo dove la tabella dice altro. Salite e discese stanno nell'aggiunta della regola.
2. Sigle e numeri di tratta come lo schema funzionale e la distinta. Non controllati dal comando.
3. Ingombri da confermare (valori dichiarati, non del progettista ne' della scheda): CZ-01.
4. Sovrapposti, a quote diverse: RA-01 sotto UI-01.
5. Planimetria inventata per il caso di prova di REL-014: non è quella di nessun committente.
6. T06 (ripresa) è un raccordo diretto sotto la UI: non ha tracciato.
7. Il balcone è la sola zona esterna praticabile: il portoncino dà sul pianerottolo, e di lì le linee non passano.

VALORIZZAZIONE. EFFICIENTAMENTO. RIQUALIFICAZIONE.

COMMITTENTE: Caso di prova (planimetria inventata)	PROGETTO: REL-014 - canalizzato aria-aria, pianta di prova	SCALA: 1:50	DATA: 29.10.2026	APPROVATO	TAVOLA: M.03
INDIRIZZO: Nessun indirizzo: esempio	TITOLO TAVOLA: Pianta dei posizionamenti e dei tracciati	REVISIONE: Rev. 00	COMMESSA: PROVA-REL-014	VERIFICATO DISEGNATO: Nove C	