


GT-01

VE-01

P

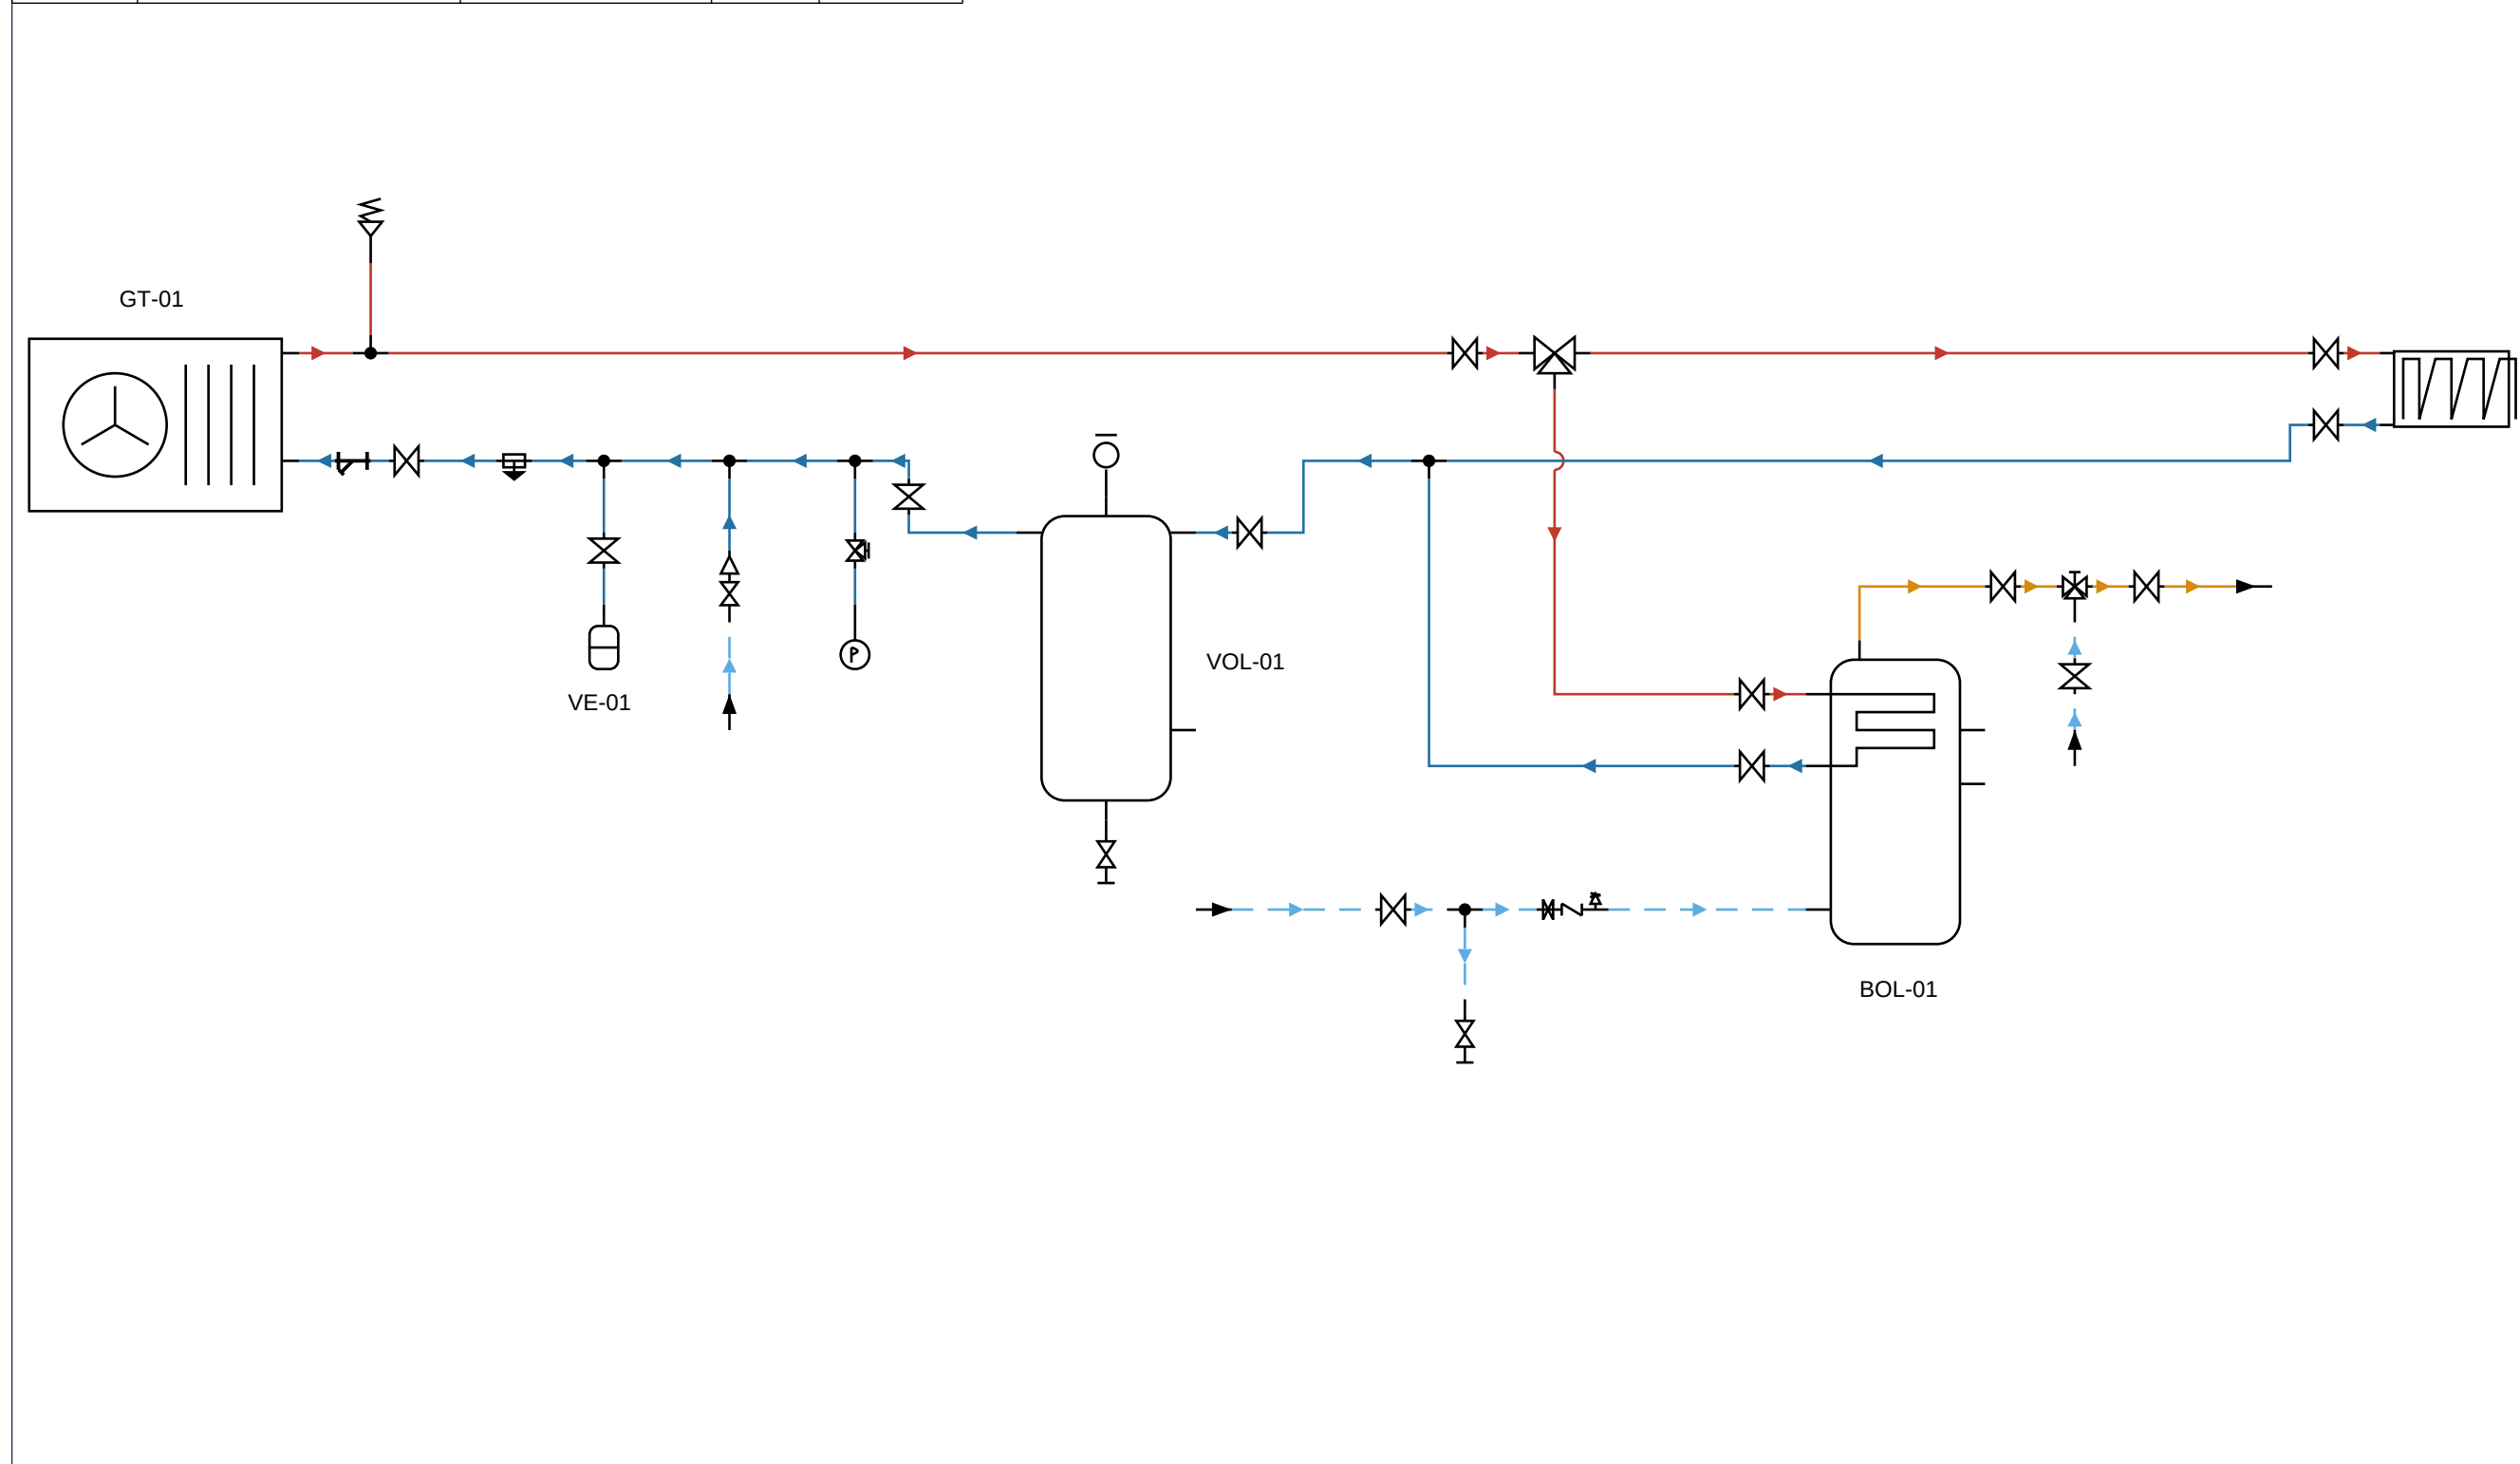

- | | |
|---|--|
|  | Valvola di sfiato aria |
|  | Volano termico
a due attacchi |
|  | Bollitore ACS |
|  | Gruppo di
sicurezza sanitario |
|  | Defangatore |
|  | Valvola deviatrice
a tre vie |
|  | Attacco di scarico |
|  | Vaso di espansione |
|  | Gruppo di riempimento |
|  | Pompa di calore
aria-acqua |
|  | Valvola miscelatrice
termostatica |
|  | Confine di rete |
|  | Manometro |
|  | Filtro a Y |
|  | Derivazione a T |
|  | Raccordo a T |
|  | Pannello radiante |
|  | Rubinetto
portamanometro a tre vie |
|  | Valvola di intercettazione |
|  | Valvola di sicurezza |
|  | Acqua fredda
sanitaria — andata
Acqua calda
sanitaria — andata
Acqua di
riscaldamento — andata
Acqua di
riscaldamento — ritorno |