


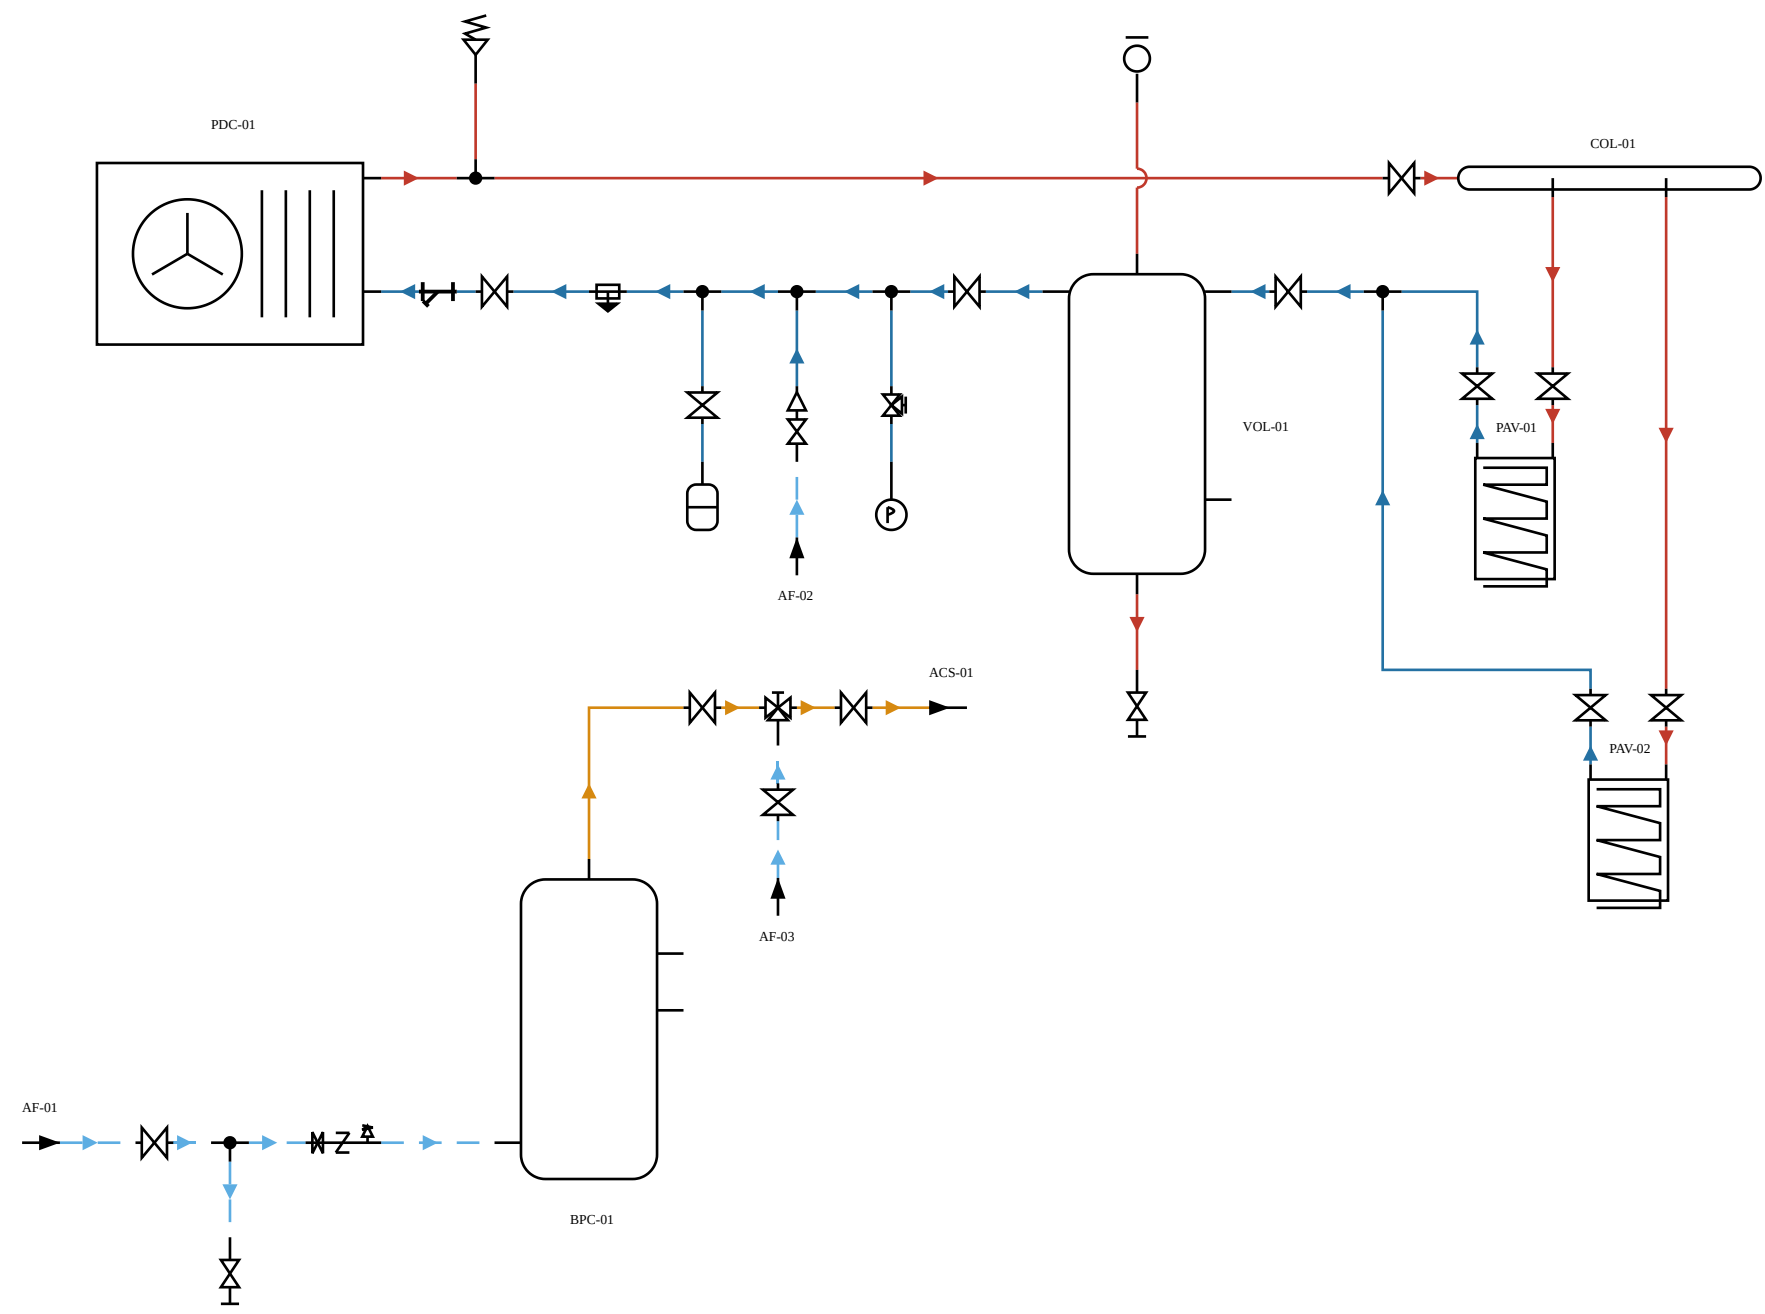

	Valvola di sfato aria
	Valano termico a due attacchi
	Boiler in pompa di calore
	Gruppo di sicurezza sanitario
	Defangatore
	Attacco di scarico
	Vaso di espansione
	Gruppo di riempimento
	Pompa di calore aria-acqua
	Valvola miscelatrice termostatica
	Confine di rete
	Manometro
	Filtro a Y
	Derivazione a T
	Raccordo a T
	Pannello radiante
	Rubinetto portamanometro a tre vie
	Valvola di intercettazione
	Valvola di sicurezza
	Collettore di zona
	Acqua fredda sanitaria — andata
	Acqua calda sanitaria — andata
	Acqua di riscaldamento — andata
	Acqua di riscaldamento — ritorno