


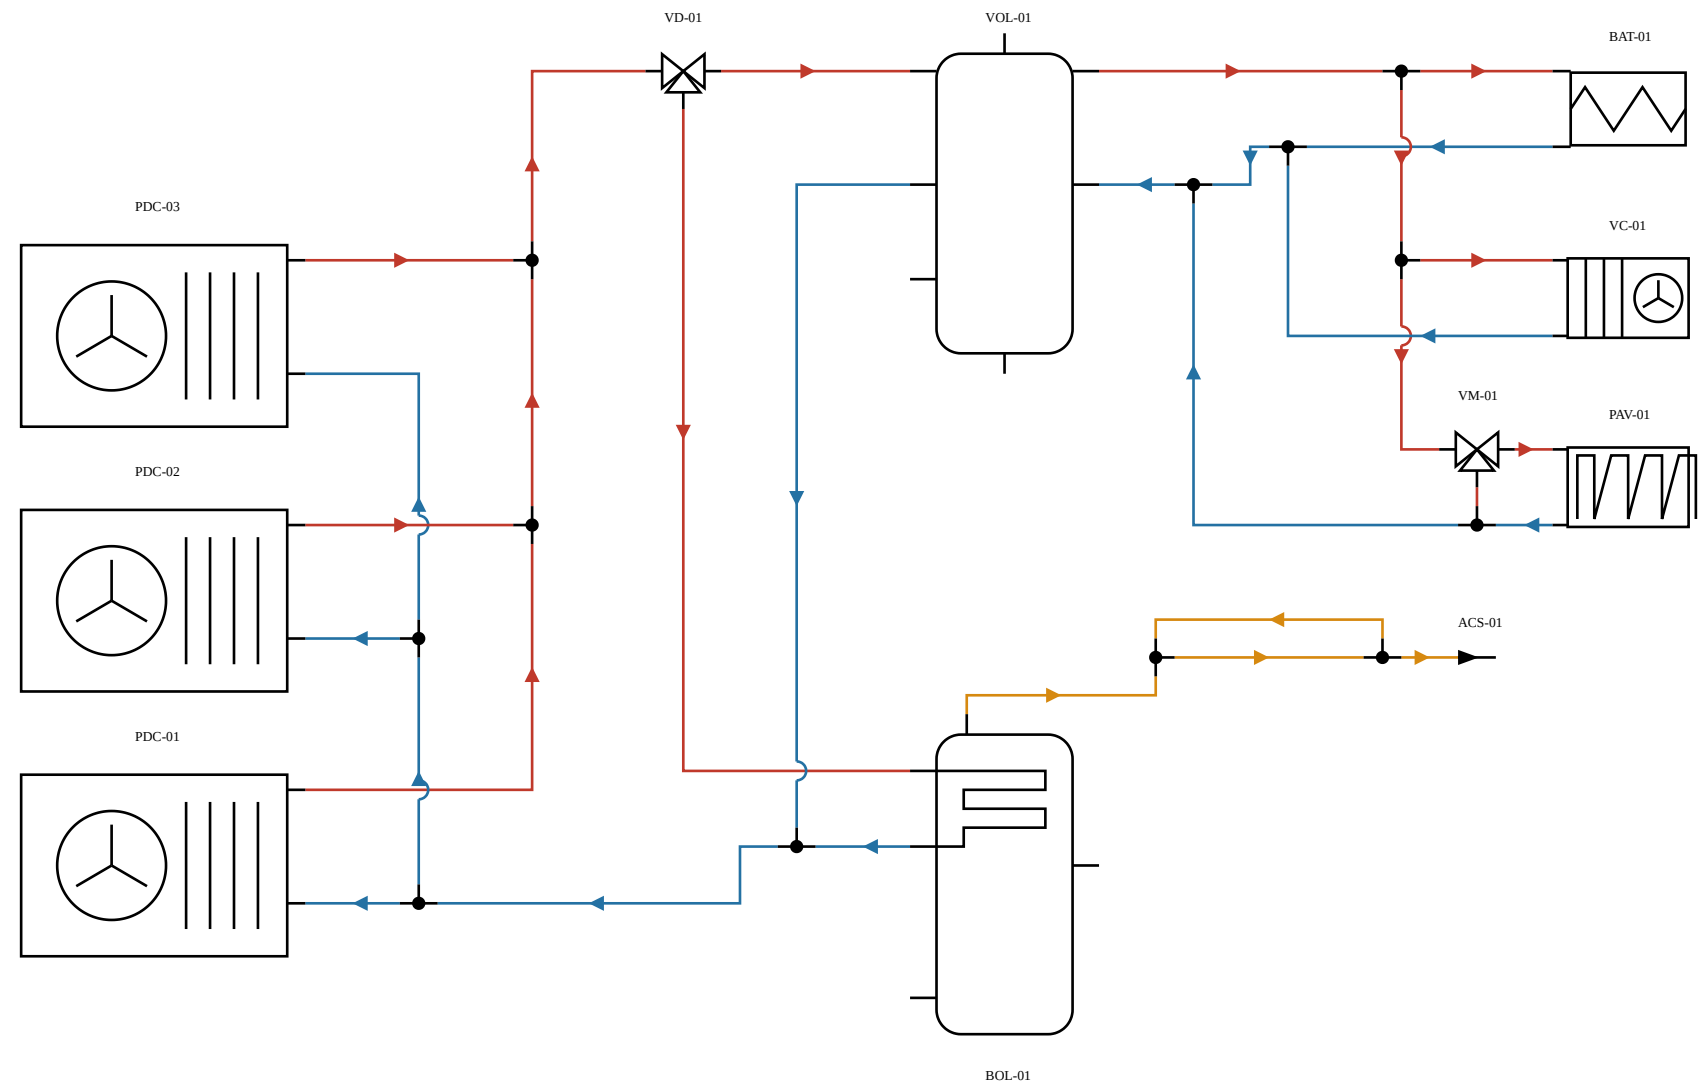

- Batteria di trattamento aria
 - Volano termico a quattro attacchi
 - Bollitore ACS
 - Valvola deviatrice a tre vie
 - Ventilconvettore
 - Pompa di calore aria-acqua
 - Valvola miscelatrice a tre vie
 - Confine di rete
 - Raccordo a T
 - Pannello radiante
- Acqua fredda sanitaria — andata
- Acqua fredda sanitaria — ritorno
- Acqua calda sanitaria — andata
- Acqua calda sanitaria — ritorno
- Acqua di riscaldamento — andata
- Acqua di riscaldamento — ritorno