
BOZZA — cartiglio incompleto

CODICE	DESCRIZIONE	CARATTERISTICHE	MARCA	MODELLO
GT-01	Pompa di calore aria-acqua	12 kW	Shenling	ThermaX R290
VOL-01	Volano termico a quattro attacchi	100 l	–	–
BOL-01	Bollitore ACS	300 l	–	–
CIR-01	Pompa di circolazione nr 1	–	–	–
CIR-02	Pompa di circolazione nr 2	–	–	–
CIR-03	Pompa di ricircolo sanitario	–	–	–
VE-01	Vaso di espansione	–	–	–
VE-02	Vaso di espansione sanitario	–	–	–

NOTE

1. Isolamento delle tubazioni a celle chiuse, conduttività massima 0,040 W/mK: nel tratto interrato in guaina corrugata, spessore 30 mm; a muro esterno spessore pieno 40 mm con protezione anti-UV; in centrale spessori minimi dell'Allegato B del DPR 412/93.
2. Antigelo: la pompa di calore resta alimentata d'inverno; la sua protezione antigelo funziona solo con la corrente.
3. Valvole di sfogo aria automatiche in tutti i punti alti e rubinetti di scarico in tutti i punti bassi del circuito.
4. La valvola sotto il vaso d'espansione si blocca aperta (maniglia tolta o lucchetto).
5. Sonda del volano (T_BT) nel pozzetto a metà altezza.

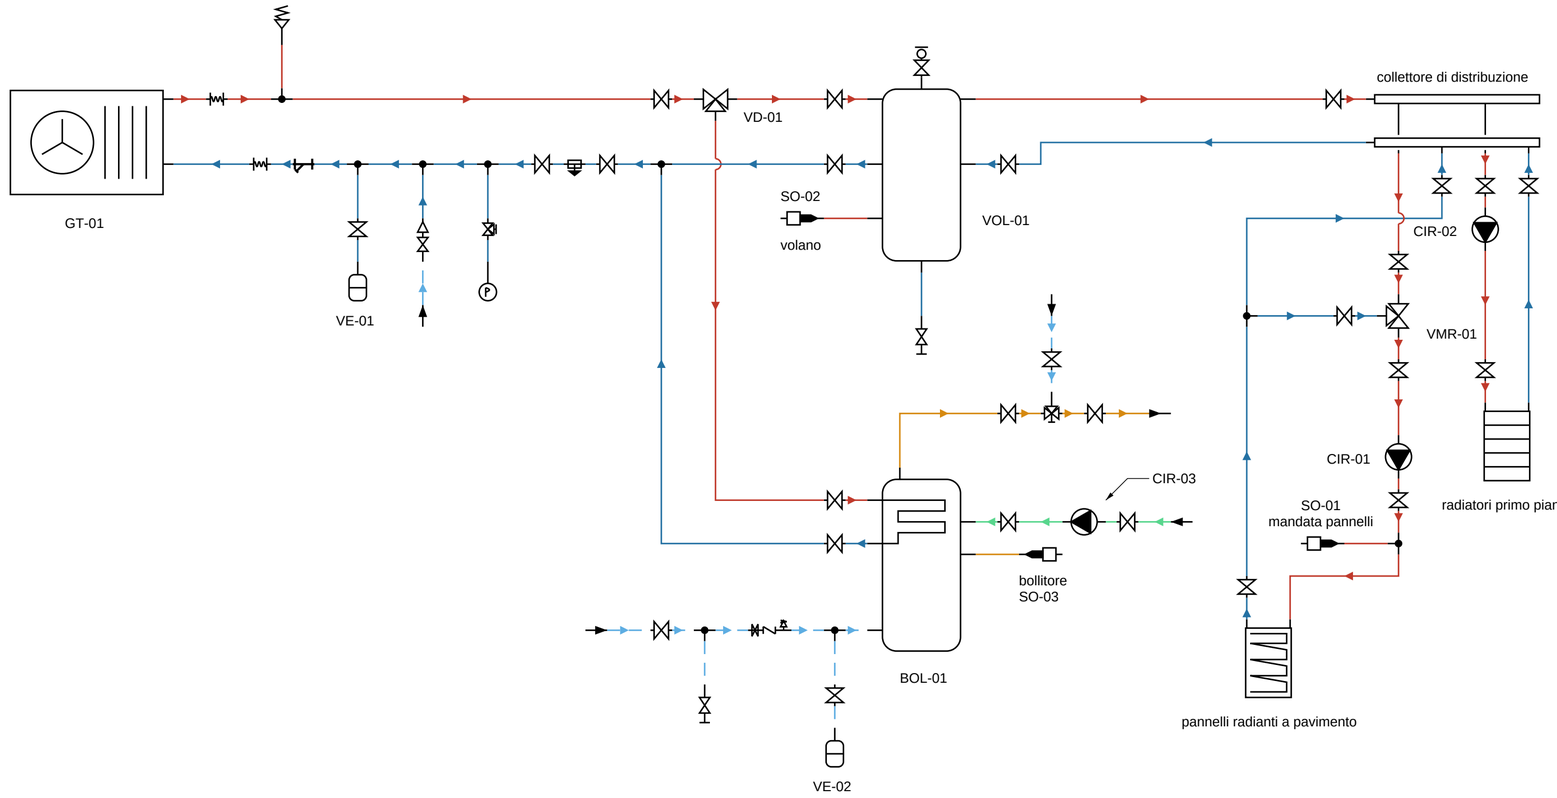

- Valvola di sfiato aria con rubinetto
- Volano termico a quattro attacchi
- Bollitore ACS
- Gruppo di sicurezza sanitario
- Defangatore
- Valvola deviatrice a tre vie
- Attacco di scarico
- Vaso di espansione
- Gruppo di riempimento con disconnettore
- Giunto antivibrante
- Pompa di calore aria-acqua
- Valvola miscelatrice a tre vie
- Valvola miscelatrice termostatica
- Confine di rete
- Manometro
- Pompa di circolazione
- Radiatore
- Filtro a Y
- Derivazione a T
- Raccordo a T
- Sonda di temperatura
- Pannello radiante
- Rubinetto portamanometro a tre vie
- Valvola di intercettazione
- Valvola di sicurezza
- Collettore di zona con ritorno

- Acqua fredda sanitaria — andata
- Acqua calda sanitaria — andata
- Acqua calda sanitaria — ricircolo
- Acqua di riscaldamento — andata
- Acqua di riscaldamento — ritorno

Vedi la tavola «elettrico e comando», dallo stesso schema

novec
VALORIZZAZIONE. EFFICIENTAMENTO. RIQUALIFICAZIONE.

COMMITTENTE: DA DEFINIRE	PROGETTO: Centrale termica villetta con pompa di calore aria-acqua	SCALA: —	DATA: 04.11.2026	APPROVATO
INDIRIZZO: DA DEFINIRE	TITOLO TAVOLA: DA DEFINIRE	REVISIONE: Rev. 00	COMMESSA: DA DEFINIRE	VERIFICATO
				DISEGNATO

TAVOLA

DA DEFINIRE