
BOZZA — cartiglio incompleto

CODICE	DESCRIZIONE	CARATTERISTICHE	MARCA	MODELLO
GT-01	Pompa di calore aria-acqua	12 kW	Shenling	ThermaX R290 12 kW
VOL-01	Volano termico a quattro attacchi	50 l	–	–
BOL-01	Bollitore ACS	200 l	–	–
CIR-01	Pompa di circolazione	–	–	–
VE-01	Vaso di espansione	–	–	–
VE-02	Vaso di espansione sanitario	12 l · precarica 3,0 bar	–	–

NOTE

1. Isolamento delle tubazioni a celle chiuse, conduttività massima 0,040 W/mK, con gli spessori minimi dell'Allegato B del DPR 412/93 sul diametro esterno (MS 26×3: 30 mm; MS 32×3: 30 mm; le altre: 30 mm da 20 a 39 mm, 40 mm da 40 a 59 mm); all'esterno spessore pieno e protezione anti-UV.
2. Antigelo: la pompa di calore resta alimentata d'inverno; la sua protezione antigelo funziona solo con la corrente.
3. Valvole di sfogo aria automatiche in tutti i punti alti e rubinetti di scarico in tutti i punti bassi del circuito.
4. La valvola sotto il vaso d'espansione si blocca aperta (maniglia tolta o lucchetto).
5. Sonda del volano (T_BT) nel pozzetto a metà altezza.

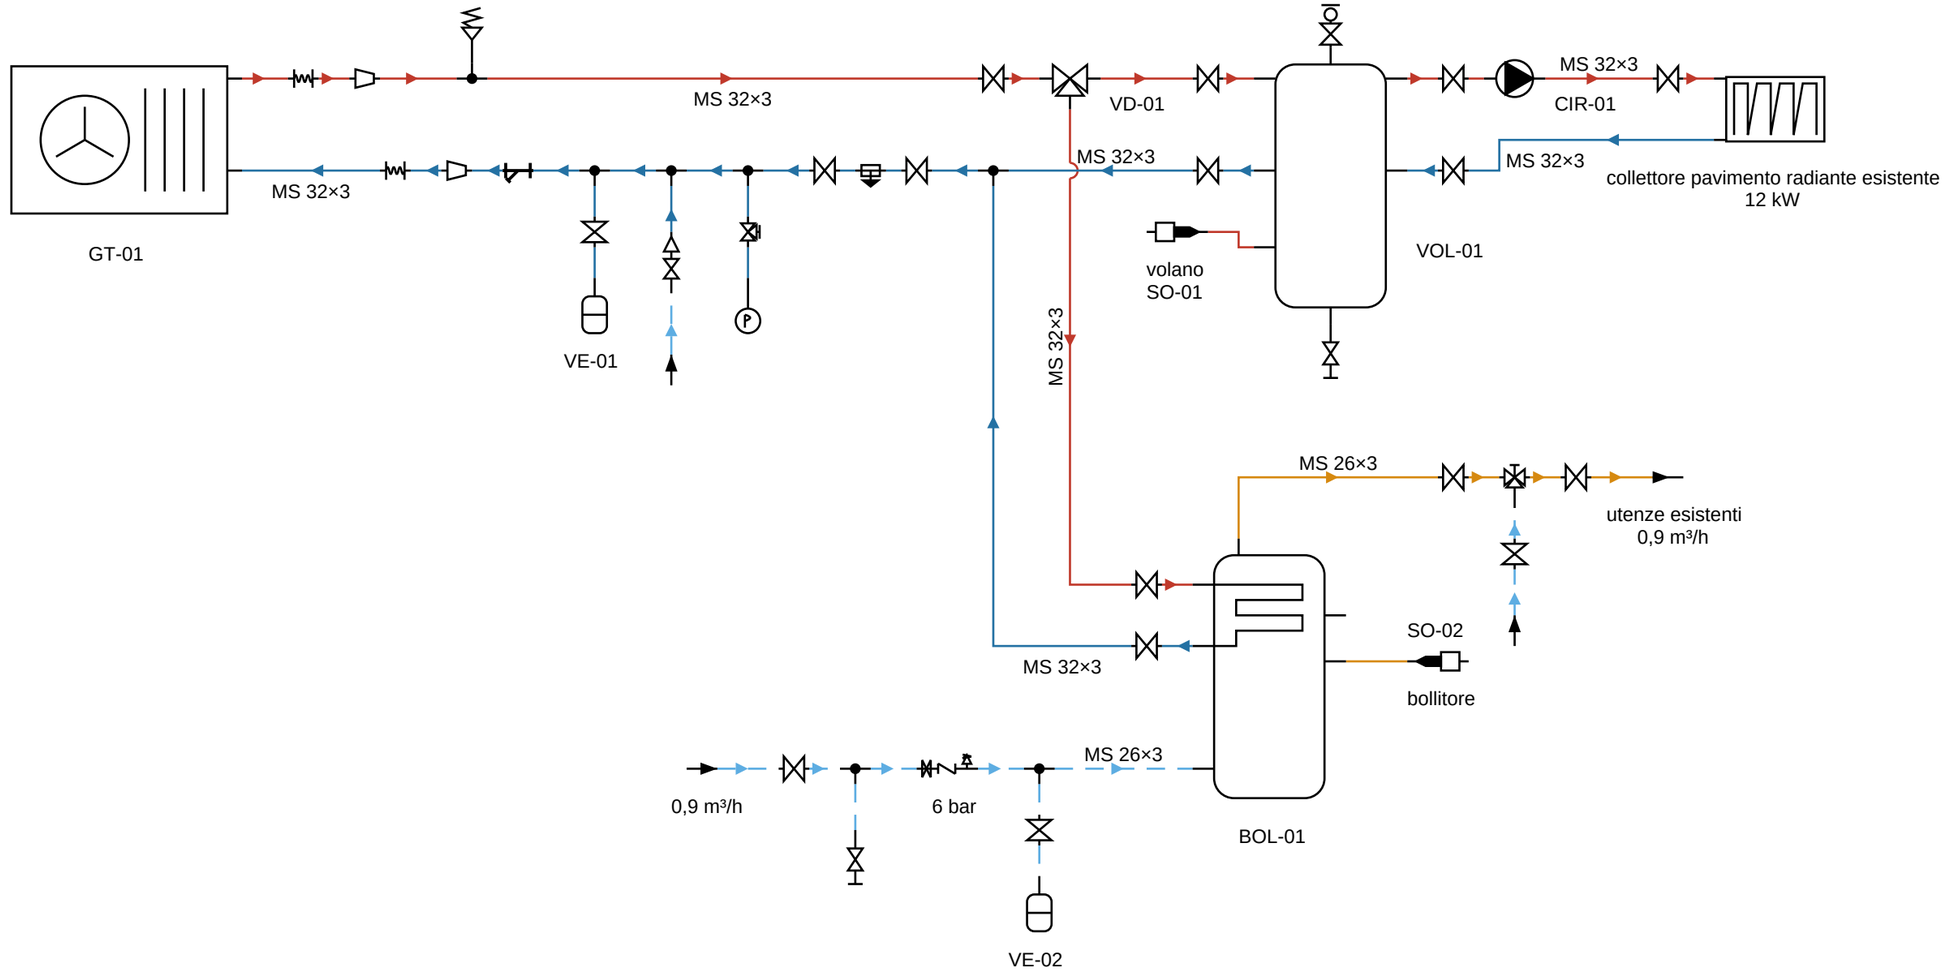

- Valvola di sfiato aria con rubinetto
- Volano termico a quattro attacchi
- Bollitore ACS
- Gruppo di sicurezza sanitario
- Defangatore
- Valvola deviatrice a tre vie
- Attacco di scarico
- Vaso di espansione
- Gruppo di riempimento con disconnettore
- Giunto antivibrante
- Pompa di calore aria-acqua
- Valvola miscelatrice termostatica
- Confine di rete
- Riduzione
- Manometro
- Pompa di circolazione
- Filtro a Y
- Derivazione a T
- Raccordo a T
- Sonda di temperatura
- Pannello radiante
- Rubinetto portamanometro a tre vie
- Valvola di intercettazione
- Valvola di sicurezza

- Acqua fredda sanitaria — andata
- Acqua calda sanitaria — andata
- Acqua di riscaldamento — andata
- Acqua di riscaldamento — ritorno
- MS multistrato, diametro esterno × spessore

VALORIZZAZIONE. EFFICIENTAMENTO. RIQUALIFICAZIONE.

COMMITTENTE: DA DEFINIRE	PROGETTO: Villetta: sostituzione caldaia con pompa di calore, volano e bollitore ACS	SCALA: —	DATA: 05.11.2026	APPROVATO
INDIRIZZO: DA DEFINIRE	TITOLO TAVOLA: DA DEFINIRE	REVISIONE: Rev. 00	COMMESSA: DA DEFINIRE	VERIFICATO
				DISEGNATO

TAVOLA: DA DEFINIRE