


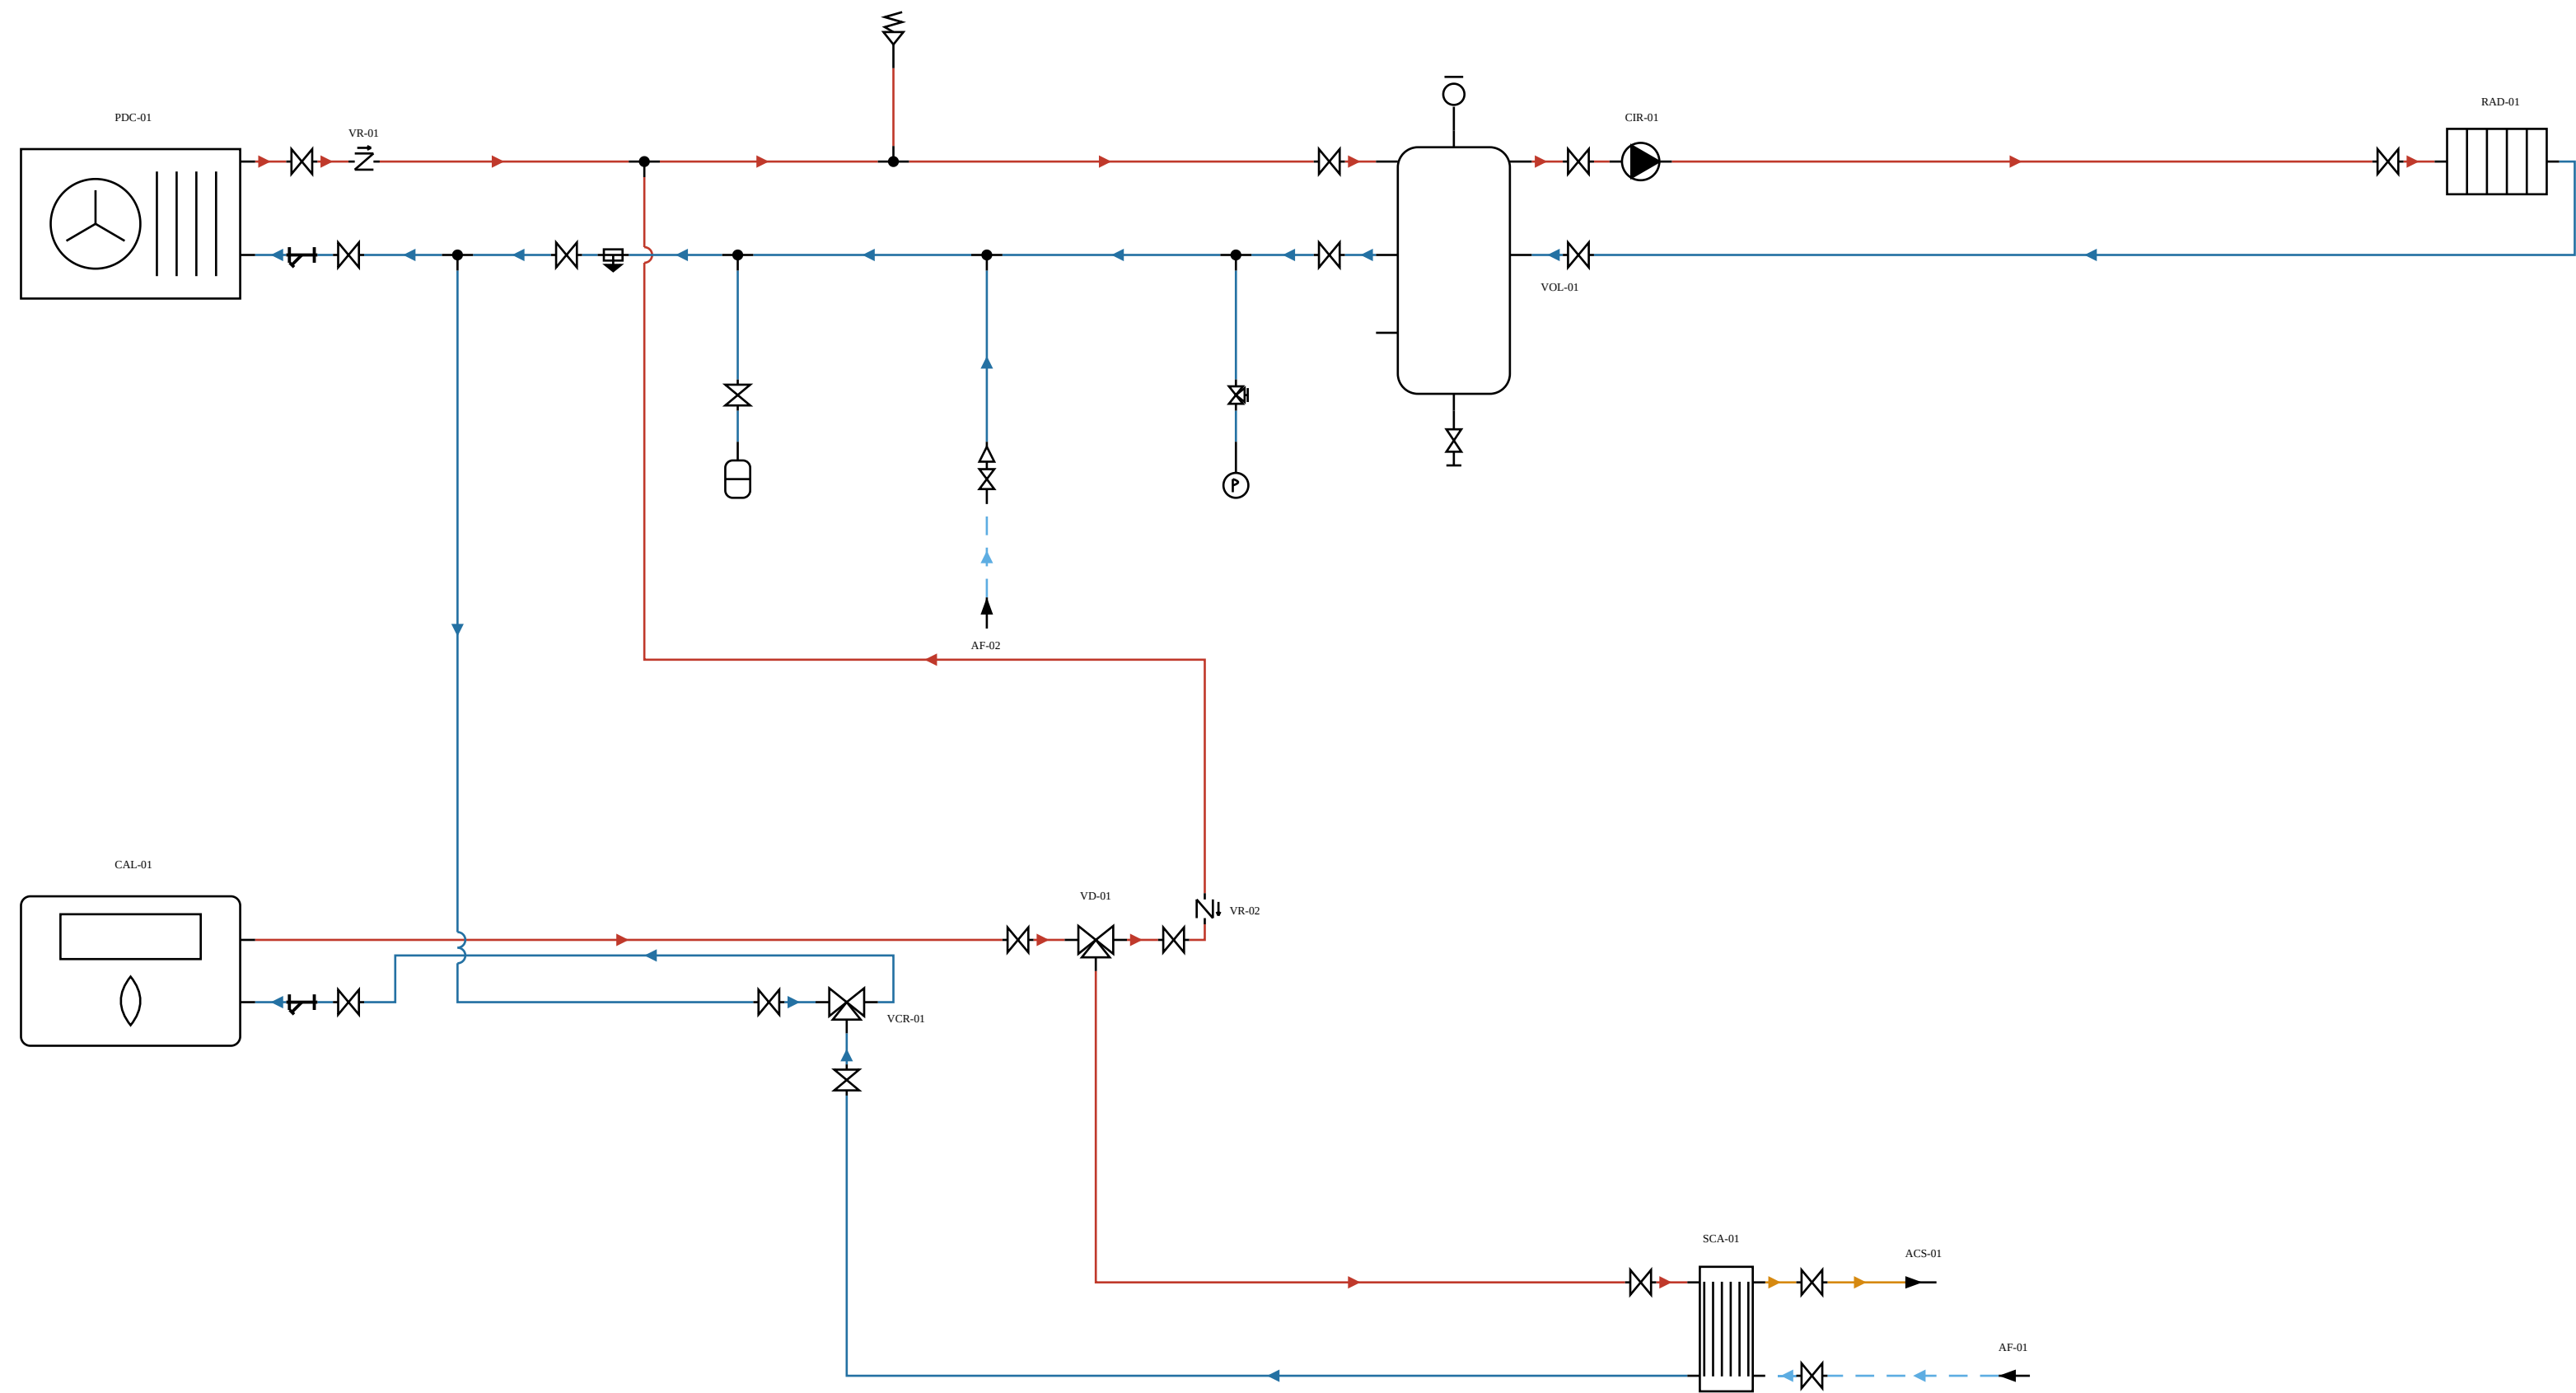

- Valvola di sfogo aria
 - Valvano termico a quattro attacchi
 - Defangatore
 - Valvola deviatrice a tre vie
 - Attacco di scarico
 - Vaso di espansione
 - Gruppo di riempimento
 - Caldaia a condensazione
 - Pompa di calore aria-acqua
 - Confine di rete
 - Scambiatore a piastre
 - Manometro
 - Pompa di circolazione
 - Radiatore
 - Filtro a Y
 - Valvola commutatrice a tre vie
 - Derivazione a T
 - Raccordo a T
 - Valvola di riseggo
 - Rubinetto portamanometro a tre vie
 - Valvola di intercettazione
 - Valvola di sicurezza
- Acqua fredda sanitaria — andata
- Acqua fredda sanitaria — ritorno
- Acqua calda sanitaria — andata
- Acqua calda sanitaria — ritorno
- Acqua di riscaldamento — andata
- Acqua di riscaldamento — ritorno