
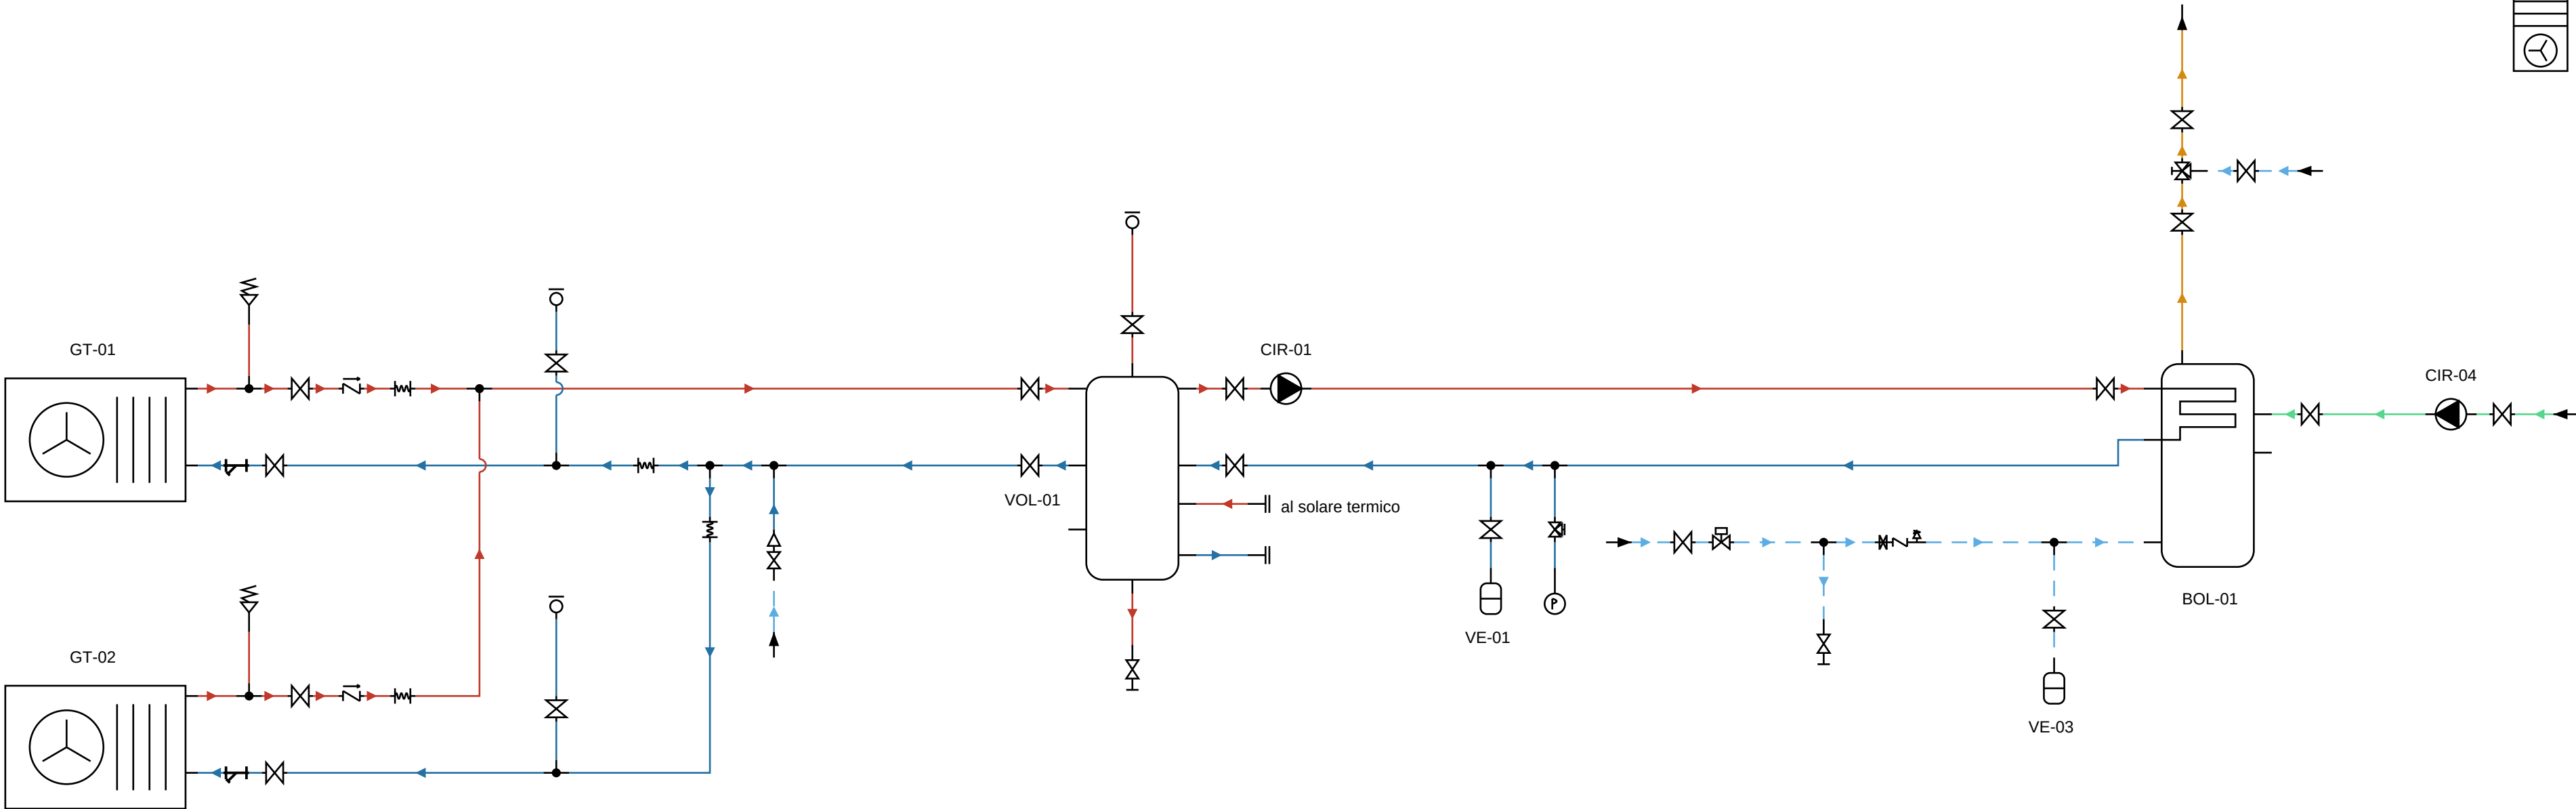


NOVE C INGEGNERIA Documenti confidenziali DA DEFINIRE - Elaborati Grafici				
CODICE	DESCRIZIONE	CARATTERISTICHE	MARCA	MODELLO
GT-01	Pompa di calore aria-acqua nr 1	15 kW	Shenling	HPM-V150W/R3
GT-02	Pompa di calore aria-acqua nr 2	15 kW	Shenling	HPM-V150W/R3
GT-03	Pompa di calore aria-acqua nr 3	15 kW	Shenling	HPM-V150W/R3
GT-04	Pompa di calore aria-acqua nr 4	15 kW	Shenling	HPM-V150W/R3
GT-05	Pompa di calore aria-acqua nr 5	15 kW	Shenling	HPM-V150W/R3
GT-06	Pompa di calore aria-acqua nr 6	15 kW	Shenling	HPM-V150W/R3
VOL-01	Volano termico a sei attacchi	200 l	Cordivari	Volano BS GBF 200
VOL-02	Volano termico a quattro attacchi	1000 l	Cordivari	Volano BS GBL 1000
BOL-01	Bollitore ACS	1000 l	-	-
CIR-01	Pompa di circolazione nr 1	-	DAB	EVOSTA3 80/130
CIR-02	Pompa di circolazione nr 2	-	Grundfos	MAGNA (sigla da completare)
CIR-03	Pompa di circolazione nr 3	-	Grundfos	MAGNA (sigla da completare)
CIR-04	Pompa di ricircolo sanitario	-	-	-
VE-01	Vaso di espansione nr 1	-	-	-
VE-02	Vaso di espansione nr 2	-	-	-
VE-03	Vaso di espansione sanitario	-	-	-

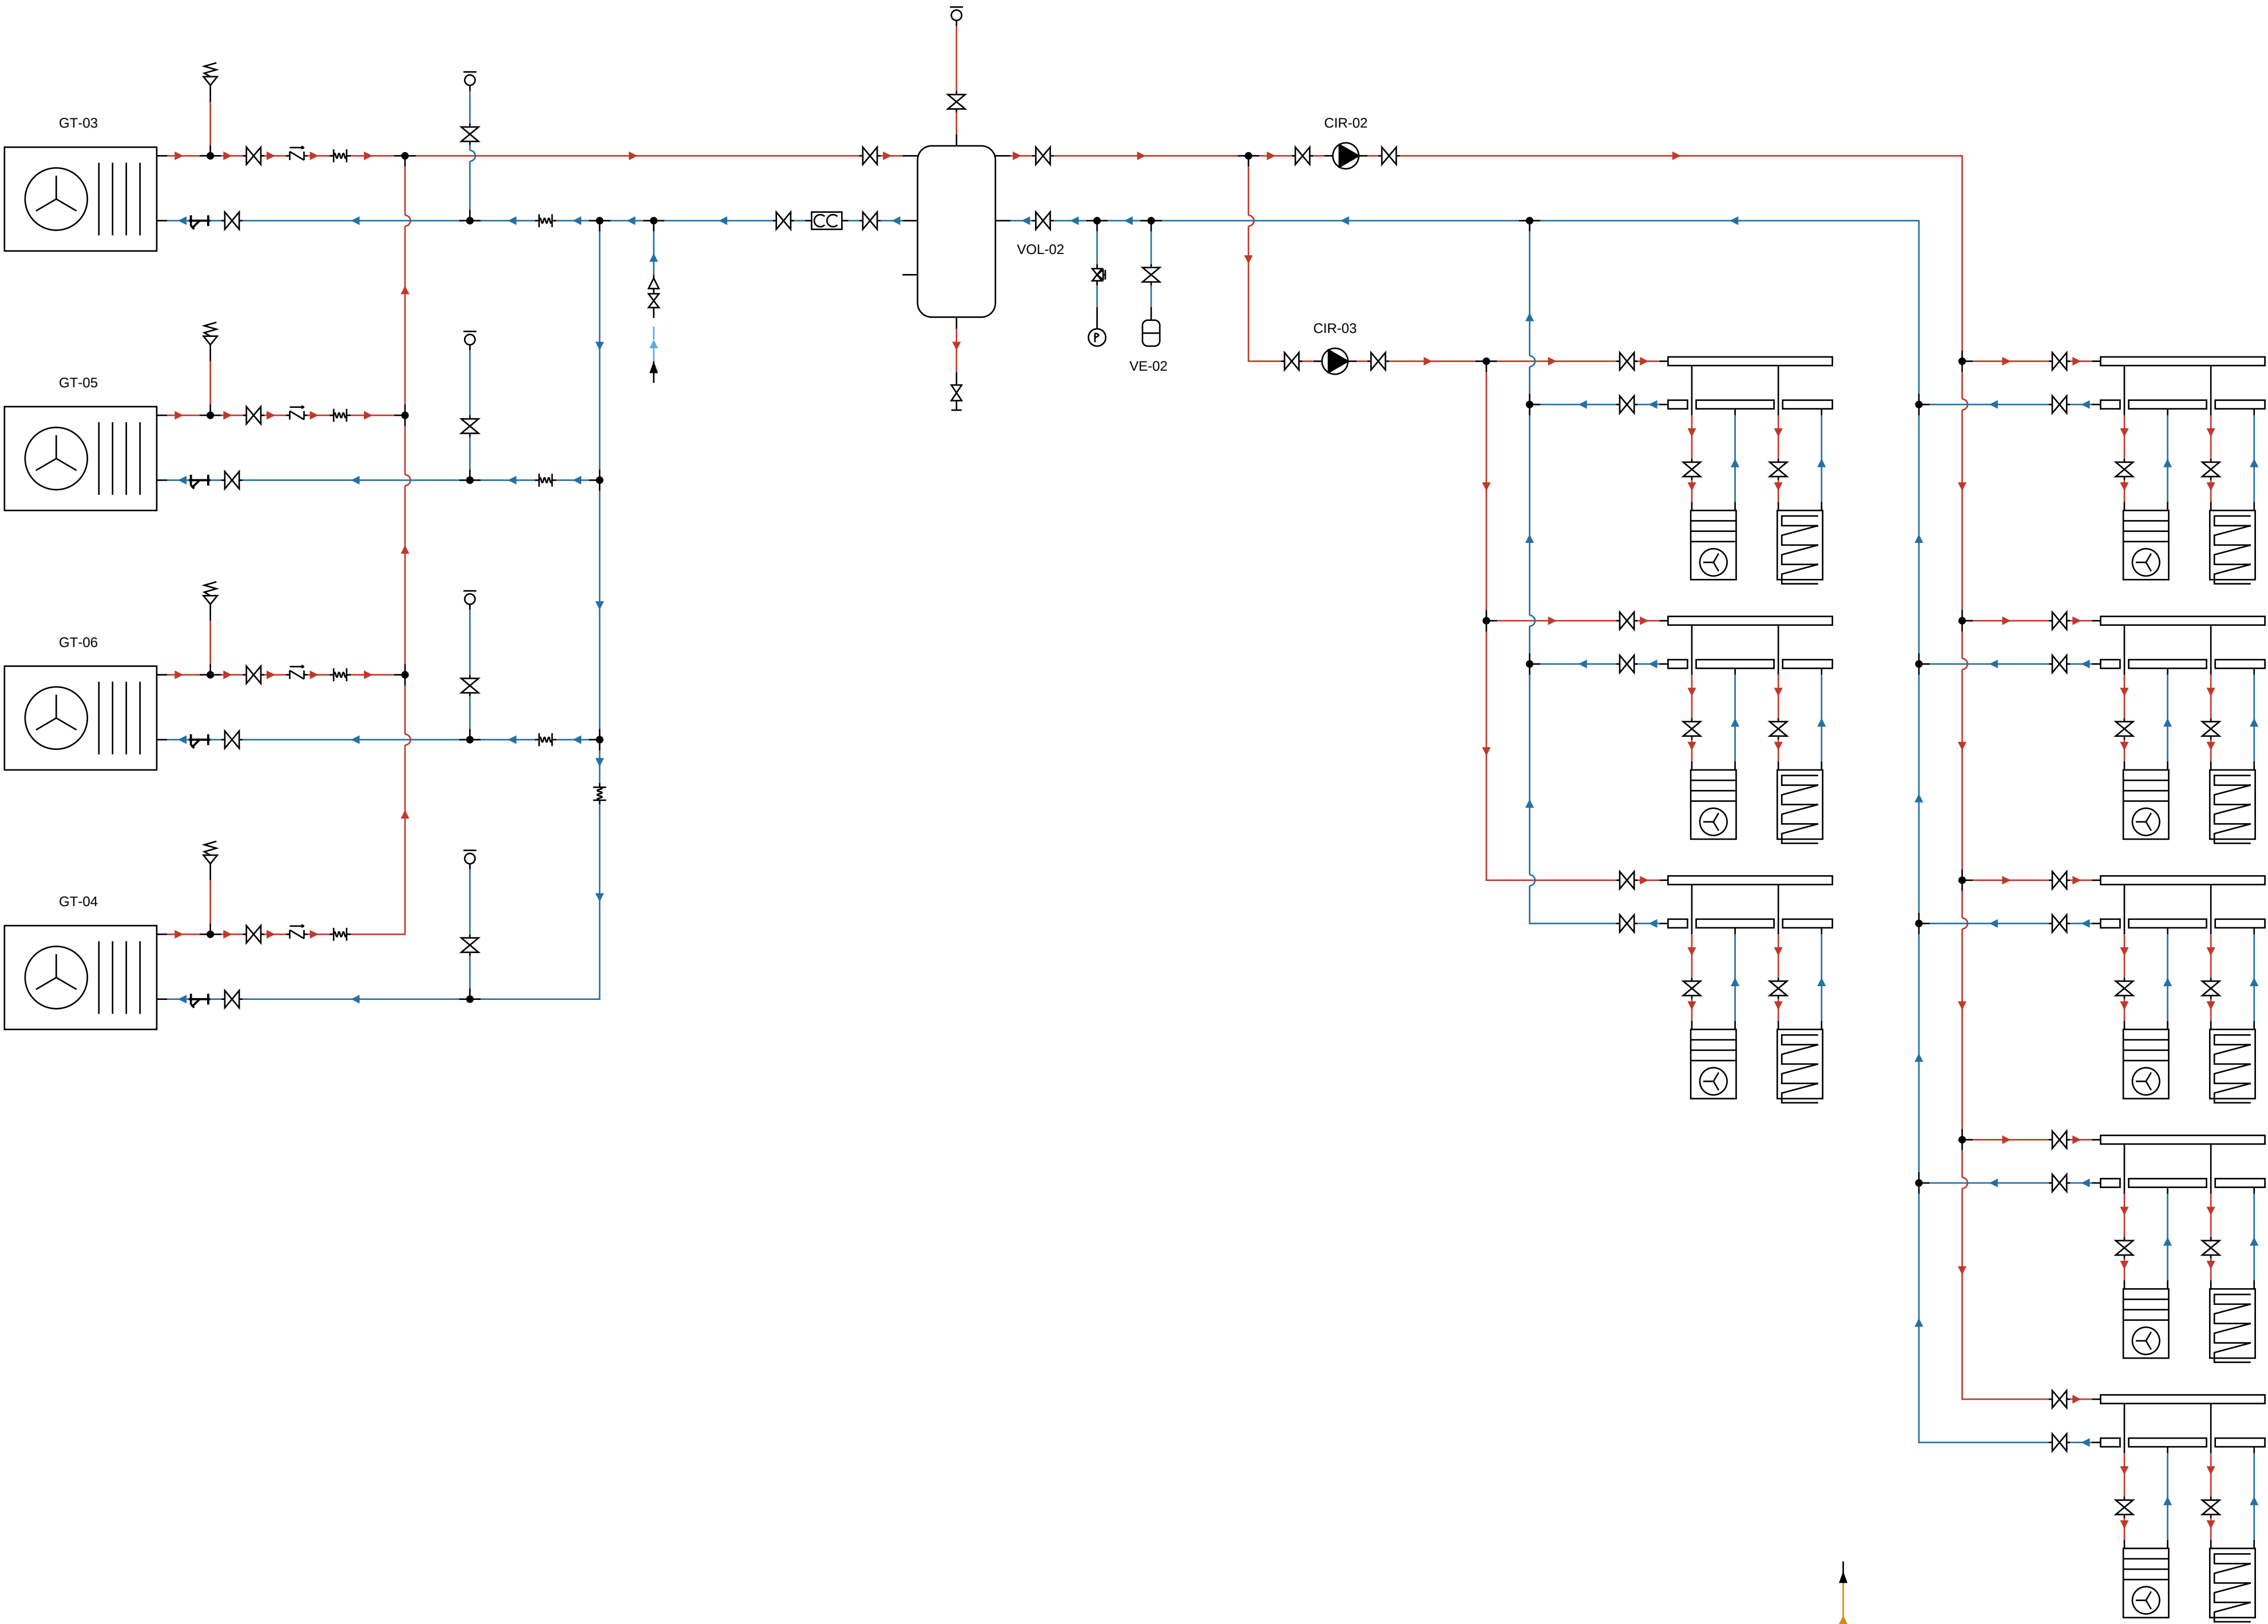

- BOZZA — cartiglio incompleto
- Valvola di sfidato aria
 - Volano termico a quattro attacchi
 - Volano termico a sei attacchi
 - Attacco predisposto
 - Bollitore ACS
 - Gruppo di sicurezza sanitario
 - Attacco di scarico
 - Vaso di espansione
 - Ventilconvettore
 - Gruppo di riempimento
 - Giunto antivibrante
 - Contatore di calore
 - Pompa di calore aria-acqua
 - Valvola miscelatrice termostatica
 - Confini di rete
 - Manometro
 - Riduttore di pressione
 - Pompa di circolazione
 - Filtro a Y
 - Derivazione a T
 - Raccordo a T
 - Pannello radiante
 - Valvola di ritegno
 - Rubinetto portamanometro a tre vie
 - Valvola di intercettazione
 - Valvola di sicurezza
 - Collettore di zona con ritorno
- Acqua fredda sanitaria — andata
— Acqua calda sanitaria — andata
— Acqua calda sanitaria — ricircolo
— Acqua di riscaldamento — andata
— Acqua di riscaldamento — ritorno

 VALORIZZAZIONE. EFFICIENTAMENTO. RIQUALIFICAZIONE.	COMMITTENTE Condominio (caso reale, anonimo)	PROGETTO Sostituzione generatori di calore - centrale termica centralizzata a pompe di calore	SCALA —	DATA 03.10.2026	APPROVATO _____	TAVOLA DA DEFINIRE
	INDIRIZZO DA DEFINIRE	TITOLO TAVOLA DA DEFINIRE	REVISIONE Rev. 00	COMMESSA DA DEFINIRE	VERIFICATO _____	
					DISEGNATO _____	