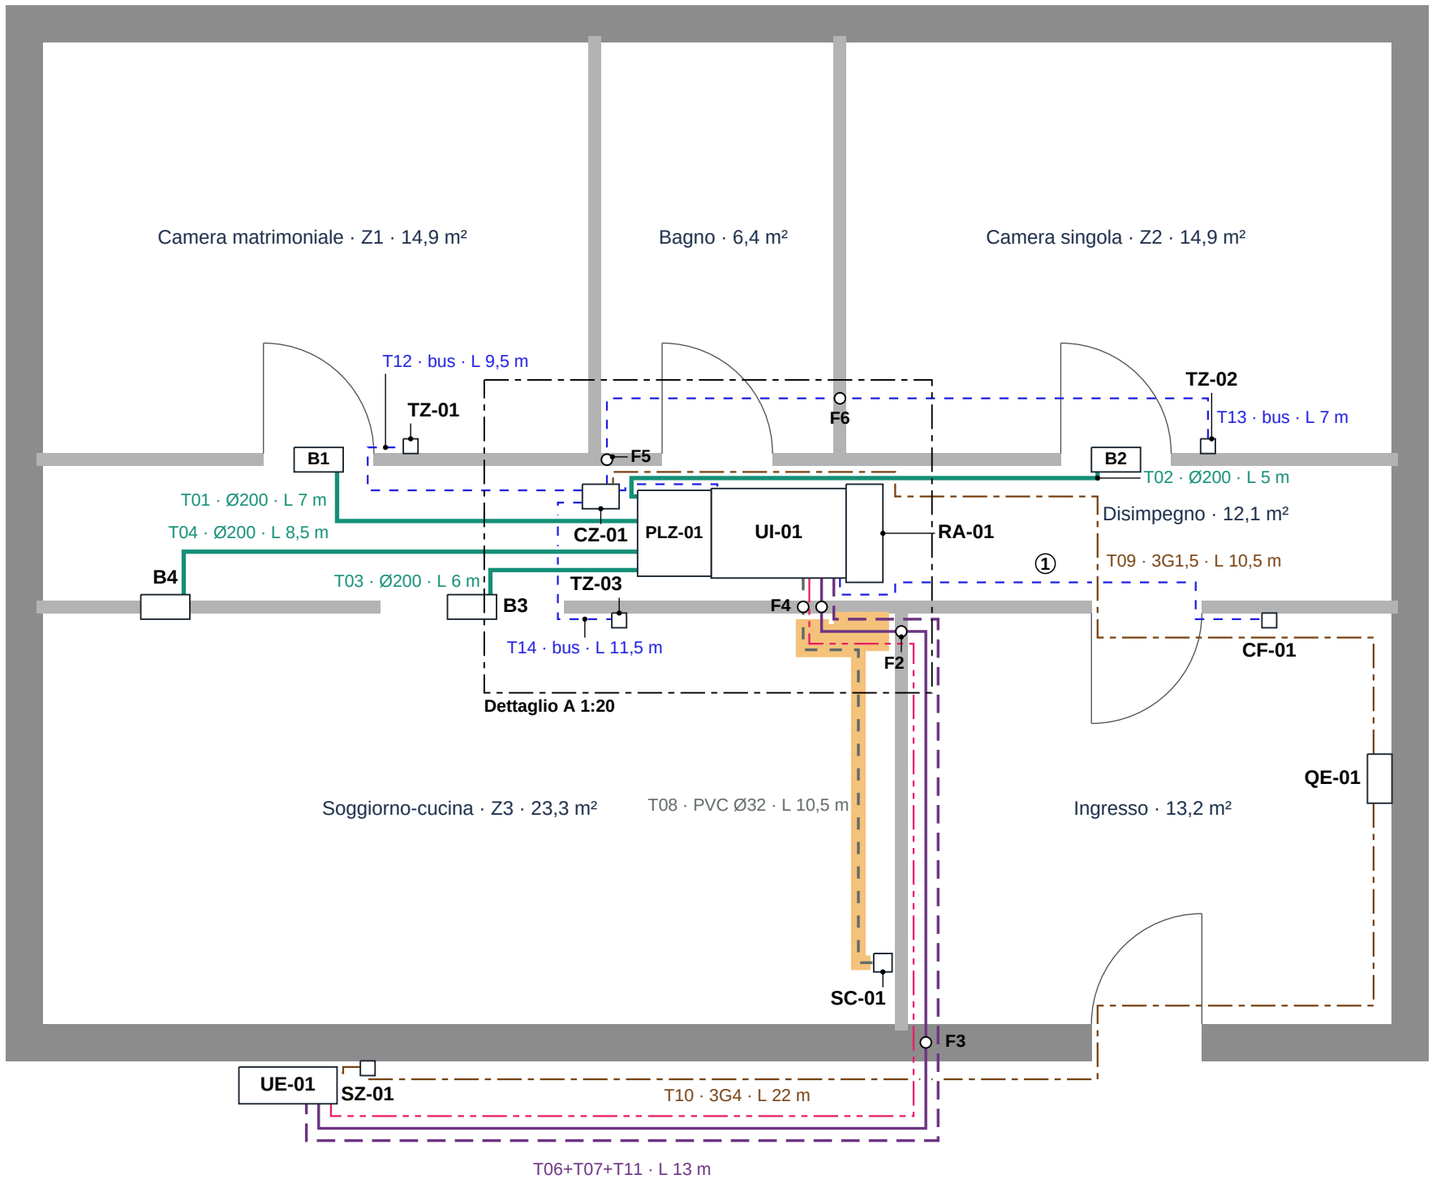


PIANTA DEI POSIZIONAMENTI E DEI TRACCIATI

Scala 1:50 su A3 · misure in metri

Percorsi indicativi, da verificare in sopralluogo.

LEGENDA

- Aria di mandata
- Refrigerante gas
- Refrigerante liquido
- Condensa
- Collegamento fra le unità
- Alimentazione elettrica
- Bus di comando
- Pezzo posato: ingombro e sigla
- Foratura (F1, F2…: elenco sotto)
- Fuori dal controsoffitto: da verificare
- ① Scritta in legenda (testo sotto)

TRATTE

Tratta	Fluido	Da	A	Dim.	L prog.	L mis.	L quot.
T01	Aria di mandata	PLZ-01	B1	Ø200	5	2,9	7
T02	Aria di mandata	PLZ-01	B2	Ø200	3	4!	5
T03	Aria di mandata	PLZ-01	B3	Ø200	4	1,4	6
T04	Aria di mandata	PLZ-01	B4	Ø200	6	4	8,5
T06	Frigo, liquido	UI-01	UE-01	1/4"	9	10,5!	12*
T07	Frigo, gas	UI-01	UE-01	5/8"	9	10,9!	12*
T08	Condensa	UI-01	SC-01	PVC Ø32	8	3,7	10,5
T09	Alimentazione	QE-01	CZ-01	3G1,5	8	8,6	10,5
T10	Alimentazione	QE-01	UE-01	3G4	18	10,7	22
T11	Cavo UI-UE	UI-01	UE-01	4G1,5	10	10,1	13
T12	Bus	CZ-01	TZ-01	bus	7	2,4	9,5
T13	Bus	CZ-01	TZ-02	bus	5	5,9!	7
T14	Bus	CZ-01	TZ-03	bus	9	1,6	11,5
T15	Bus	UI-01	CF-01	2×0,75	6	4	8,5
T16	Bus	CZ-01	UI-01	DA DEFINIRE	—	0,9	5*°

Passano per organi in linea: T10 per SZ-01. L prog. del progettista, si quota; L mis. sul disegno, un controllo (! oltre il 15 %); L quot. = (L + 1 m) × 1,15 per eccesso a 0,5 m, regola della distinta; * minimo (frigo 12 m, condensa 10 m, bus 5 m, ramo aria 2 m, il cavo fra le unita' segue le linee frigo + 1 m); ° sulla misura, L prog. manca.

AVVISI

– Misura oltre il 15 % di L prog.: T02 4 m su 3 (+35 %); T06 10,5 m su 9 (+16 %); T07 10,9 m su 9 (+21 %); T13 5,9 m su 5 (+19 %). Da verificare il percorso o il dato.
– Senza L prog., quotate sulla misura (°): T16. Da riportare nel grafo, o da chiedere.
– Fuori dal controsoffitto (fascia arancio): T06-T07-T11 0,85 m; T08 3,35 m. Canalina o traccia, da verificare.
– Dettagli A 1:20 (zone incorniciate): tavole collaudo-t1-dettaglio-<lettera>, perche' a 1:50 le scritte non ci stanno.

FORATURE

F1 · T06 T07 T11 · tramezza t-corr-sud · controsoffitto
F2 · T06 T07 T11 · tramezza t-sogg-ingresso · controsoffitto
F3 · T06 T07 T11 · perimetrale m-sud · controsoffitto
F4 · T08 · tramezza t-corr-sud · controsoffitto
F5 · T13 · tramezza t-corr-nord · traccia
F6 · T13 · tramezza t-bagno-singola · traccia
Fori per i pezzi a parete: B1, B2 nel muro t-corr-nord; B3, B4 nel muro t-corr-sud.

SCRITTE IN LEGENDA

① T15 · 2×0,75 · L 8,5 m

NOTE

1. Quote: canali, linee frigo e condensa in controsoffitto; cavi e bus in traccia, salvo dove la tabella dice altro. Salite e discese stanno nell'aggiunta della regola.
2. Sigle e numeri di tratta come lo schema funzionale e la distinta.
3. Caso del collaudo indipendente REL-012 (t1): planimetria inventata, data a parole dal progettista del collaudo; non e' quella di nessun committente.
4. Misure interne 11 x 8 m, origine spostata di 0,30 m per il muro perimetrale.
5. Posizioni di centrale di zona, termostati, comando a filo, sezionatore e scarico della cucina assunte: da confermare.