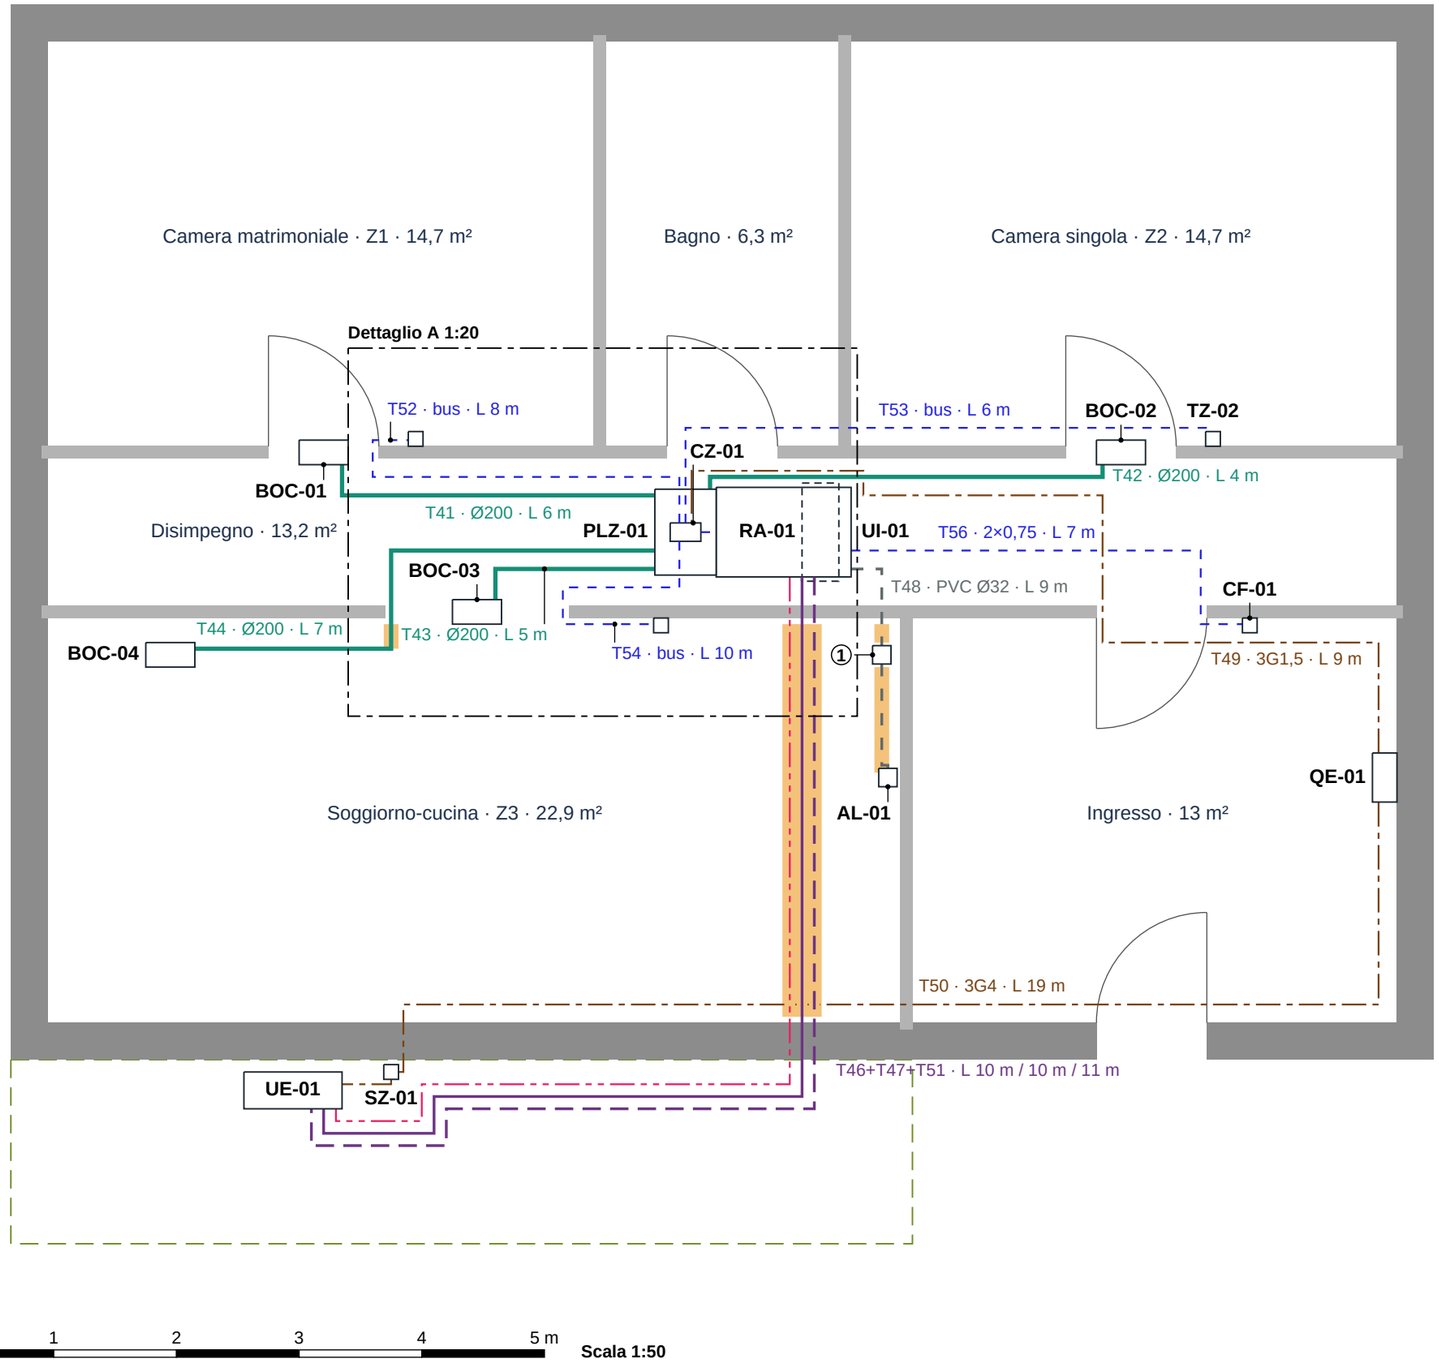


PIANTA DEI POSIZIONAMENTI E DEI TRACCIATI

Scala 1:50 su A3 · misure in metri

Percorsi indicativi, da verificare in sopralluogo.

LEGENDA

- Aria di mandata
- Refrigerante gas
- Refrigerante liquido
- Condensa
- Collegamento fra le unità
- Alimentazione elettrica
- Bus di comando
- Pezzo posato: ingombro e sigla
- Pezzo sotto un altro (altra quota)
- Zona esterna praticabile
- Fuori dal controsoffitto: da verificare
- ① Scritta in legenda (testo sotto)

TRATTE

Tratta	Fluido	Da	A	Dim.	L prog.	L mis.	L quot.
T41	Aria di mandata	PLZ-01	BOC-01	Ø200	6	2,8	8,5
T42	Aria di mandata	PLZ-01	BOC-02	Ø200	4	3,4	6
T43	Aria di mandata	PLZ-01	BOC-03	Ø200	5	1,6	7
T44	Aria di mandata	PLZ-01	BOC-04	Ø200	7	4,5	9,5
T46	Frigo, liquido	UI-01	UE-01	1/4"	10	8,6	13
T47	Frigo, gas	UI-01	UE-01	5/8"	10	9	13
T48	Condensa	UI-01	AL-01	PVC Ø32	9	1,8	11,5
T49	Alimentazione	QE-01	CZ-01	3G1,5	9	8,3	11,5
T50	Alimentazione	QE-01	UE-01	3G4	19	10,6	23
T51	Cavo UI-UE	UI-01	UE-01	4G1,5	11	8,2	14
T52	Bus	CZ-01	TZ-01	bus	8	3,5	10,5
T53	Bus	CZ-01	TZ-02	bus	6	5,1	8,5
T54	Bus	CZ-01	TZ-03	bus	10	2,4	13
T55	Bus	CZ-01	UI-01	2×0,75	3	0,1	5
T56	Bus	UI-01	CF-01	2×0,75	7	3,8	9,5

Passano per organi in linea: T48 per SIF-01; T50 per SZ-01. L prog. del progettista, si quota; L mis. sul disegno, un controllo (! oltre il 15 %); L quot. = (L + 1 m) × 1,15 per eccesso a 0,5 m, regola della distinta; * minimo (frigo 12 m, condensa 10 m, bus 5 m, ramo aria 2 m, il cavo fra le unita' segue le linee frigo + 1 m); ° sulla misura, L prog. manca.

AVVISI

– Fuori dal controsoffitto (fascia arancio): T44 0,2 m; T46-T47-T51 3,2 m; T48 1 m. Canalina o traccia, da verificare.
– Confronto con la distinta e il grafo: 49 discordanze (15 tratte della pianta che la distinta non ha; 15 tratte della distinta non in pianta; 4 sigle diverse dallo schema; 15 lunghezze diverse dal grafo). L'elenco per esteso e' in discordanze.tracciati.json («confronto») e in console.
– Dettagli A 1:20 (zone incorniciate): tavole discordanze-dettaglio-<lettera>, perche' a 1:50 le scritte non ci stanno.

SCRITTE IN LEGENDA

① SIF-01

NOTE

1. Quote: canali, linee frigo e condensa in controsoffitto; cavi e bus in traccia, salvo dove la tabella dice altro. Salite e discese stanno nell'aggiunta della regola.
2. Sigle e numeri di tratta come lo schema funzionale e la distinta. Controllati con la distinta e il grafo: ci sono discordanze (vedi gli avvisi).
3. Ingombri da confermare (valori dichiarati, non del progettista ne' della scheda): UI-01, PLZ-01, CZ-01, RA-01.
4. Sovrapposti, a quote diverse: CZ-01 sopra PLZ-01; RA-01 sotto UI-01.
5. Planimetria a parole del progettista: 11 × 8 m misure interne, muri perimetrali 30 cm fuori dal rettangolo interno, tramezze 10 cm.
6. Le tramezze del corridoio hanno le facce a y=3,4 e y=4,6 (corridoio libero 1,2 m): assi a 3,35 e 4,65.
7. Il terrazzo sta solo a sud del soggiorno (dal testo): la profondità di 1,5 m è assunta, da confermare. Fuori dal terrazzo le linee non passano.
8. Da confermare: posizione dei termostati e del comando a filo; posizione del sezionatore e dell'allaccio allo scarico della cucina; il lato della UI sotto cui sta la ripresa.
9. T05 (ripresa) è un raccordo diretto sotto la UI: non ha tracciato.

novec — VALORIZZAZIONE. EFFICIENTAMENTO. RIQUALIFICAZIONE.	COMMITTENTE: DA DEFINIRE	PROGETTO: Canalizzato aria-aria in pompa di calore - appartamento al secondo piano	SCALA: 1:50	DATA: 29.10.2026	APPROVATO / VERIFICATO / DISEGNATO
	INDIRIZZO: DA DEFINIRE	TITOLO TAVOLA: Pianta dei posizionamenti e dei tracciati	REVISIONE: Rev. 00	COMMESSA: DA DEFINIRE	TAVOLA: DA DEFINIRE