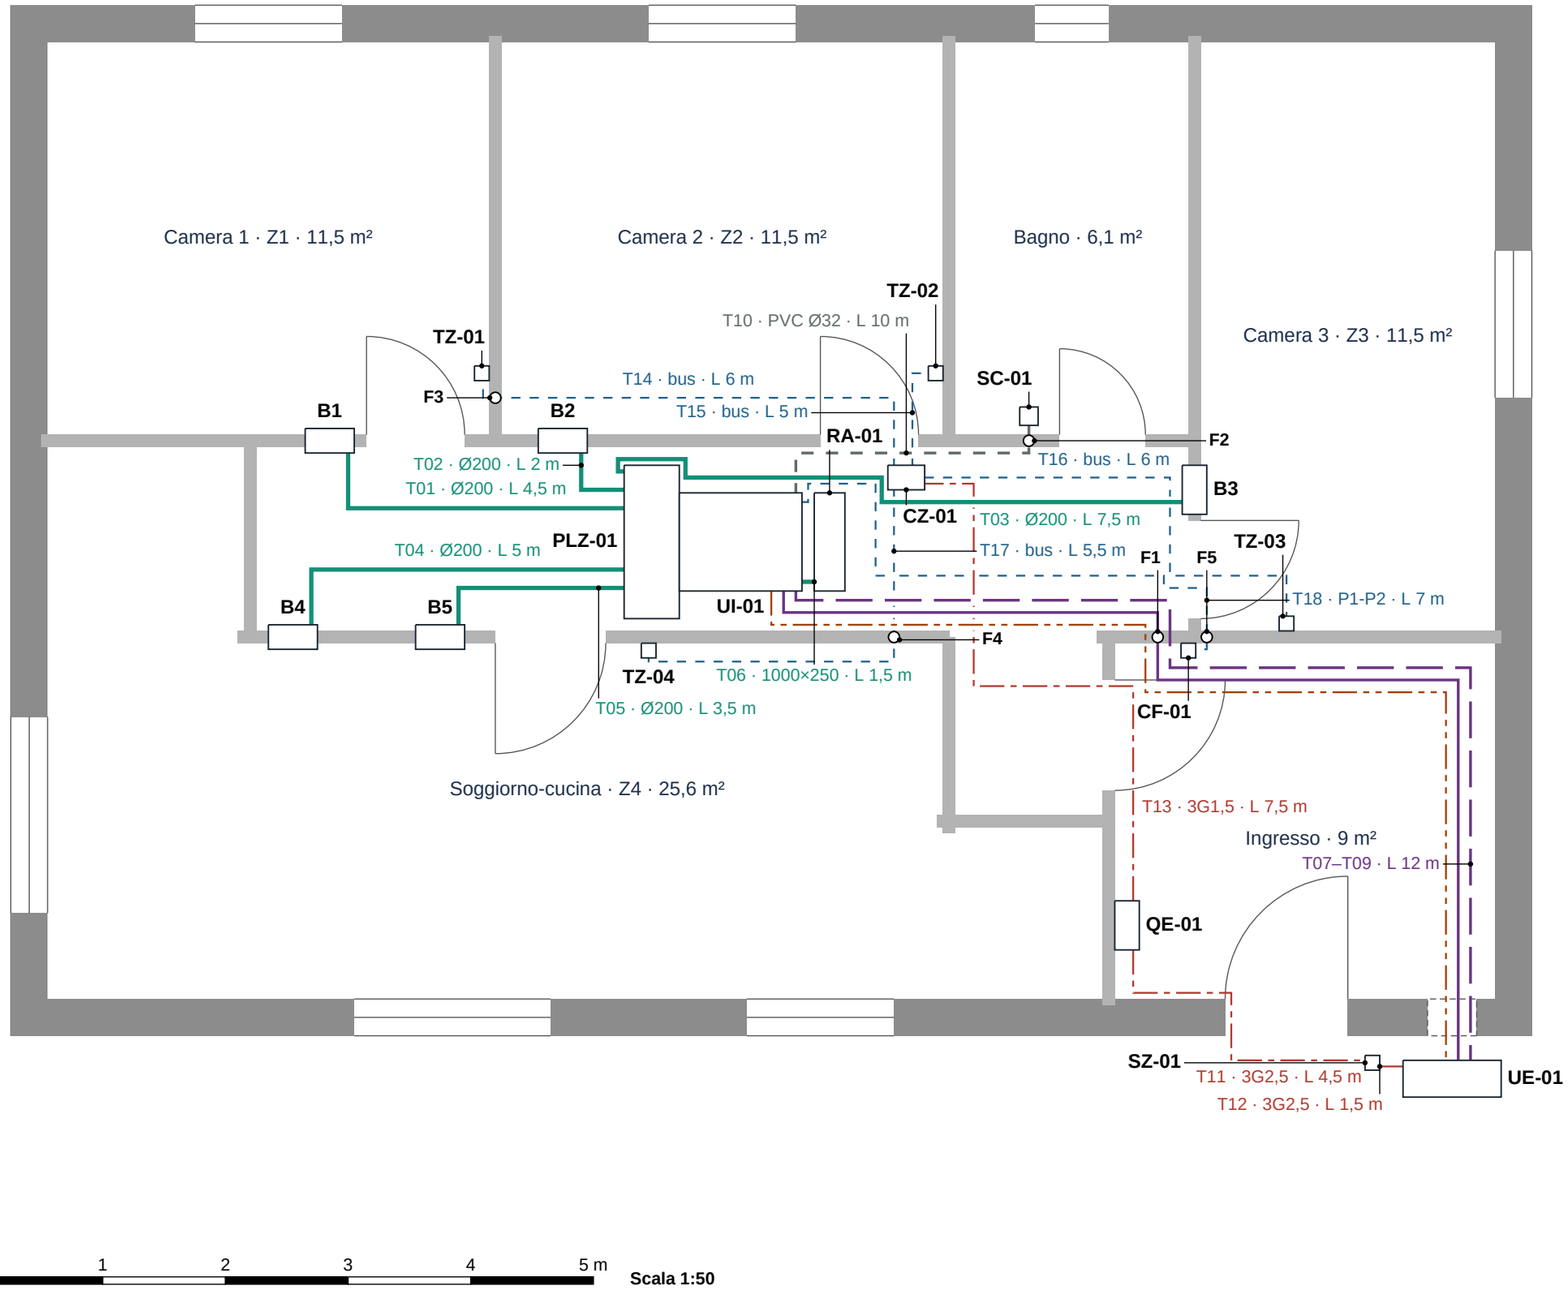


0 1 2 3 4 5 m

Scala 1:50

PIANTA DEI POSIZIONAMENTI E DEI TRACCIATI

Scala 1:50 su A3 · misure in metri

Percorsi indicativi, da verificare in sopralluogo.

LEGENDA

- Aria di ripresa
- Aria di mandata
- Refrigerante gas
- Refrigerante liquido
- Condensa
- Collegamento elettrico fra le unità
- Alimentazione elettrica
- Bus di comando
- Pezzo posato: ingombro in pianta e sigla
- Foratura da eseguire (F1, F2…: elenco sotto)

TRATTE

Tratta	Fluido	Da	A	Dim.	L mis.	L quot.
T01	Aria di mandata	PLZ-01	B1	Ø200	2,7	4,5
T02	Aria di mandata	PLZ-01	B2	Ø200	0,7	2
T03	Aria di mandata	PLZ-01	B3	Ø200	5,1	7,5
T04	Aria di mandata	PLZ-01	B4	Ø200	3	5
T05	Aria di mandata	PLZ-01	B5	Ø200	1,6	3,5
T06	Aria di ripresa	RA-01	UI-01	1000×250	0,1	1,5
T07	Frigo, liquido	UI-01	UE-01	6,35	9,3	12
T08	Frigo, gas	UI-01	UE-01	12,7	9,3	12
T09	Cavo UI-UE	UI-01	UE-01	4G1,5	9,3	12
T10	Condensa	UI-01	SC-01	PVC Ø32	2,5	10*
T11	Alimentazione	QE-01	SZ-01	3G2,5	2,8	4,5
T12	Alimentazione	SZ-01	UE-01	3G2,5	0,2	1,5
T13	Alimentazione	QE-01	CZ-01	3G1,5	5,1	7,5
T14	Bus	CZ-01	TZ-01	bus	4	6
T15	Bus	CZ-01	TZ-02	bus	0,9	5*
T16	Bus	CZ-01	TZ-03	bus	4,1	6
T17	Bus	CZ-01	TZ-04	bus	3,4	5,5
T18	Bus	UI-01	CF-01	P1-P2	4,9	7

L mis.: misurata sul percorso disegnato. L quot. = (L mis. + 1 m) × 1,15, per eccesso a 0,5 m; * = minimo del fluido. Minimi: aria di mandata 2 m, frigo, gas 12 m, frigo, liquido 12 m, condensa 10 m, cavo ui-ue 12 m, bus 5 m.

FORATURE

F1 · T07 T08 T09 · tramezza t-ingresso-nord · controsoffitto
F2 · T10 · tramezza t-camere · controsoffitto
F3 · T14 · tramezza t-c1-c2 · traccia
F4 · T17 · tramezza t-soggiorno-nord · traccia
F5 · T18 · tramezza t-ingresso-nord · traccia
Fori per i pezzi a parete: B1, B2 nel muro t-camere; B3 nel muro t-camera-3; B4, B5 nel muro t-soggiorno-nord.

NOTE

1. Quote: controsoffitto per canali, linee frigo e condensa; traccia per cavi e bus, salvo dove la tabella dice altro. Le salite e le discese stanno nell'aggiunta della regola.
2. Le sigle e i numeri di tratta sono quelli dello schema funzionale.
3. Planimetria inventata per il caso di prova di REL-014: non è quella di nessun committente.

novec
VALORIZZAZIONE. EFFICIENTAMENTO. RIQUALIFICAZIONE.

COMMITTENTE: Caso di prova (planimetria inventata)	PROGETTO: REL-014 - canalizzato aria-aria, pianta di prova	SCALA: 1:50	DATA: 29.10.2026	APPROVATO / VERIFICATO / DISEGNATO: Nove C
INDIRIZZO: Nessun indirizzo: esempio	TITOLO TAVOLA: Pianta dei posizionamenti e dei tracciati	REVISIONE: Rev. 00	COMMESSA: PROVA-REL-014	TAVOLA: M.03