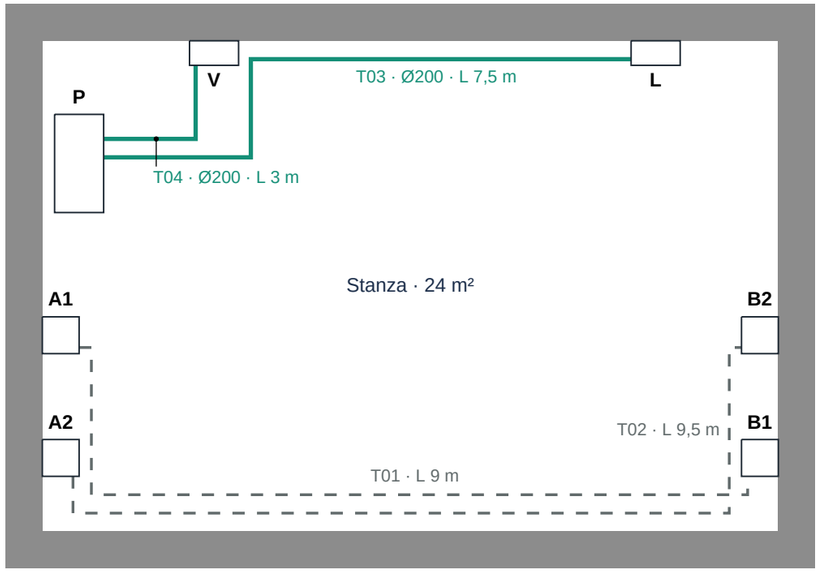


0 1 2 3 4 5 m

Scala 1:50

CASO DI PROVA: UN INCROCIO OBBLIGATO E UNO EVITABILE

Scala 1:50 su A3 · misure in metri

Percorsi indicativi, da verificare in sopralluogo.

LEGENDA

- Aria di mandata
- Condensa
- Pezzo posato: ingombro in pianta e sigla

TRATTE

Tratta	Fluido	Da	A	Dim.	L mis.	L quot.
T01	Condensa	A1	B1		6,8	9
T02	Condensa	A2	B2		7,1	9,5
T03	Aria di mandata	P	L	Ø200	5,1	7,5
T04	Aria di mandata	P	V	Ø200	1,4	3

L mis.: misurata sul percorso disegnato. L quot. = (L mis. + 1 m) × 1,15, per eccesso a 0,5 m.

NOTE

1. Quote: controsoffitto per canali, linee frigo e condensa; traccia per cavi e bus, salvo dove la tabella dice altro. Le salite e le discese stanno nell'aggiunta della regola.
2. Le sigle e i numeri di tratta sono quelli dello schema funzionale.
3. Una stanza 6 × 4 m. T01 e T02 hanno i capi alternati sui due muri, quindi si incrociano per forza: un sormonto e uno solo. T03 e T04 partono dallo stesso plenum: chi va lontano non deve sbarrare la strada a chi va vicino.

novec
VALORIZZAZIONE. EFFICIENTAMENTO. RIQUALIFICAZIONE.

COMMITTENTE: Caso di prova	PROGETTO: REL-014 - incrocio	SCALA: 1:50	DATA: 29.10.2026	APPROVATO	TAVOLA: P.02
INDIRIZZO: Nessuno	TITOLO TAVOLA: Caso di prova: un incrocio obbligato e uno evitabile	REVISIONE: Rev. 00	COMMESSA: PROVA-REL-014	VERIFICATO / DISEGNATO	