
BOZZA — cartiglio incompleto

CODICE	DESCRIZIONE	CARATTERISTICHE	MARCA	MODELLO
GT-01	Pompa di calore aria-acqua nr 1	15 kW	Shenling	HPM-V150W/R3
GT-02	Pompa di calore aria-acqua nr 2	15 kW	Shenling	HPM-V150W/R3
GT-03	Pompa di calore aria-acqua nr 3	15 kW	Shenling	HPM-V150W/R3
GT-04	Pompa di calore aria-acqua nr 4	15 kW	Shenling	HPM-V150W/R3
GT-05	Pompa di calore aria-acqua nr 5	15 kW	Shenling	HPM-V150W/R3
GT-06	Pompa di calore aria-acqua nr 6	15 kW	Shenling	HPM-V150W/R3
VOL-01	Volano termico a sei attacchi	200 l	Cordivari	Volano BS GBF 200
VOL-02	Volano termico a quattro attacchi	1000 l	Cordivari	Volano BS GBL 1000
BOL-01	Bollitore ACS	1000 l	–	–
CIR-01	Pompa di circolazione nr 1	–	DAB	EVOSTA3 80/130
CIR-02	Pompa di circolazione nr 2	–	Grundfos	MAGNA (sigla da completare)
CIR-03	Pompa di circolazione nr 3	–	Grundfos	MAGNA (sigla da completare)
CIR-04	Pompa di ricircolo sanitario	–	–	–
VE-01	Vaso di espansione nr 1	–	–	–
VE-02	Vaso di espansione nr 2	–	–	–
VE-03	Vaso di espansione sanitario	–	–	–

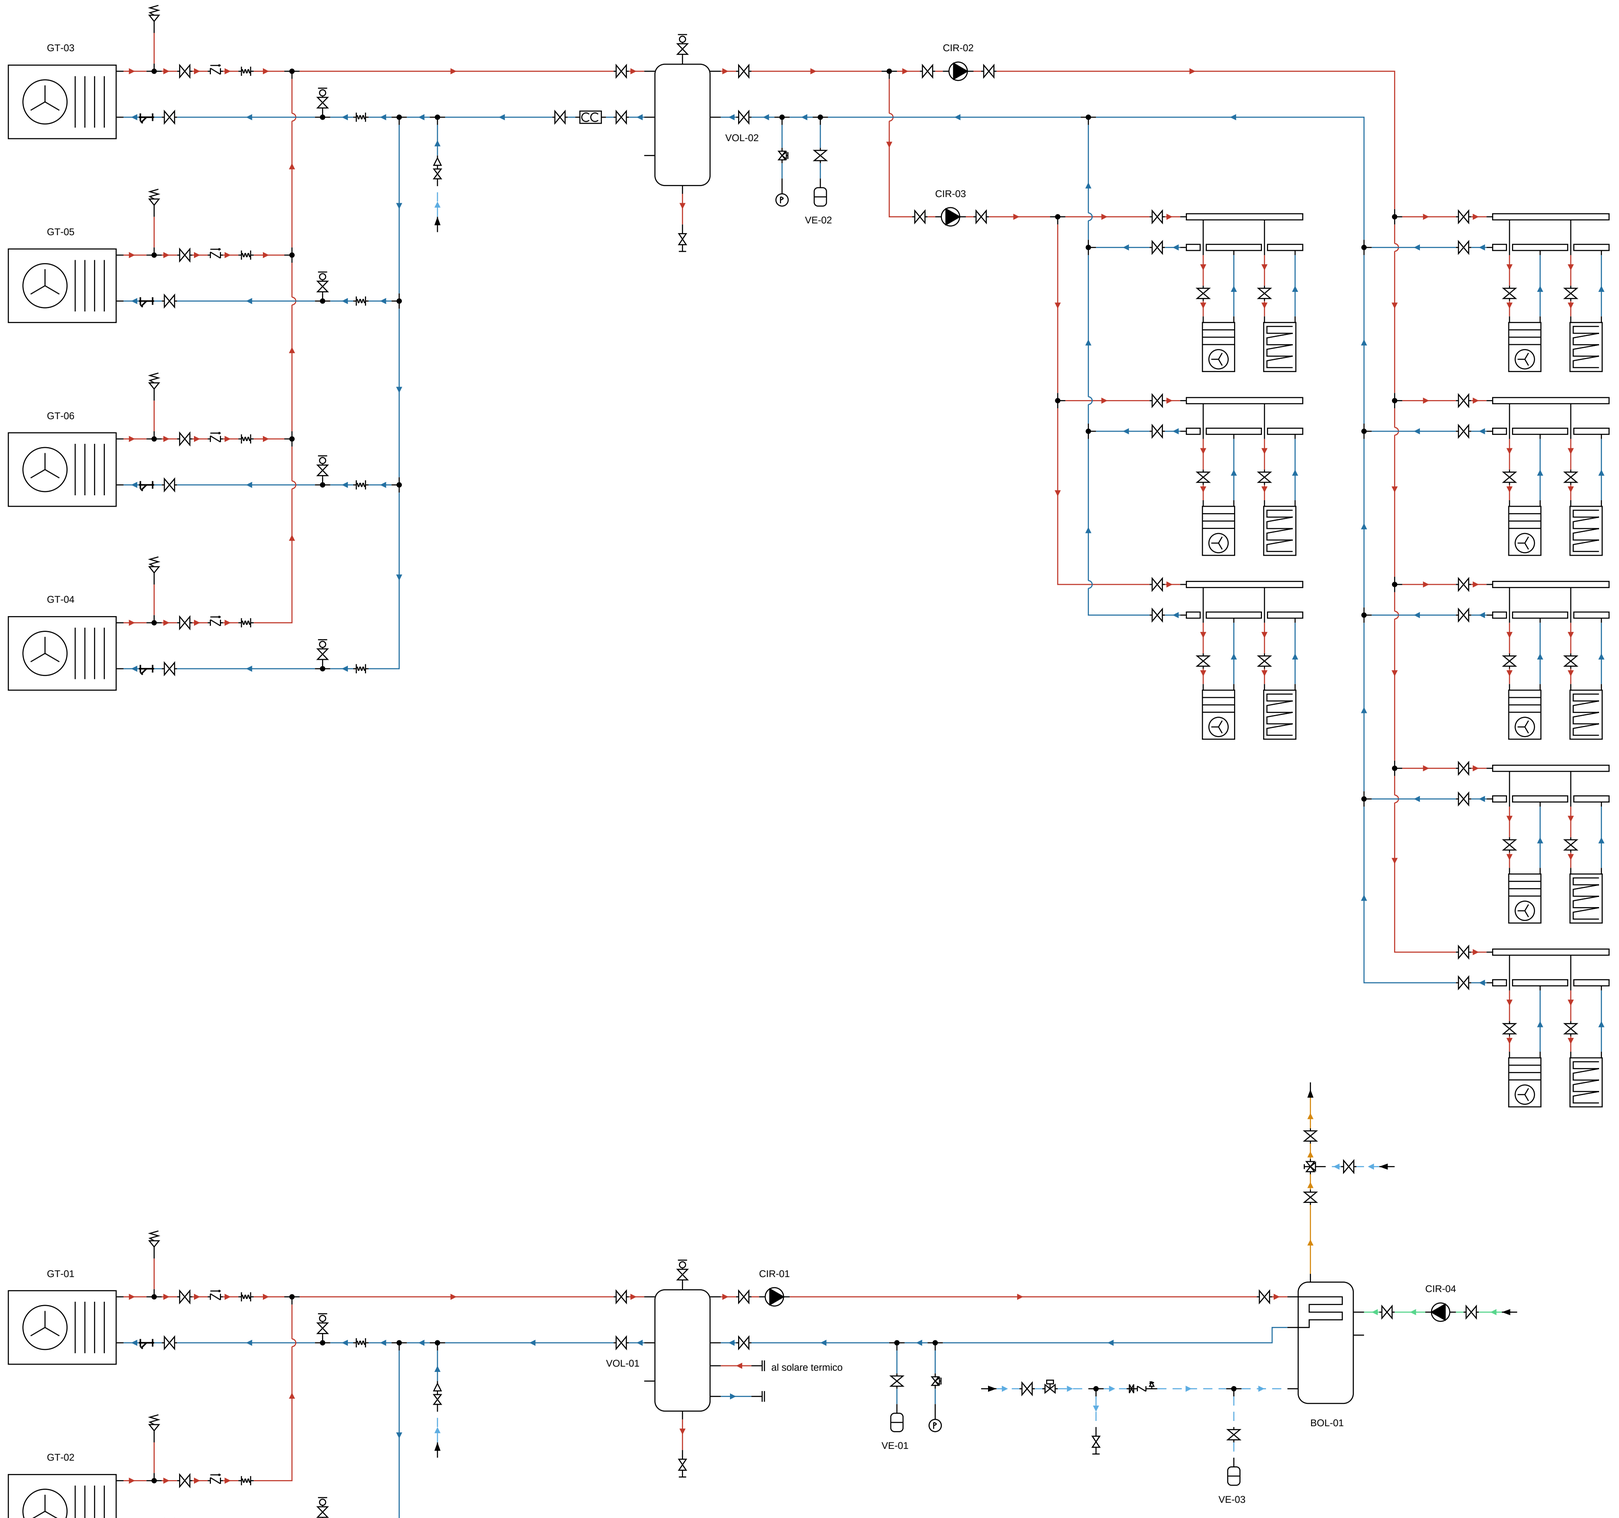

- Valvola di sfiato aria con rubinetto
- Volano termico a quattro attacchi
- Volano termico a sei attacchi
- Attacco predisposto
- Bollitore ACS
- Gruppo di sicurezza sanitario
- Attacco di scarico
- Vaso di espansione
- Ventilconvettore
- Gruppo di riempimento
- Giunto antivibrante
- Contatore di calore
- Pompa di calore aria-acqua
- Valvola miscelatrice termostatica
- Confine di rete
- Manometro
- Riduttore di pressione
- Pompa di circolazione
- Filtro a Y
- Derivazione a T
- Raccordo a T
- Pannello radiante
- Valvola di ritegno
- Rubinetto portamanometro a tre vie
- Valvola di intercettazione
- Valvola di sicurezza
- Collettore di zona con ritorno

- Acqua fredda sanitaria — andata
- Acqua calda sanitaria — andata
- Acqua calda sanitaria — ricircolo
- Acqua di riscaldamento — andata
- Acqua di riscaldamento — ritorno

novec
VALORIZZAZIONE. EFFICIENTAMENTO. RIQUALIFICAZIONE.

COMMITTENTE: Condominio (caso reale, anonimo)	PROGETTO: Sostituzione generatori di calore - centrale termica centralizzata a pompe di calore	SCALA: —	DATA: 03.10.2026	APPROVATO:	TAVOLA: DA DEFINIRE
INDIRIZZO: DA DEFINIRE	TITOLO TAVOLA: DA DEFINIRE	REVISIONE: Rev. 00	COMMESSA: DA DEFINIRE	VERIFICATO: DISEGNATO:	