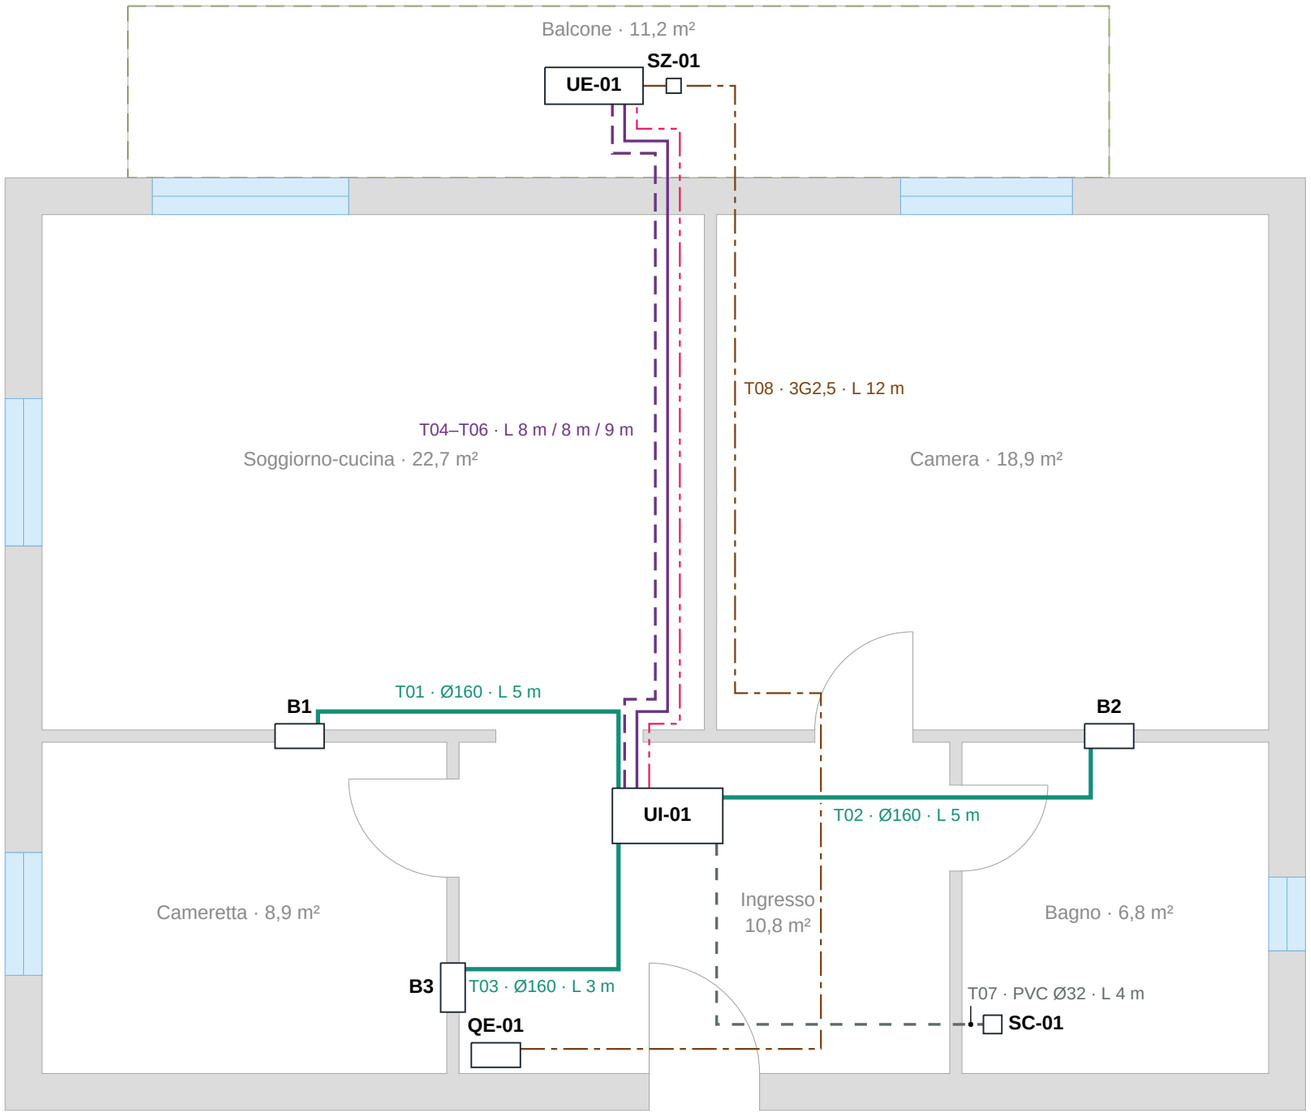


0 1 2 3 4 5 m

Scala 1:50

PIANTA DEI POSIZIONAMENTI E DEI TRACCIATI

Scala 1:50 su A3 · misure in metri

Percorsi indicativi, da verificare in sopralluogo.

LEGENDA

- Aria di mandata
- Refrigerante gas
- Refrigerante liquido
- Condensa
- Collegamento fra le unità
- Alimentazione elettrica
- Pezzo posato: ingombro e sigla
- Zona esterna praticabile

TRATTE

Tratta	Fluido	Da	A	Dim.	L prog.	L mis.	L quot.
T01	Aria di mandata	UI-01	B1	Ø160	5	3,2	7
T02	Aria di mandata	UI-01	B2	Ø160	5	3,4	7
T03	Aria di mandata	UI-01	B3	Ø160	3	2,3	5
T04	Frigo, liquido	UI-01	UE-01	1/4"	8	6,2	12*
T05	Frigo, gas	UI-01	UE-01	1/2"	8	6,2	12*
T06	Cavo UI-UE	UI-01	UE-01	4G1,5	9	6,2	13*
T07	Condensa	UI-01	SC-01	PVC Ø32	4	3,6	10*
T08	Alimentazione	QE-01	UE-01	3G2,5	12	11,6	15

Passano per organi in linea: T08 per SZ-01. L prog. del progettista, si quota; L mis. sul disegno, un controllo (! oltre il 15 %); L quot. = (L + 1 m) × 1,15 per eccesso a 0,5 m, regola della distinta; * minimo (frigo 12 m, condensa 10 m, bus 5 m, ramo aria 2 m, il cavo fra le unita' segue le linee frigo + 1 m); ° sulla misura, L prog. manca.

NOTE

1. Quote: canali, linee frigo e condensa in controsoffitto; cavi e bus in traccia, salvo dove la tabella dice altro. Salite e discese stanno nell'aggiunta della regola.
2. Sigle e numeri di tratta come lo schema funzionale e la distinta. Non controllati dal comando.
3. Ingombri da confermare (valori dichiarati, non del progettista ne' della scheda): UI-01.
4. Caso anonimo di REL-026 (C-3): la planimetria d'origine e' un disegno inventato (planimetria.pdf, disegnato da disegna_la_planimetria.py), con arredi, quote e retini; la base e' trascritta dalle sue quote e la tavola la ridisegna nella grafica standard.
5. Taratura: scala 1:50 dichiarata nel cartiglio, verificata sulla quota 10,60 e sulle porte da 80 cm.