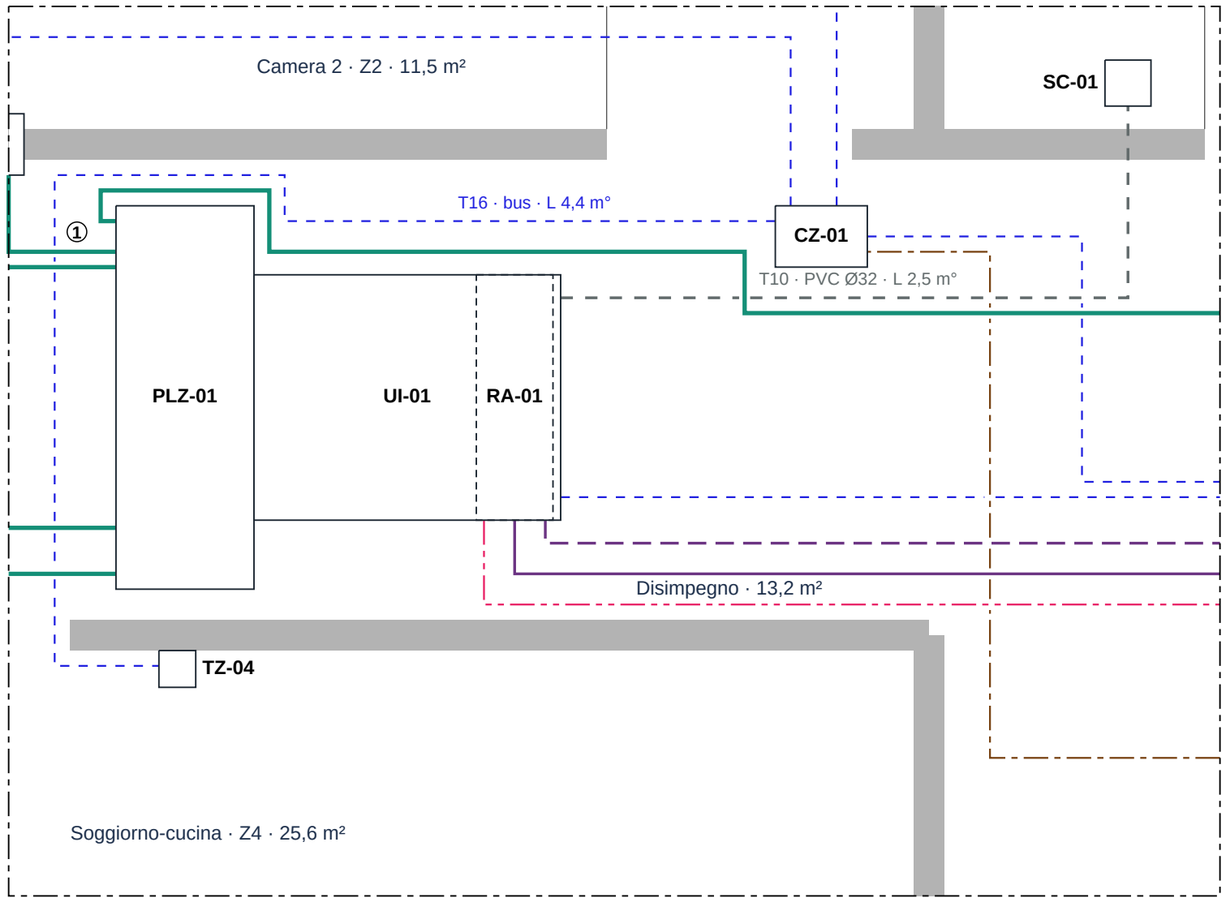



0 1 2 m

**Scala 1:20**

## PIANTA DEI POSIZIONAMENTI E DEI TRACCIATI - DETTAGLIO A

Scala 1:20 su A3 · misure in metri

**Percorsi indicativi, da verificare in sopralluogo.**

### LEGENDA

- Aria di mandata
- Refrigerante gas
- Refrigerante liquido
- Condensa
- Collegamento fra le unità
- Alimentazione elettrica
- Bus di comando
- Pezzo posato: ingombro e sigla
- Pezzo sotto un altro (altra quota)
- Zona esterna praticabile
- ① Scritta in legenda (testo sotto)

**Tratte, lunghezze e avvisi: tavola appartamento-aria-aria.**

### SCRITTE IN LEGENDA

① T02 · Ø200 · L 0,6 m°

### NOTE

1. Quote: canali, linee frigo e condensa in controsoffitto; cavi e bus in traccia, salvo dove la tabella dice altro. Salite e discese stanno nell'aggiunta della regola.
2. Sigle e numeri di tratta come lo schema funzionale e la distinta. Non controllati dal comando.
3. Ingombri da confermare (valori dichiarati, non del progettista ne' della scheda): CZ-01.
4. Sovrapposti, a quote diverse: RA-01 sotto UI-01.
5. Planimetria inventata per il caso di prova di REL-014: non è quella di nessun committente.
6. T06 (ripresa) è un raccordo diretto sotto la UI: non ha tracciato.
7. Il balcone è la sola zona esterna praticabile: il portoncino dà sul pianerottolo, e di lì le linee non passano.

VALORIZZAZIONE. EFFICIENTAMENTO. RIQUALIFICAZIONE.

| | | | | | |
|---|---|---|---|---|---|
| COMMITTENTE: Caso di prova (planimetria inventata) | PROGETTO: REL-014 - canalizzato aria-aria, pianta di prova | SCALA: 1:20 | DATA: 29.10.2026 | APPROVATO | TAVOLA: M.03.A |
| INDIRIZZO: Nessun indirizzo: esempio | TITOLO TAVOLA: Pianta dei posizionamenti e dei tracciati - dettaglio A | REVISIONE: Rev. 00 | COMMESSA: PROVA-REL-014 | VERIFICATO<br>DISEGNATO: Nove C | |