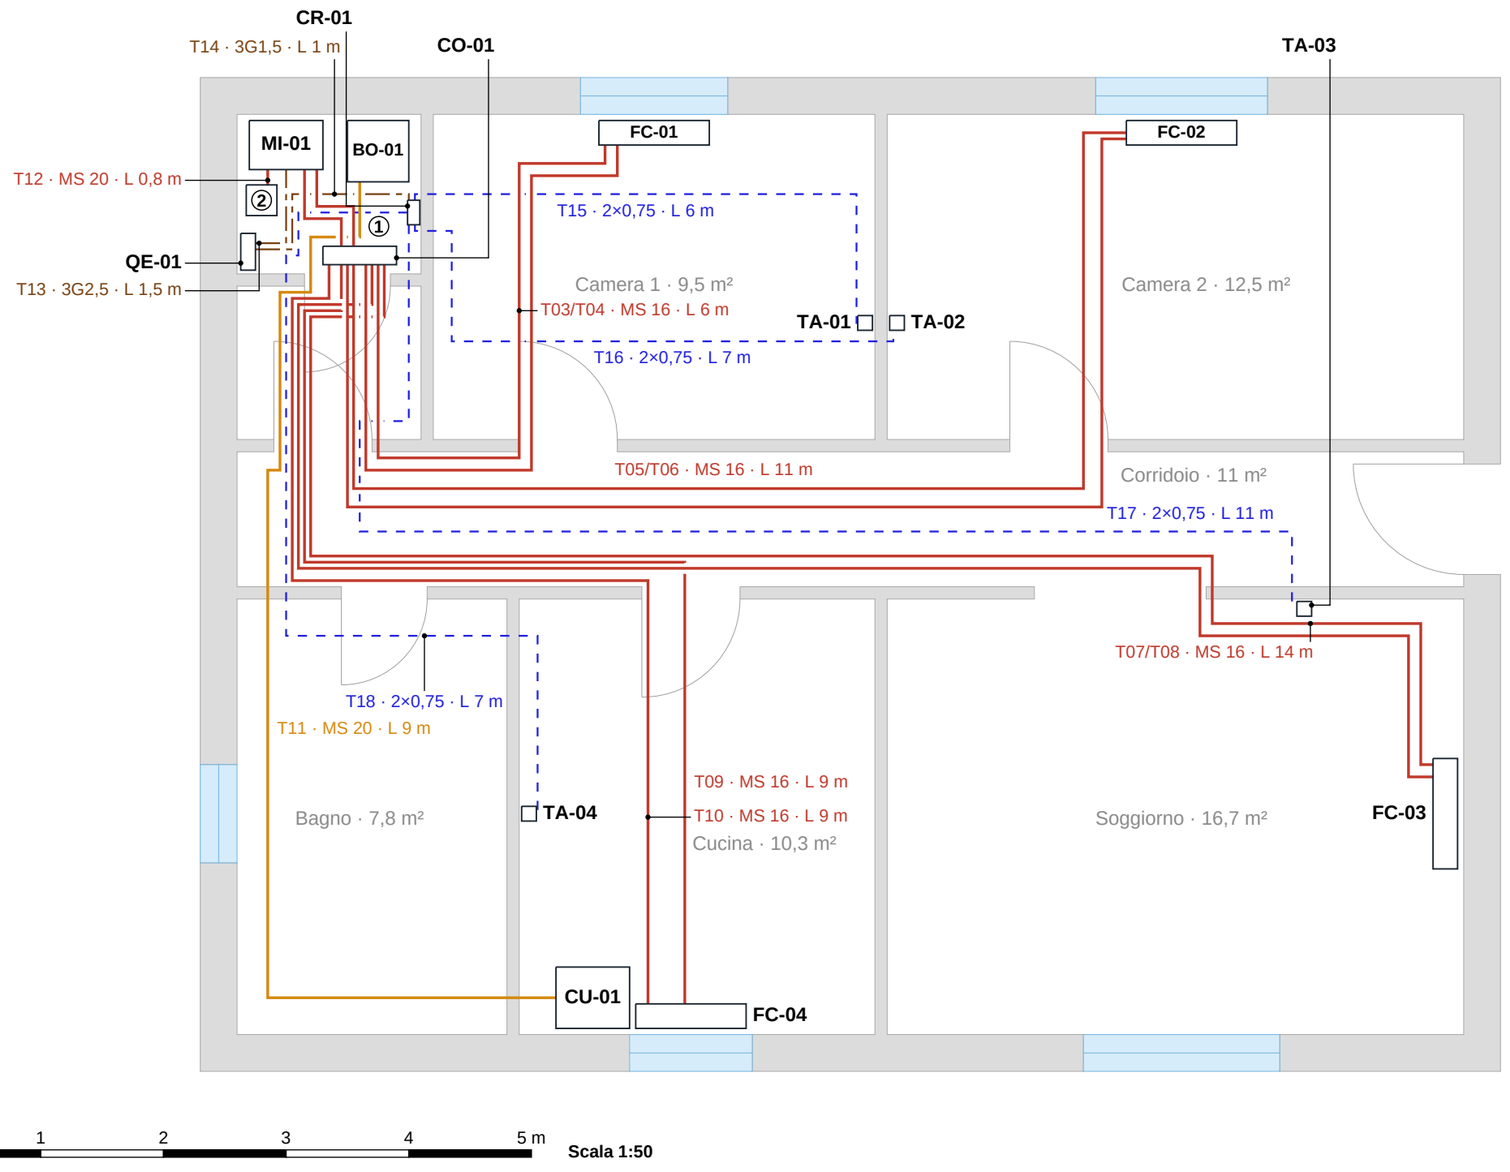



# PIANTA DEI POSIZIONAMENTI E DEI TRACCIATI

Scala 1:50 su A3 · misure in metri

**Percorsi indicativi, da verificare in sopralluogo.**

## LEGENDA

- Acqua calda sanitaria
- Acqua di riscaldamento
- Alimentazione elettrica
- Bus di comando
- Pezzo posato: ingombro e sigla
- ① Scritta in legenda (testo sotto)

## TRATTE

| Tratta | Fluido | Da | A | Dim. | L prog. | L mis. | L quot. |
|---|---|---|---|---|---|---|---|
| T01 | Acqua risc. | MI-01 | CO-01 | MS 26 | 1,5 | 0,9 | 3 |
| T02 | Acqua risc. | MI-01 | CO-01 | MS 26 | 1,5 | 0,9 | 3 |
| T03 | Acqua risc. | CO-01 | FC-01 | MS 16 | 6 | 6,4 | 8,5 |
| T04 | Acqua risc. | CO-01 | FC-01 | MS 16 | 6 | 6 | 8,5 |
| T05 | Acqua risc. | CO-01 | FC-02 | MS 16 | 11 | 11 | 14 |
| T06 | Acqua risc. | CO-01 | FC-02 | MS 16 | 11 | 11,3 | 14 |
| T07 | Acqua risc. | CO-01 | FC-03 | MS 16 | 14 | 14 | 17,5 |
| T08 | Acqua risc. | CO-01 | FC-03 | MS 16 | 14 | 13,8 | 17,5 |
| T09 | Acqua risc. | CO-01 | FC-04 | MS 16 | 9 | 9,4 | 11,5 |
| T10 | Acqua risc. | CO-01 | FC-04 | MS 16 | 9 | 9,2 | 11,5 |
| T11 | ACS | BO-01 | CU-01 | MS 20 | 9 | 9,8 | 11,5 |
| T12 | Acqua risc. | VE-01 | MI-01 | MS 20 | 0,8 | 0,1 | 2,5 |
| T13 | Alimentazione | QE-01 | MI-01 | 3G2,5 | 1,5 | 0,8 | 3 |
| T14 | Alimentazione | QE-01 | CR-01 | 3G1,5 | 1 | 1,8! | 2,5 |
| T15 | Bus | CR-01 | TA-01 | 2×0,75 | 6 | 4,7 | 8,5 |
| T16 | Bus | CR-01 | TA-02 | 2×0,75 | 7 | 4,9 | 9,5 |
| T17 | Bus | CR-01 | TA-03 | 2×0,75 | 11 | 11,1 | 14 |
| T18 | Bus | CR-01 | TA-04 | 2×0,75 | 7 | 8 | 9,5 |

L prog. del progettista, si quota; L mis. sul disegno, un controllo (! oltre il 15 %); L quot. = (L + 1 m) × 1,15 per eccesso a 0,5 m, regola della distinta; * minimo (frigo 12 m, condensa 10 m, bus 5 m, ramo aria 2 m, il cavo fra le unita' segue le linee frigo + 1 m); ° sulla misura, L prog. manca.

## AVVISI

– Misura oltre il 15 % di L prog.: T14 1,8 m su 1 (+75 %). Da verificare il percorso o il dato.

## SCRITTE IN LEGENDA

① T01/T02 · MS 26 · L 1,5 m

② VE-01

## NOTE

1. Quote: canali, linee frigo e condensa in controsoffitto; cavi e bus in traccia, salvo dove la tabella dice altro. Salite e discese stanno nell'aggiunta della regola.
2. Sigle e numeri di tratta come lo schema funzionale e la distinta. Non controllati dal comando.
3. Caso di prova anonimo (REL-026, C-1 e C-2): planimetria inventata. La centrale sta in un locale tecnico di 1,5 x 1,3 m: le scritte delle linee che ne escono non ci stanno, e vanno fuori dalla pianta col richiamo.
4. Mandata e ritorno di ogni ventilconvettore sono due tratte fra gli stessi pezzi: per FC-01 e FC-03 dichiarate in fascio, per FC-02 e FC-04 no. Due tratte che corrono insieme hanno una scritta sola (T03/T04); se non corrono insieme, ciascuna la sua.

novec
VALORIZZAZIONE. EFFICIENTAMENTO. RIQUALIFICAZIONE.

| | | | | | |
|---|---|---|---|---|---|
| COMMITTENTE: Caso di prova (planimetria inventata) | PROGETTO: REL-026 - le scritte fuori dalla pianta | SCALA: 1:50 | DATA: 13.11.2026 | APPROVATO | TAVOLA: M.03 |
| INDIRIZZO: Nessun indirizzo: esempio | TITOLO TAVOLA: Pianta dei posizionamenti e dei tracciati | REVISIONE: Rev. 00 | COMMESSA: PROVA-REL-026 | VERIFICATO<br>DISEGNATO: Nove C | |