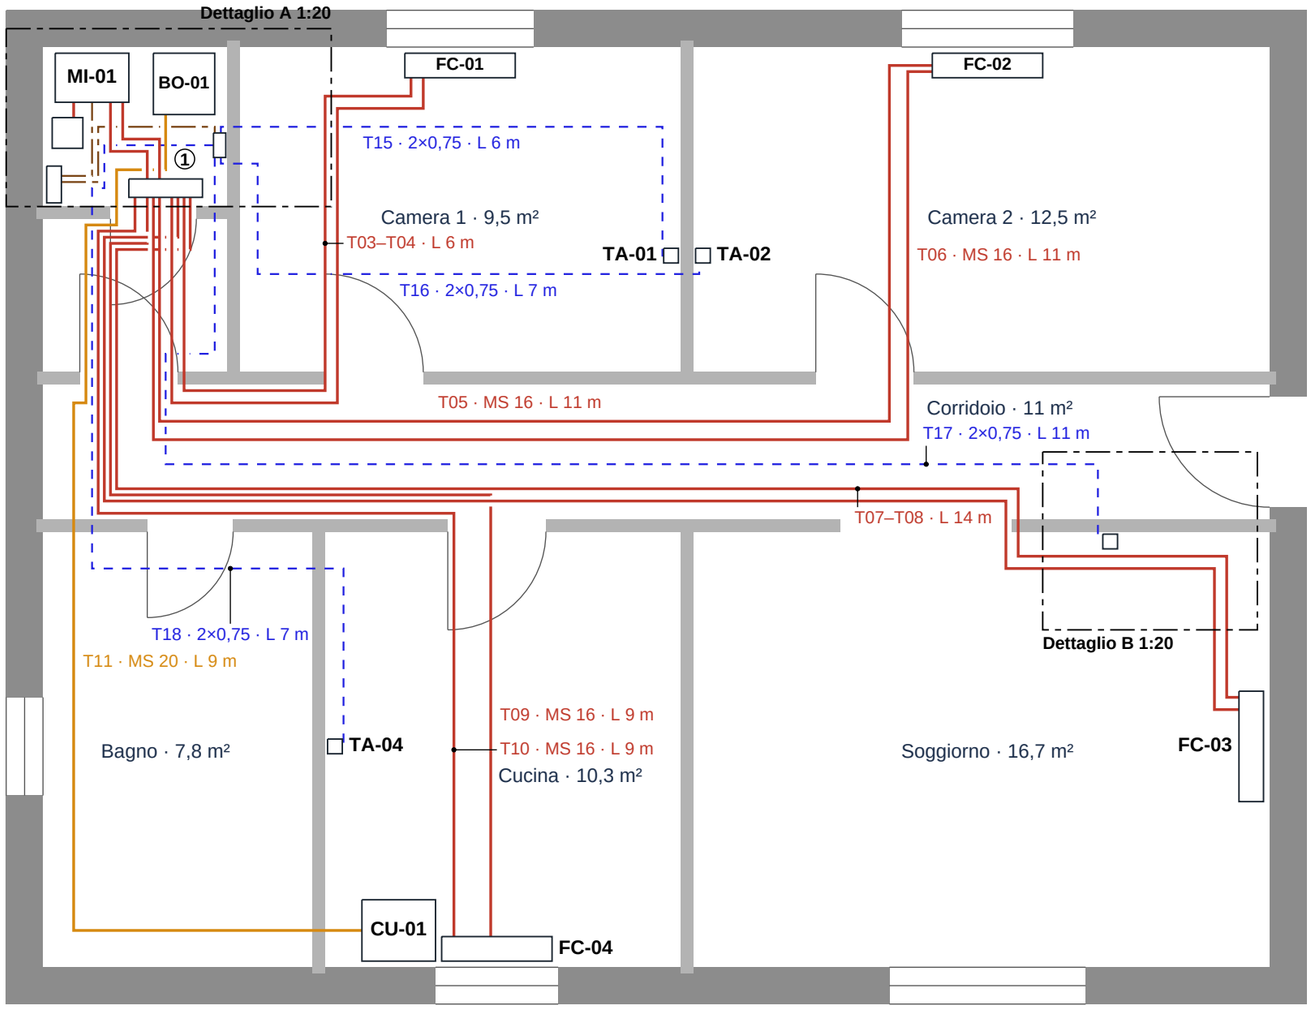


PIANTA DEI POSIZIONAMENTI E DEI TRACCIATI

Scala 1:50 su A3 · misure in metri

Percorsi indicativi, da verificare in sopralluogo.

LEGENDA

- Acqua calda sanitaria
- Acqua di riscaldamento
- Alimentazione elettrica
- Bus di comando
- Pezzo posato: ingombro e sigla
- ① Scritta in legenda (testo sotto)

TRATTE

Tratta	Fluido	Da	A	Dim.	L prog.	L mis.	L quot.
T01	Acqua risc.	MI-01	CO-01	MS 26	1,5	0,9	3
T02	Acqua risc.	MI-01	CO-01	MS 26	1,5	0,9	3
T03	Acqua risc.	CO-01	FC-01	MS 16	6	6,4	8,5
T04	Acqua risc.	CO-01	FC-01	MS 16	6	6	8,5
T05	Acqua risc.	CO-01	FC-02	MS 16	11	11	14
T06	Acqua risc.	CO-01	FC-02	MS 16	11	11,3	14
T07	Acqua risc.	CO-01	FC-03	MS 16	14	14	17,5
T08	Acqua risc.	CO-01	FC-03	MS 16	14	13,8	17,5
T09	Acqua risc.	CO-01	FC-04	MS 16	9	9,4	11,5
T10	Acqua risc.	CO-01	FC-04	MS 16	9	9,2	11,5
T11	ACS	BO-01	CU-01	MS 20	9	9,8	11,5
T12	Acqua risc.	VE-01	MI-01	MS 20	0,8	0,1	2,5
T13	Alimentazione	QE-01	MI-01	3G2,5	1,5	0,8	3
T14	Alimentazione	QE-01	CR-01	3G1,5	1	1,8!	2,5
T15	Bus	CR-01	TA-01	2×0,75	6	4,7	8,5
T16	Bus	CR-01	TA-02	2×0,75	7	4,9	9,5
T17	Bus	CR-01	TA-03	2×0,75	11	11,1	14
T18	Bus	CR-01	TA-04	2×0,75	7	8	9,5

L prog. del progettista, si quota; L mis. sul disegno, un controllo (! oltre il 15 %); L quot. = (L + 1 m) × 1,15 per eccesso a 0,5 m, regola della distinta; * minimo (frigo 12 m, condensa 10 m, bus 5 m, ramo aria 2 m, il cavo fra le unita' segue le linee frigo + 1 m); ° sulla misura, L prog. manca.

AVVISI

– Misura oltre il 15 % di L prog.: T14 1,8 m su 1 (+75 %). Da verificare il percorso o il dato.
– Dettagli A 1:20, B 1:20 (zone incorniciate): tavole centrale-fitta-dettaglio-<lettera>, perche' a 1:50 le scritte non ci stanno.

SCRITTE IN LEGENDA

① T01–T02 · L 1,5 m

NOTE

1. Quote: canali, linee frigo e condensa in controsoffitto; cavi e bus in traccia, salvo dove la tabella dice altro. Salite e discese stanno nell'aggiunta della regola.
2. Sigle e numeri di tratta come lo schema funzionale e la distinta. Non controllati dal comando.
3. Caso di prova anonimo (REL-026, C-1 e C-2): planimetria inventata. La centrale sta in un locale tecnico di 1,5 x 1,3 m: le scritte delle linee che ne escono non ci stanno, e vanno fuori dalla pianta col richiamo.
4. Mandata e ritorno di ogni ventilconvettore sono due tratte fra gli stessi pezzi: per FC-01 e FC-03 dichiarate in fascio, per FC-02 e FC-04 no. Due tratte che corrono insieme hanno una scritta sola (T03/T04); se non corrono insieme, ciascuna la sua.

noveC — VALORIZZAZIONE. EFFICIENTAMENTO. RIQUALIFICAZIONE.	COMMITTENTE: Caso di prova (planimetria inventata)	PROGETTO: REL-026 - le scritte fuori dalla pianta	SCALA: 1:50	DATA: 13.11.2026	APPROVATO / VERIFICATO / DISEGNATO: Nove C
	INDIRIZZO: Nessun indirizzo: esempio	TITOLO TAVOLA: Pianta dei posizionamenti e dei tracciati	REVISIONE: Rev. 00	COMMESSA: PROVA-REL-026	TAVOLA: M.03