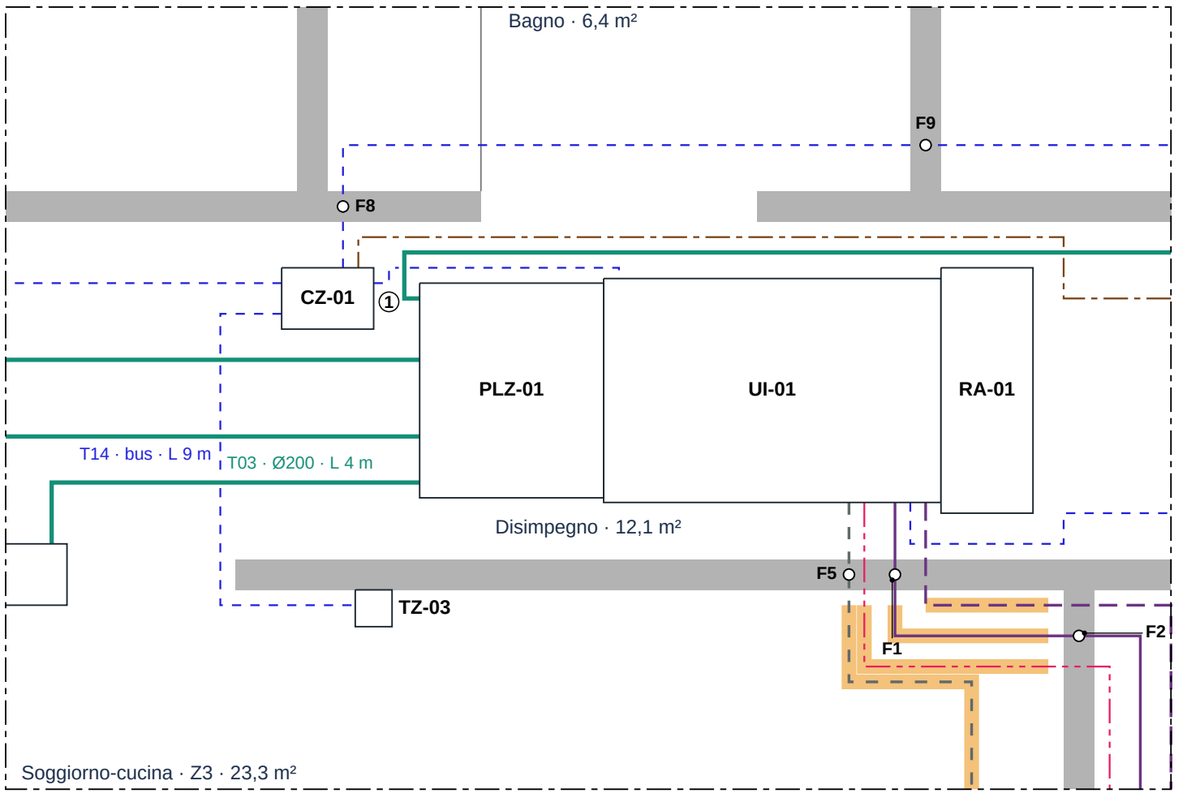


0 1 2 m

Scala 1:20

PIANTA DEI POSIZIONAMENTI E DEI TRACCIATI - DETTAGLIO A

Scala 1:20 su A3 · misure in metri

Percorsi indicativi, da verificare in sopralluogo.

LEGENDA

- Aria di mandata
- Refrigerante gas
- Refrigerante liquido
- Condensa
- Collegamento fra le unità
- Alimentazione elettrica
- Bus di comando
- Pezzo posato: ingombro e sigla
- Zona esterna praticabile
- Foratura (F1, F2…: elenco sotto)
- Fuori dal controsoffitto: da verificare
- ① Scritta in legenda (testo sotto)

Tratte, lunghezze, forature e avvisi: tavola collaudo-t1.

SCRITTE IN LEGENDA

① T16 · DA DEFINIRE · L 0,9 m°

NOTE

1. Quote: canali, linee frigo e condensa in controsoffitto; cavi e bus in traccia, salvo dove la tabella dice altro. Salite e discese stanno nell'aggiunta della regola.
2. Sigle e numeri di tratta come lo schema funzionale e la distinta. Non controllati dal comando.
3. Caso del collaudo indipendente REL-012 (t1): planimetria inventata, data a parole dal progettista del collaudo; non e' quella di nessun committente.
4. Misure interne 11 x 8 m, origine spostata di 0,30 m per il muro perimetrale.
5. Posizioni di centrale di zona, termostati, comando a filo, sezionatore e scarico della cucina assunte: da confermare.
6. Il terrazzo sta a sud del soggiorno: la profondita' di 1,5 m e' assunta, da confermare.

novec
VALORIZZAZIONE. EFFICIENTAMENTO. RIQUALIFICAZIONE.

COMMITTENTE: DA DEFINIRE	PROGETTO: Canalizzato aria-aria in pompa di calore - appartamento al secondo piano	SCALA: 1:20	DATA: 29.10.2026	APPROVATO	TAVOLA: DA DEFINIRE
INDIRIZZO: DA DEFINIRE	TITOLO TAVOLA: Pianta dei posizionamenti e dei tracciati - dettaglio A	REVISIONE: Rev. 00	COMMESSA: DA DEFINIRE	VERIFICATO / DISEGNATO	