


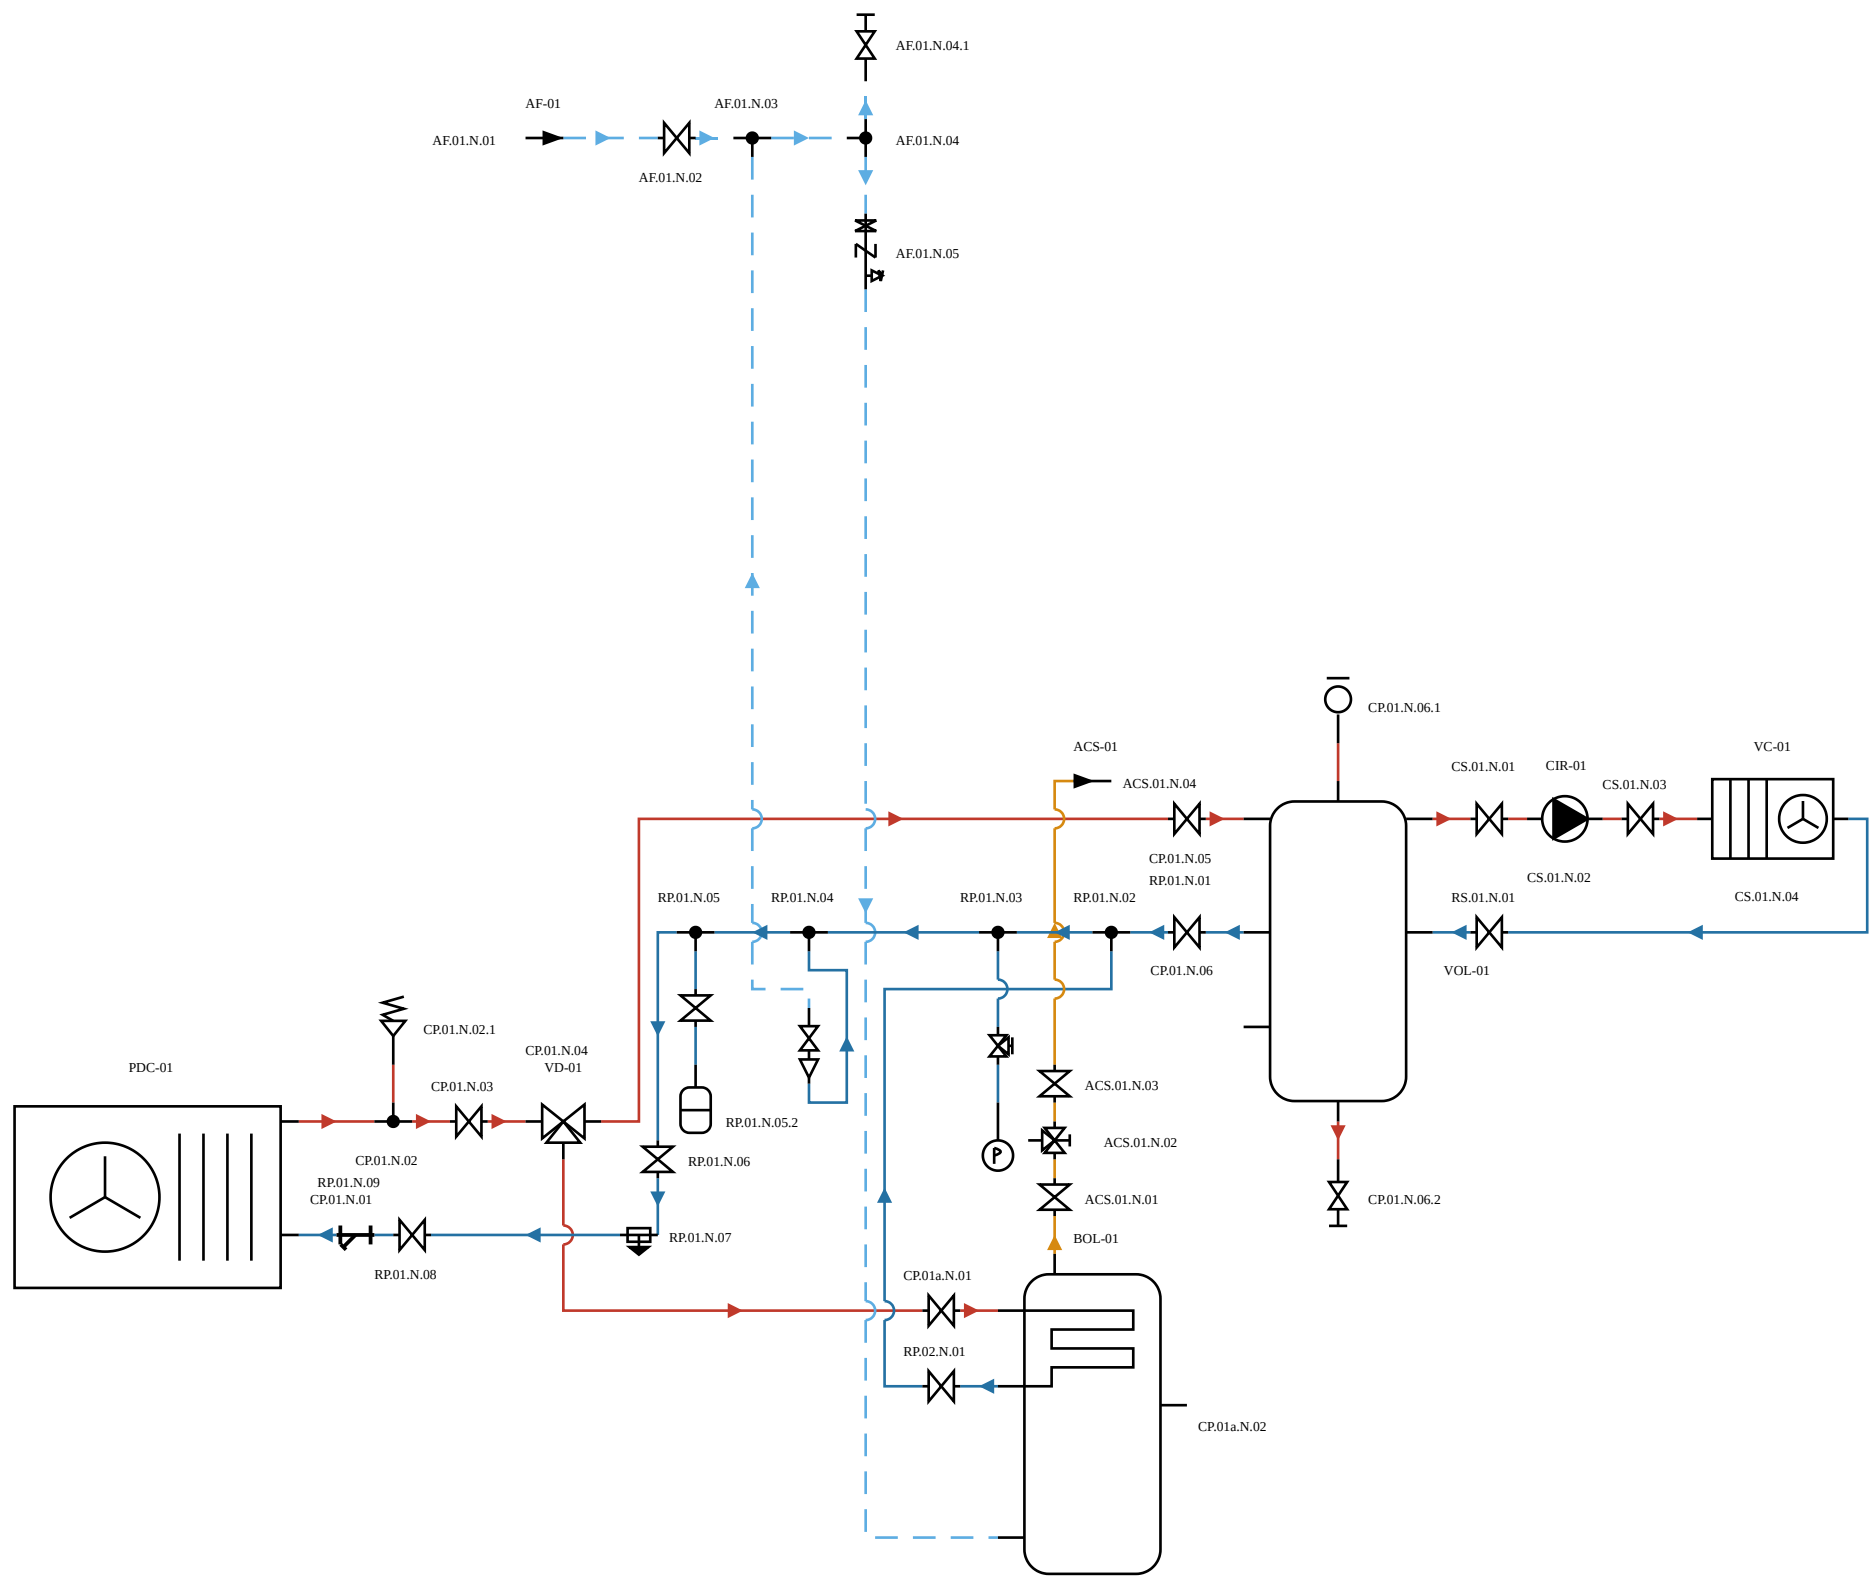

|  |                                    |
|--|------------------------------------|
|  | Valvola di sfato aria              |
|  | Valvano termico a quattro attacchi |
|  | Bollitore ACS                      |
|  | Gruppo di sicurezza sanitario      |
|  | Defangatore                        |
|  | Valvola deviatrice a tre vie       |
|  | Attacco di scarico                 |
|  | Vaso di espansione                 |
|  | Ventilconvettore                   |
|  | Gruppo di riempimento              |
|  | Pompa di calore aria-acqua         |
|  | Valvola miscelatrice termostatica  |
|  | Confine di rete                    |
|  | Manometro                          |
|  | Pompa di circolazione              |
|  | Filtro a Y                         |
|  | Derivazione a T                    |
|  | Raccordo a T                       |
|  | Rubinetto portamanometro a tre vie |
|  | Valvola di intercettazione         |
|  | Valvola di sicurezza               |
|  | Acqua fredda sanitaria — andata    |
|  | Acqua fredda sanitaria — ritorno   |
|  | Acqua calda sanitaria — andata     |
|  | Acqua calda sanitaria — ritorno    |
|  | Acqua di riscaldamento — andata    |
|  | Acqua di riscaldamento — ritorno   |