


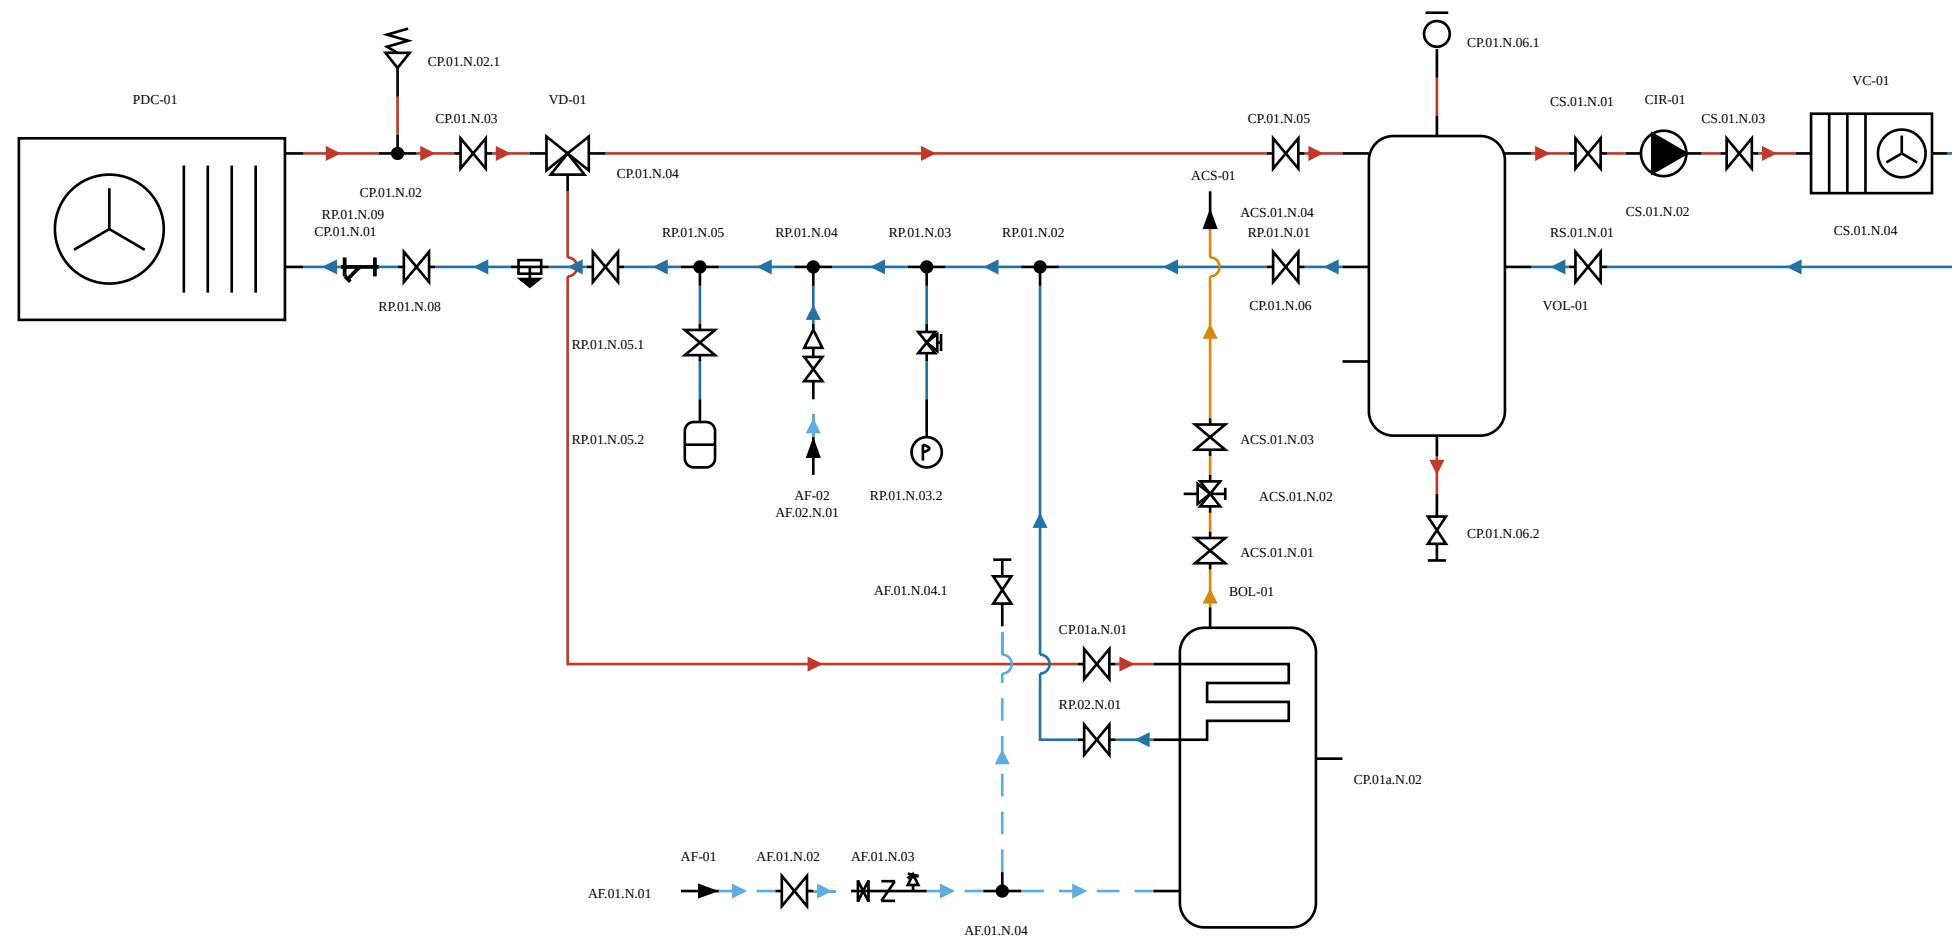

- | | |
|--|------------------------------------|
| | Valvola di sfidato aria |
| | Valvano termico a quattro attacchi |
| | Bollitore ACS |
| | Gruppo di sicurezza sanitario |
| | Defangatore |
| | Valvola deviatrice a tre vie |
| | Attacco di scarico |
| | Vaso di espansione |
| | Ventilconvettore |
| | Gruppo di riempimento |
| | Pompa di calore aria-acqua |
| | Valvola miscelatrice termostatica |
| | Confine di rete |
| | Manometro |
| | Pompa di circolazione |
| | Filtro a Y |
| | Derivazione a T |
| | Raccordo a T |
| | Rubinetto portamanometro a tre vie |
| | Valvola di intercettazione |
| | Valvola di sicurezza |
| | Acqua fredda sanitaria — andata |
| | Acqua fredda sanitaria — ritorno |
| | Acqua calda sanitaria — andata |
| | Acqua calda sanitaria — ritorno |
| | Acqua di riscaldamento — andata |
| | Acqua di riscaldamento — ritorno |