


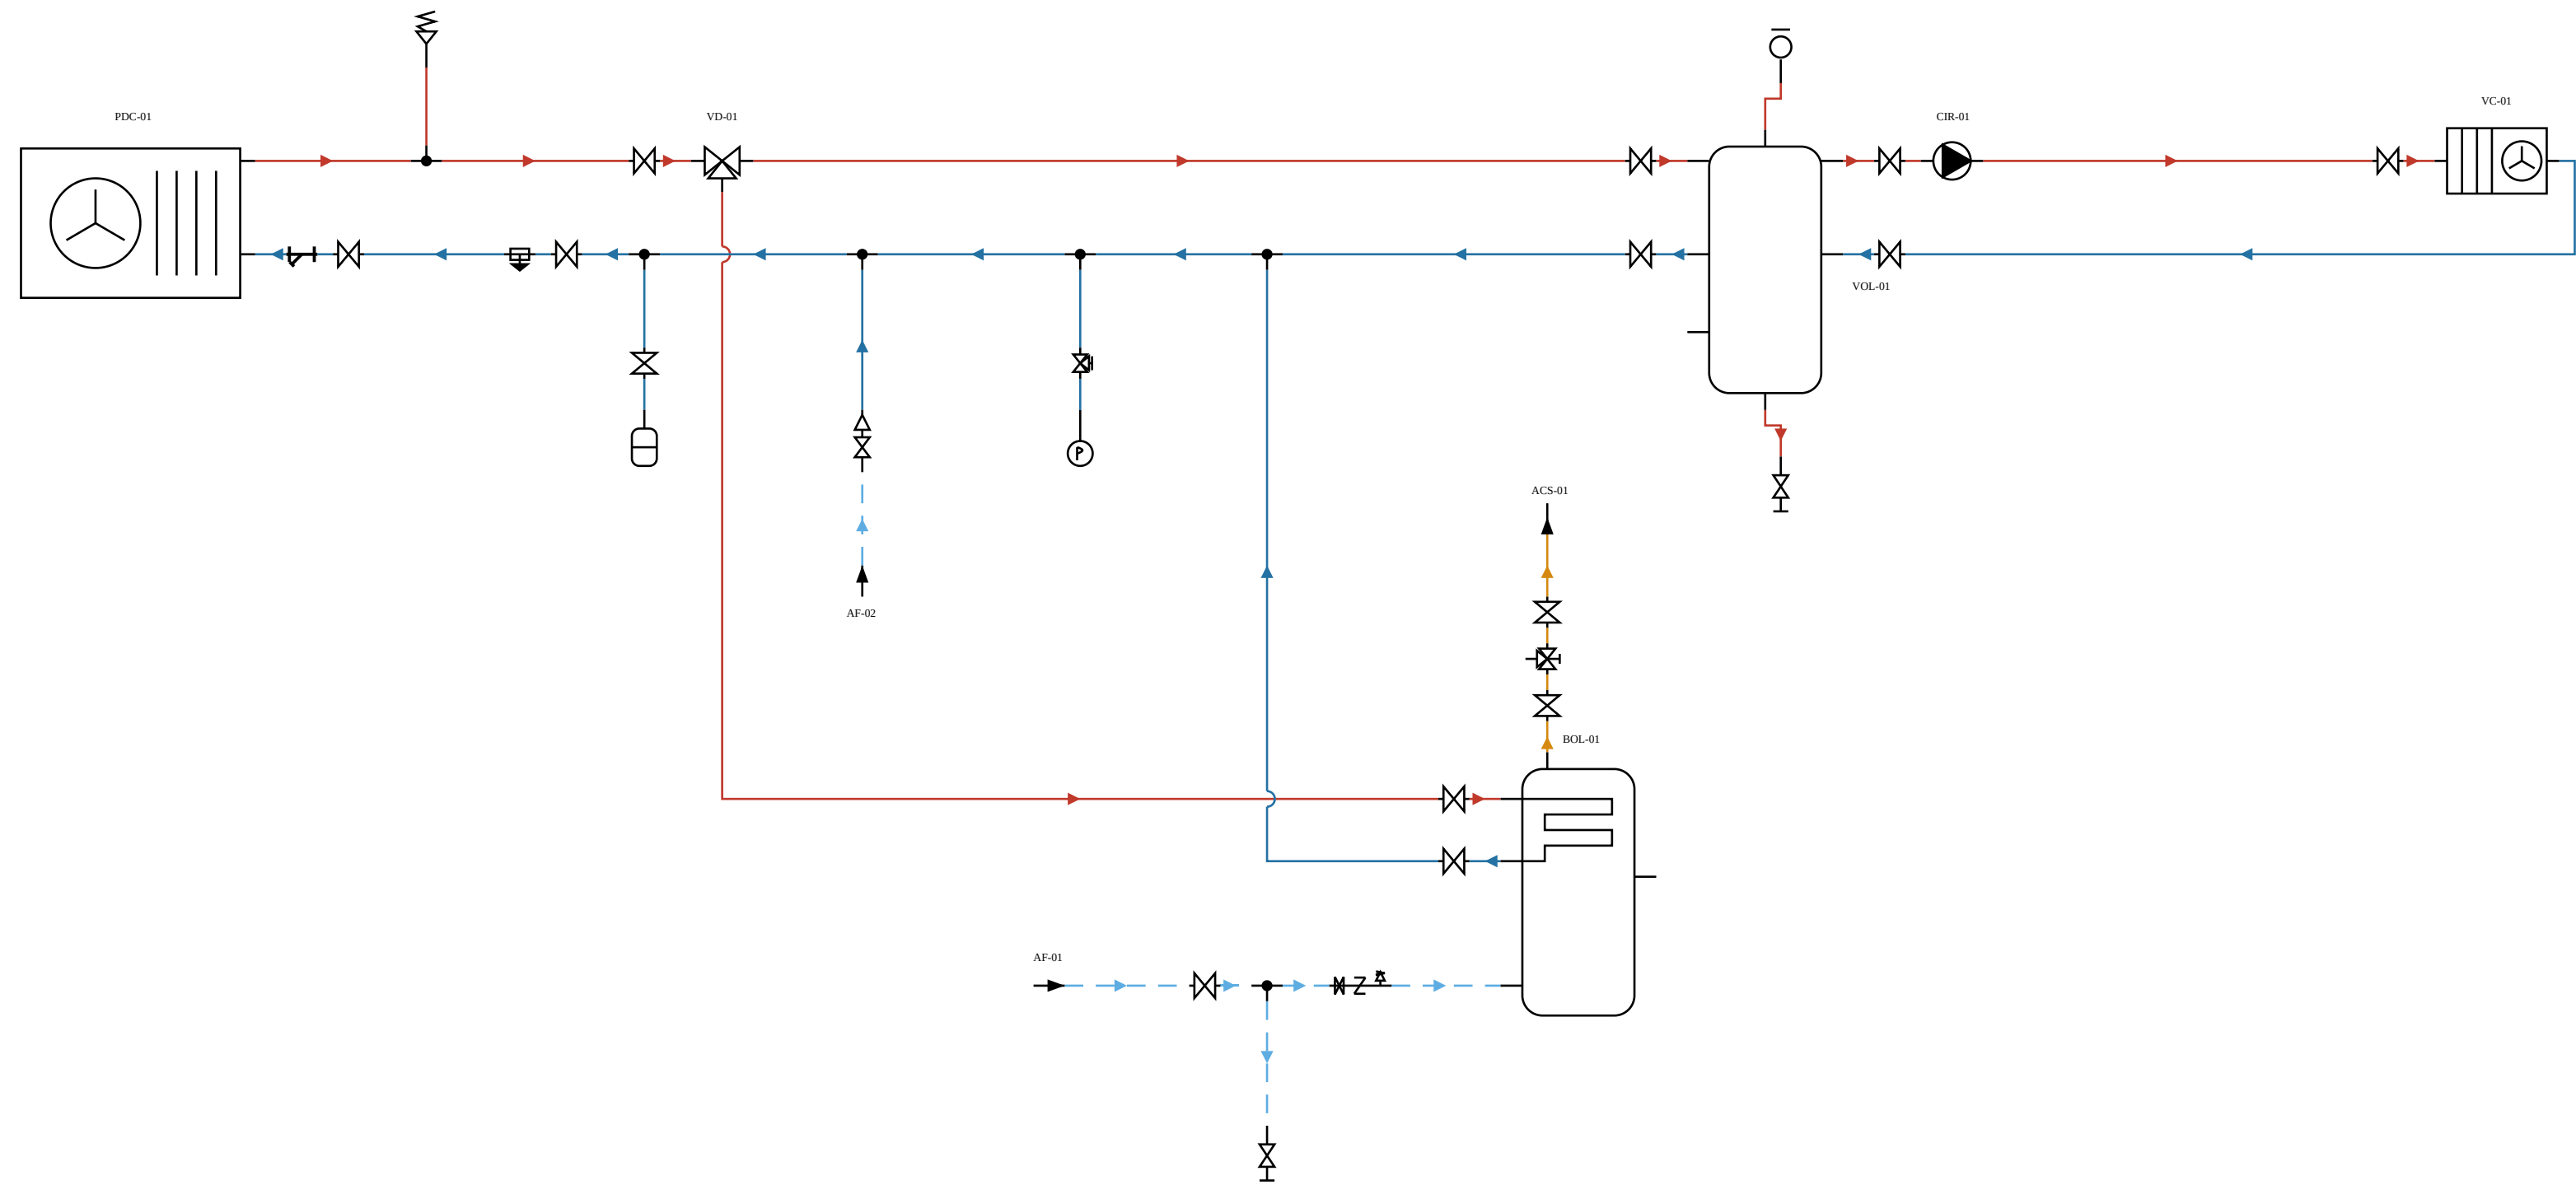

- Valvola di sfogo aria
- Valano termico a quattro attacchi
- Bollitore ACS
- Gruppo di sicurezza sanitario
- Defangatore
- Valvola deviatrice a tre vie
- Attacco di scarico
- Vaso di espansione
- Ventilconvettore
- Gruppo di riempimento
- Pompa di calore aria-acqua
- Valvola miscelatrice termostatica
- Confine di rete
- Manometro
- Pompa di circolazione
- Filtro a Y
- Derivazione a T
- Raccordo a T
- Rubinetto portamanometro a tre vie
- Valvola di intercettazione
- Valvola di sicurezza

- Acqua fredda sanitaria — andata
- Acqua fredda sanitaria — ritorno
- Acqua calda sanitaria — andata
- Acqua calda sanitaria — ritorno
- Acqua di riscaldamento — andata
- Acqua di riscaldamento — ritorno