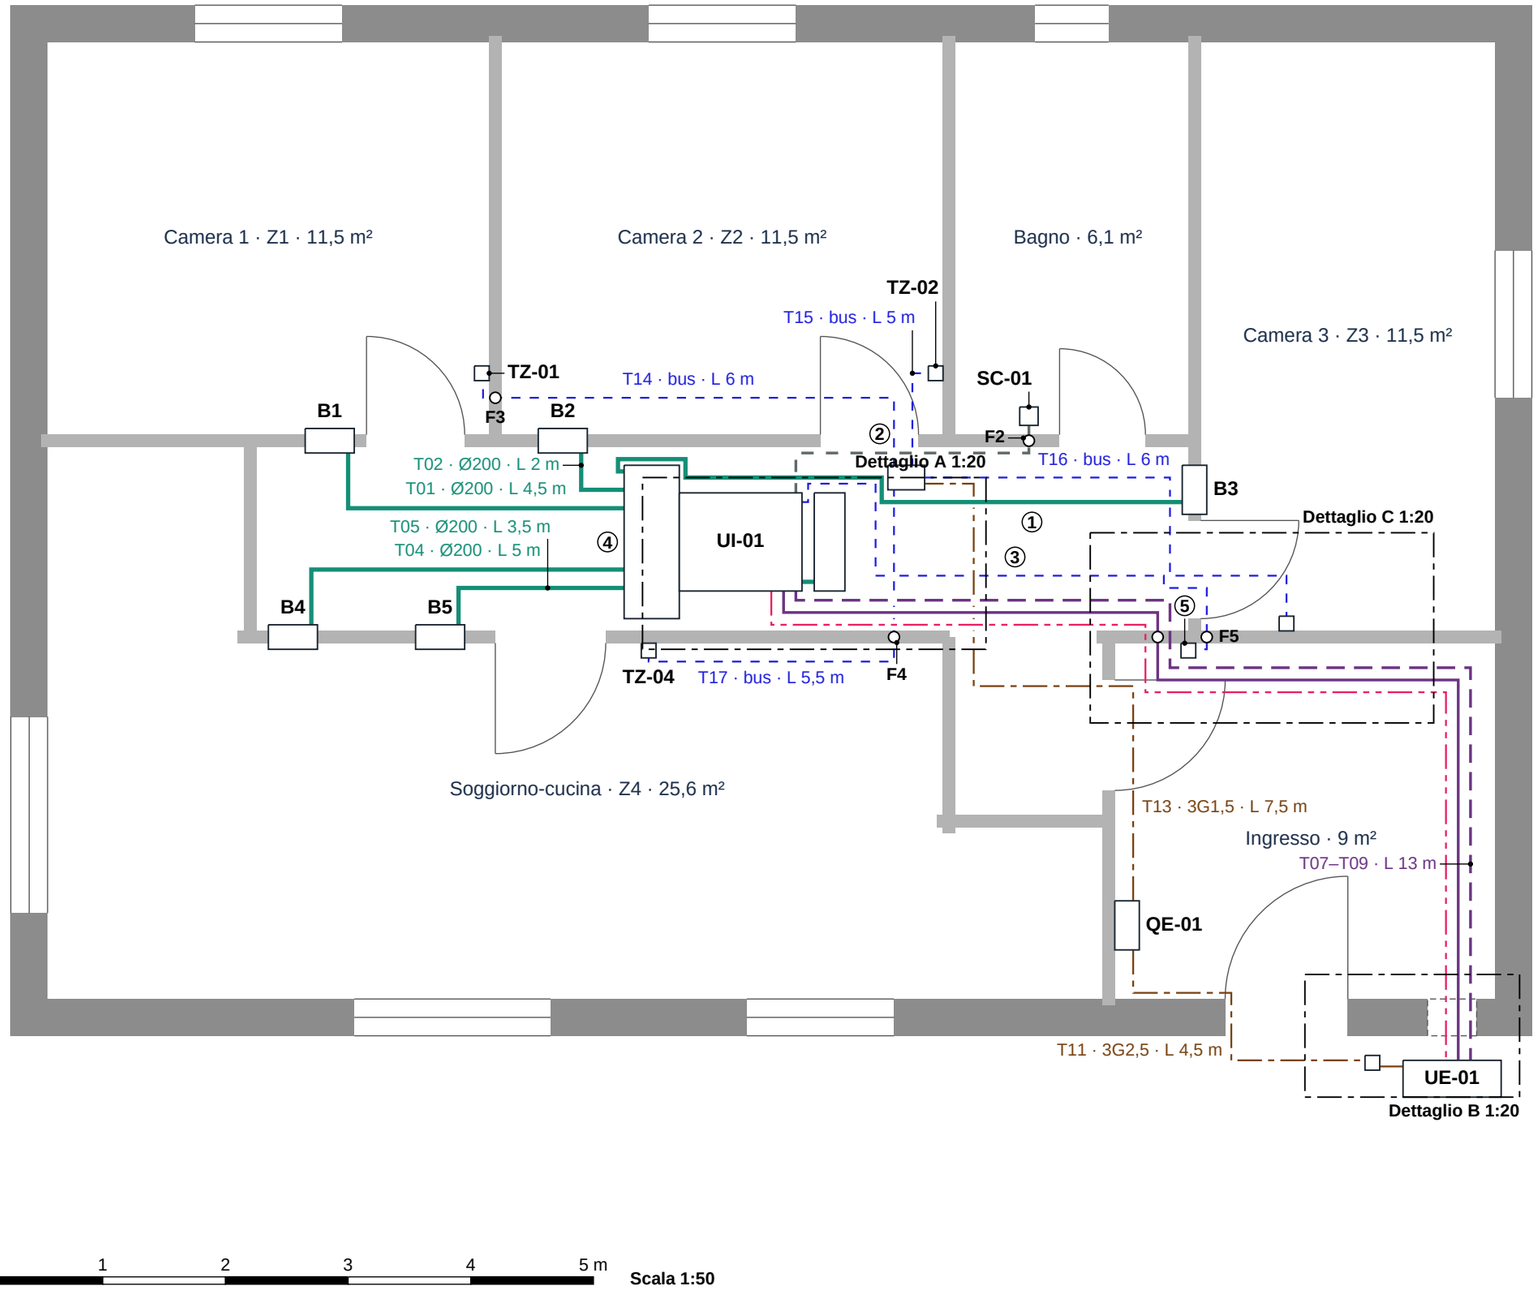


PIANTA DEI POSIZIONAMENTI E DEI TRACCIATI

Scala 1:50 su A3 · misure in metri

Percorsi indicativi, da verificare in sopralluogo.

LEGENDA

- Aria di ripresa
- Aria di mandata
- Refrigerante gas
- Refrigerante liquido
- Condensa
- Collegamento fra le unità
- Alimentazione elettrica
- Bus di comando
- Pezzo posato: ingombro e sigla
- Foratura (F1, F2…: elenco sotto)
- ① Scritta in legenda (testo sotto)

TRATTE

Tratta	Fluido	Da	A	Dim.	L prog.	L mis.	L quot.
T01	Aria di mandata	PLZ-01	B1	Ø200	—	2,7	4,5°
T02	Aria di mandata	PLZ-01	B2	Ø200	—	0,7	2°
T03	Aria di mandata	PLZ-01	B3	Ø200	—	5,1	7,5°
T04	Aria di mandata	PLZ-01	B4	Ø200	—	3	5°
T05	Aria di mandata	PLZ-01	B5	Ø200	—	1,6	3,5°
T06	Aria di ripresa	RA-01	UI-01	1000×250	—	0,1	2*°
T07	Frigo, liquido	UI-01	UE-01	6,35	—	9,3	12°
T08	Frigo, gas	UI-01	UE-01	12,7	—	9,3	12°
T09	Cavo UI-UE	UI-01	UE-01	4G1,5	—	9,3	13*°
T10	Condensa	UI-01	SC-01	PVC Ø32	—	2,5	10*°
T11	Alimentazione	QE-01	SZ-01	3G2,5	—	2,8	4,5°
T12	Alimentazione	SZ-01	UE-01	3G2,5	—	0,2	1,5°
T13	Alimentazione	QE-01	CZ-01	3G1,5	—	5,1	7,5°
T14	Bus	CZ-01	TZ-01	bus	—	4	6°
T15	Bus	CZ-01	TZ-02	bus	—	0,9	5*°
T16	Bus	CZ-01	TZ-03	bus	—	4,1	6°
T17	Bus	CZ-01	TZ-04	bus	—	3,4	5,5°
T18	Bus	UI-01	CF-01	bus	—	4,9	7°

L prog. del progettista, si quota; L mis. sul disegno, un controllo (! oltre il 15 %); L quot. = (L + 1 m) × 1,15 per eccesso a 0,5 m, regola della distinta; * minimo (frigo 12 m, condensa 10 m, bus 5 m, ramo aria 2 m, il cavo fra le unita' segue le linee frigo + 1 m); ° sulla misura, L prog. manca.

AVVISI

– Senza L prog., quotate sulla misura (°): T01, T02, T03, T04, T05, T06, T07, T08, T09, T10, T11, T12, T13, T14, T15, T16, T17, T18. Da riportare nel grafo, o da chiedere.
– Dettagli A 1:20, B 1:20, C 1:20 (zone incorniciate): tavole appartamento-aria-aria-dettaglio-<lettera>, perche' a 1:50 le scritte non ci stanno.

FORATURE

F1 · T07 T08 T09 · tramezza t-ingresso-nord · controsoffitto
F2 · T10 · tramezza t-camere · controsoffitto
F3 · T14 · tramezza t-c1-c2 · traccia
F4 · T17 · tramezza t-soggiorno-nord · traccia
F5 · T18 · tramezza t-ingresso-nord · traccia
Fori per i pezzi a parete: B1, B2 nel muro t-camere; B3 nel muro t-camera-3; B4, B5 nel muro t-soggiorno-nord.

SCRITTE IN LEGENDA

① T03 · Ø200 · L 7,5 m
② T10 · PVC Ø32 · L 10 m
③ T18 · P1-P2 · L 7 m
④ PLZ-01
⑤ CF-01

NOTE

1. Quote: canali, linee frigo e condensa in controsoffitto; cavi e bus in traccia, salvo dove la tabella dice altro. Salite e discese stanno nell'aggiunta della regola.
2. Sigle e numeri di tratta come lo schema funzionale e la distinta.
3. Planimetria inventata per il caso di prova di REL-014: non è quella di nessun committente.

noveC
VALORIZZAZIONE. EFFICIENTAMENTO. RIQUALIFICAZIONE.

COMMITTENTE: Caso di prova (planimetria inventata)	PROGETTO: REL-014 - canalizzato aria-aria, pianta di prova	SCALA: 1:50	DATA: 29.10.2026	APPROVATO / VERIFICATO / DISEGNATO: Nove C
INDIRIZZO: Nessun indirizzo: esempio	TITOLO TAVOLA: Pianta dei posizionamenti e dei tracciati	REVISIONE: Rev. 00	COMMESSA: PROVA-REL-014	TAVOLA: M.03