
BOZZA — cartiglio incompleto

CODICE	DESCRIZIONE	CARATTERISTICHE	MARCA	MODELLO
UE-01	Unità esterna split a pompa di calore	7,1 kW	Mitsubishi Electric	SUZ-M71VA
UI-01	Unità interna canalizzata ad espansione diretta	–	Mitsubishi Electric	PEAD-M71JA
PLZ-01	Plenum motorizzato di zona a quattro serrande	–	Airzone	–
CZ-01	Centrale di zona	–	Airzone	–
TZ-01	Termostato di zona nr 1	–	Airzone	Think a filo
TZ-02	Termostato di zona nr 2	–	Airzone	Think a filo
TZ-03	Termostato di zona nr 3	–	Airzone	Think a filo
CF-01	Comando a filo dell'unità	–	Mitsubishi Electric	PAR-41MAA

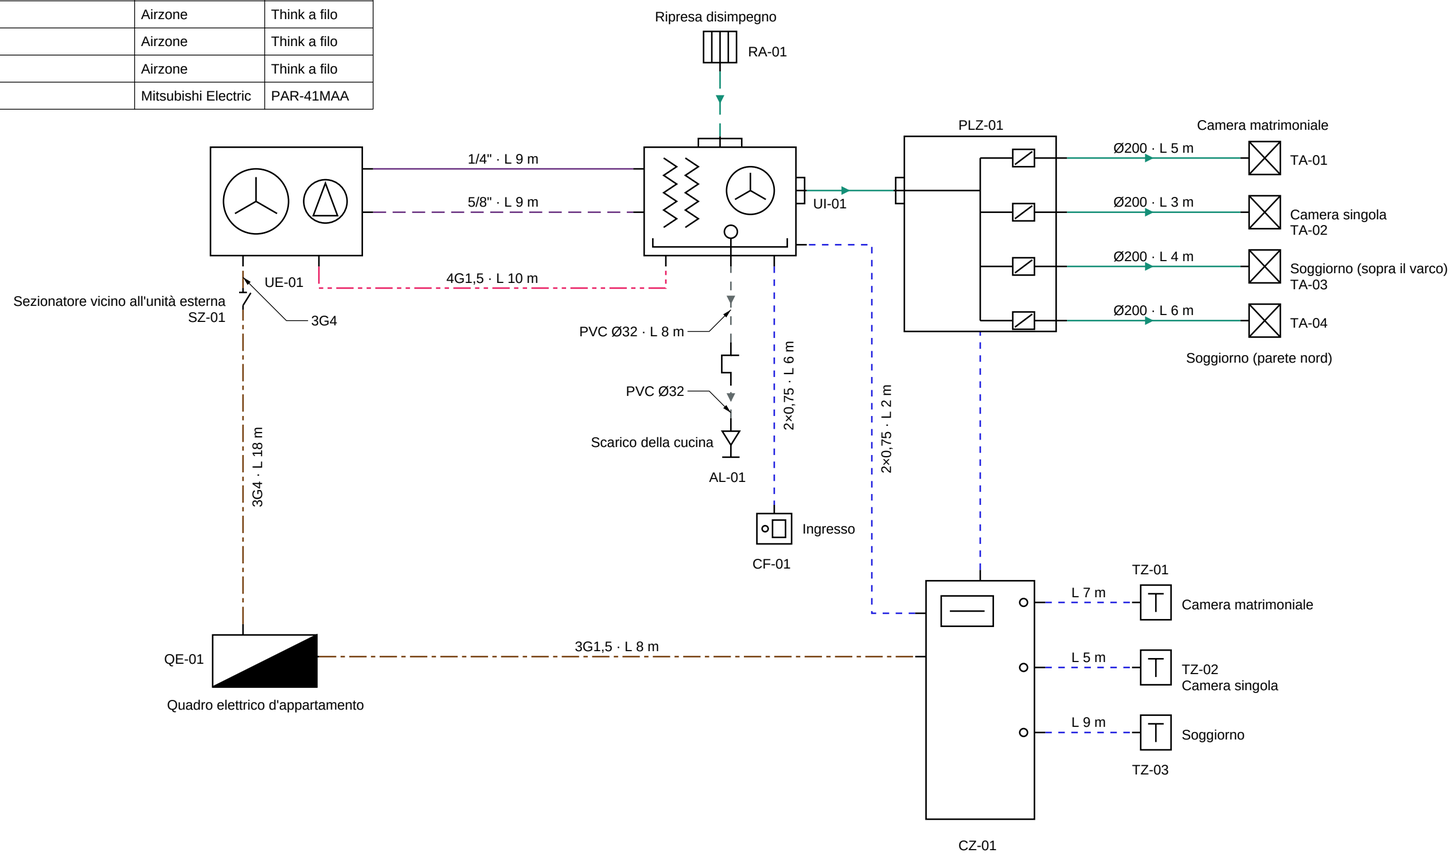

- Bocchetta di mandata con plenum di raccordo
- Allaccio allo scarico
- Sifone ispezionabile
- Unità interna canalizzata
- Quadro elettrico
- Sezionatore onnipolare
- Griglia di ripresa con plenum e filtro
- Termostato di zona
- Unità esterna ad espansione diretta
- Comando a filo
- Centrale di zona
- Plenum motorizzato di zona a quattro serrande

- Condensa
- Bus di comando
- Collegamento fra le unità
- Alimentazione elettrica
- Refrigerante gas
- Refrigerante liquido
- Aria di ripresa
- Aria di mandata
- Ø · L sezione e lunghezza, dato del progettista

TABELLA DELLE TRATTE — diametri e lunghezze per la quotazione

Tratto	Da - a	Ø / sezione	Materiale	Q m³/h	v m/s	L stim. m	L quot. m
T01	PLZ-01 - TA-01	Ø200	flessibile coibentato	300	2,7	5	7
T02	PLZ-01 - TA-02	Ø200	flessibile coibentato	220	1,9	3	5
T03	PLZ-01 - TA-03	Ø200	flessibile coibentato	300	2,7	4	6
T04	PLZ-01 - TA-04	Ø200	flessibile coibentato	300	2,7	6	8,5
T05	RA-01 - UI-01	800×300	plenum di ripresa coibentato				
T06	UE-01 - UI-01	1/4"	Cu ricotto pre-isolato, isolamento min. 10 mm			9	12
T07	UE-01 - UI-01	5/8"	Cu ricotto pre-isolato, isolamento min. 13 mm			9	12
T08	UI-01 - SIF-01 - AL-01	PVC Ø32	PVC rigido, pendenza min. 1%			8	10,5

Tratto	Da - a	Ø / sezione	Materiale	Q m³/h	v m/s	L stim. m	L quot. m
T09	QE-01 - CZ-01	3G1,5	FG16OR16			8	10,5
T10	QE-01 - SZ-01 - UE-01	3G4	FG16OR16			18	22
T11	UE-01 - UI-01	4G1,5	a doppio isolamento			10	13
T12	CZ-01 - TZ-01	-	cavo di bus			7	9,5
T13	CZ-01 - TZ-02	-	cavo di bus			5	7
T14	CZ-01 - TZ-03	-	cavo di bus			9	11,5
T15	CZ-01 - UI-01	2×0,75	cavo di bus			2	5
T16	UI-01 - CF-01	2×0,75	cavo di bus			6	8,5

NOTE DELLA DISTINTA

1. «L da quotare» = (L stimata + 1 m) × 1,15, per eccesso a 0,5 m; minimi: fluido frigorigeno in fase liquida, fluido frigorigeno in fase gassosa 12 m; condensa 10 m; bus di comando 5 m; aria di mandata, aria di ripresa 2 m. La L stimata è un dato del progettista, scritta su ogni tratto.
2. Quantità indicative per un prezzo a corpo, fisso e invariabile: l'installatore le verifica nel sopralluogo obbligatorio prima dell'offerta; le varianti hanno solo il prezzo unitario.
3. Velocità nei tratti di aria di mandata da 1,9 a 2,7 m/s, sulla sezione lorda, dalle portate e dalle sezioni del progettista (verifica: segnala, non corregge).
4. Fornitura: apparecchiature fornite da Nove C; bocchette e griglie, opere edili del Committente; messa in servizio con Nove C.
5. La distinta non progetta: lunghezze, sezioni, portate, protezioni, marca e modello sono dati del progettista; la distinta li maggiora e ne conta il corredo con regole scritte, ciascuna con la sua fonte (regole f8b849f909489495).

novec
VALORIZZAZIONE. EFFICIENTAMENTO. RIQUALIFICAZIONE.

COMMITTENTE: DA DEFINIRE
INDIRIZZO: DA DEFINIRE
PROGETTO: Canalizzato aria-aria in pompa di calore - appartamento al secondo piano
TITOLO TAVOLA: DA DEFINIRE
SCALA: —
DATA: 29.10.2026
REVISIONE: Rev. 00
COMMESSA: DA DEFINIRE
APPROVATO:
VERIFICATO:
DISEGNATO:
TAVOLA: DA DEFINIRE