


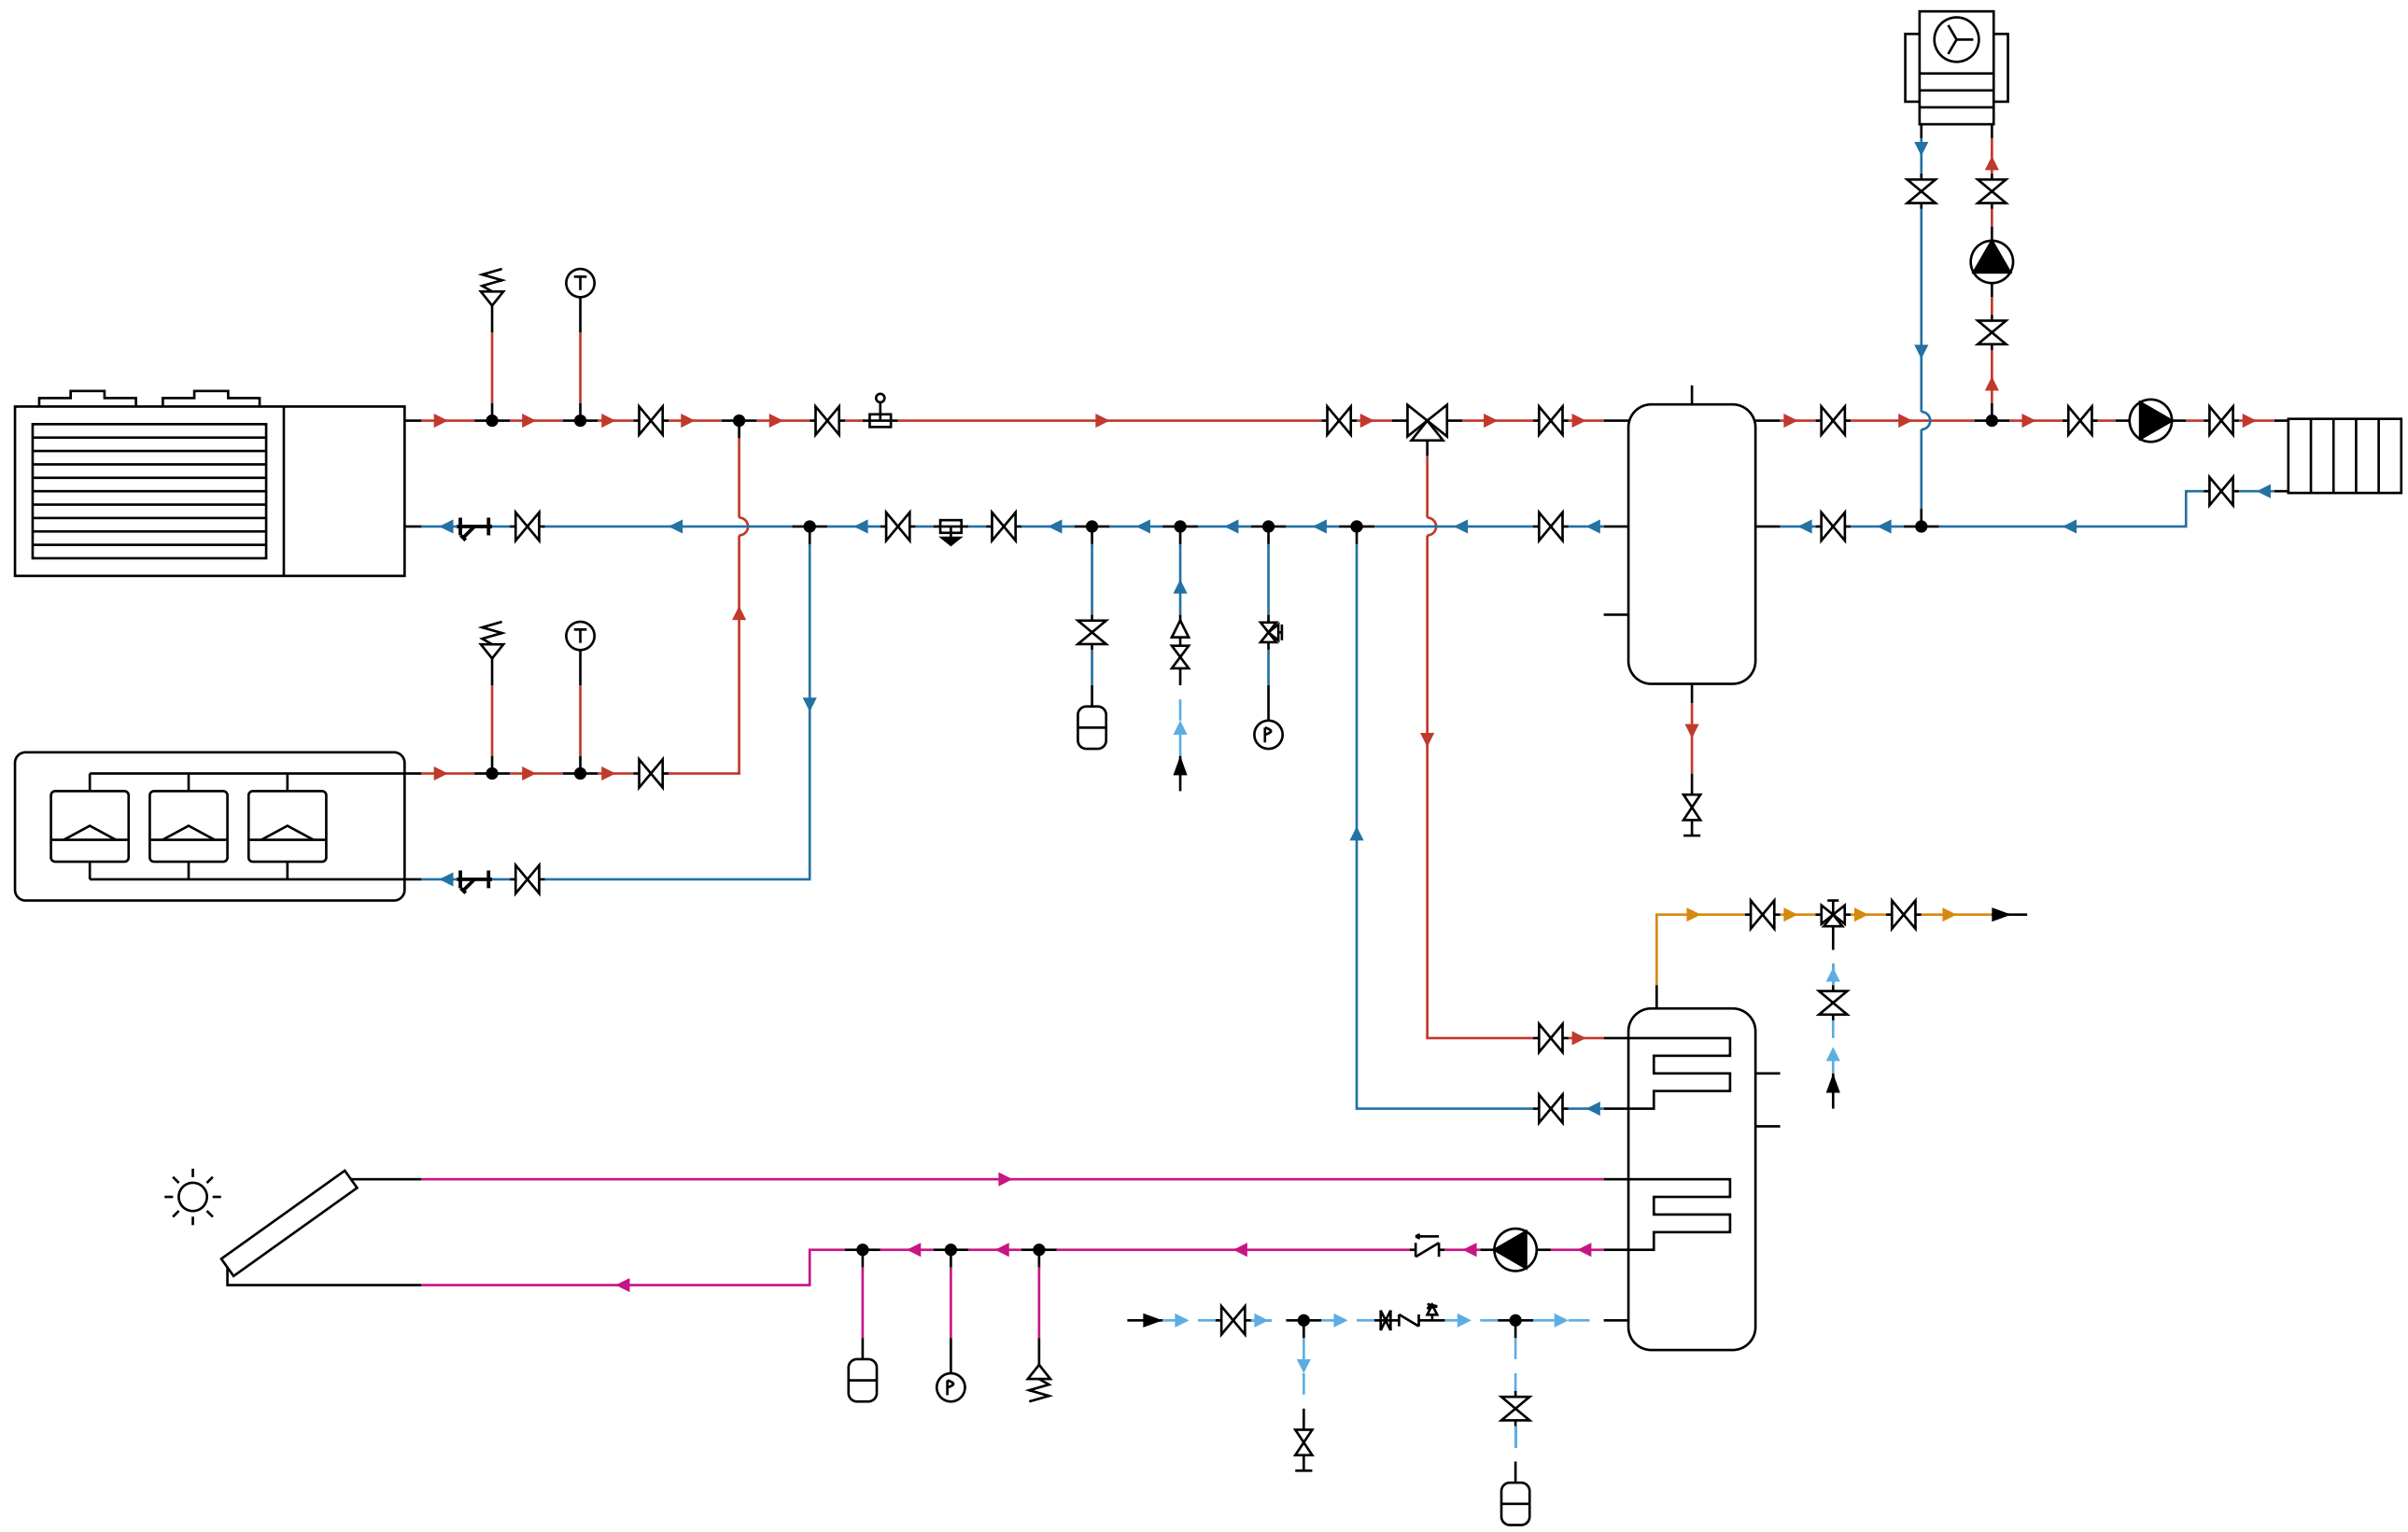

- Separatore d'aria
- Valano termico a quattro attacchi
- Bollitore ACS a due serpentine
- Gruppo di sicurezza sanitario
- Defangatore
- Valvola deviatrice a tre vie
- Attacco di scarico
- Vaso di espansione
- Ventilconvettore canalizzato
- Gruppo di riempimento
- Caldaia modulare a condensazione
- Pompa di calore aria-acqua di alta potenza
- Valvola miscelatrice termostatica
- Confine di rete
- Manometro
- Pompa di circolazione
- Radiatore
- Collettore solare
- Filtro a Y
- Derivazione a T
- Raccordo a T
- Termometro
- Valvola di ritegno
- Rubinetto portamanometro a tre vie
- Valvola di intercettazione
- Valvola di sicurezza

- Acqua fredda sanitaria — andata
- Acqua calda sanitaria — andata
- Acqua di riscaldamento — andata
- Acqua di riscaldamento — ritorno
- Fluido solare — andata e ritorno



COMMITTENTE

Condominio di prova

INDIRIZZO

Via di Prova 1, 00000 Comune di Prova (XX)

PROGETTO

Centrale ibrida condominiale con pompa di calore di alta potenza, caldaia modulare e solare termico

TITOLO TAVOLA

Schema funzionale della centrale termica

SCALA

—

DATA

26.09.2026

REVISIONE

Rev. 00

COMMESSA

PROVA-REL-003

APPROVATO

VERIFICATO

DISEGNATO

TAVOLA

T6