


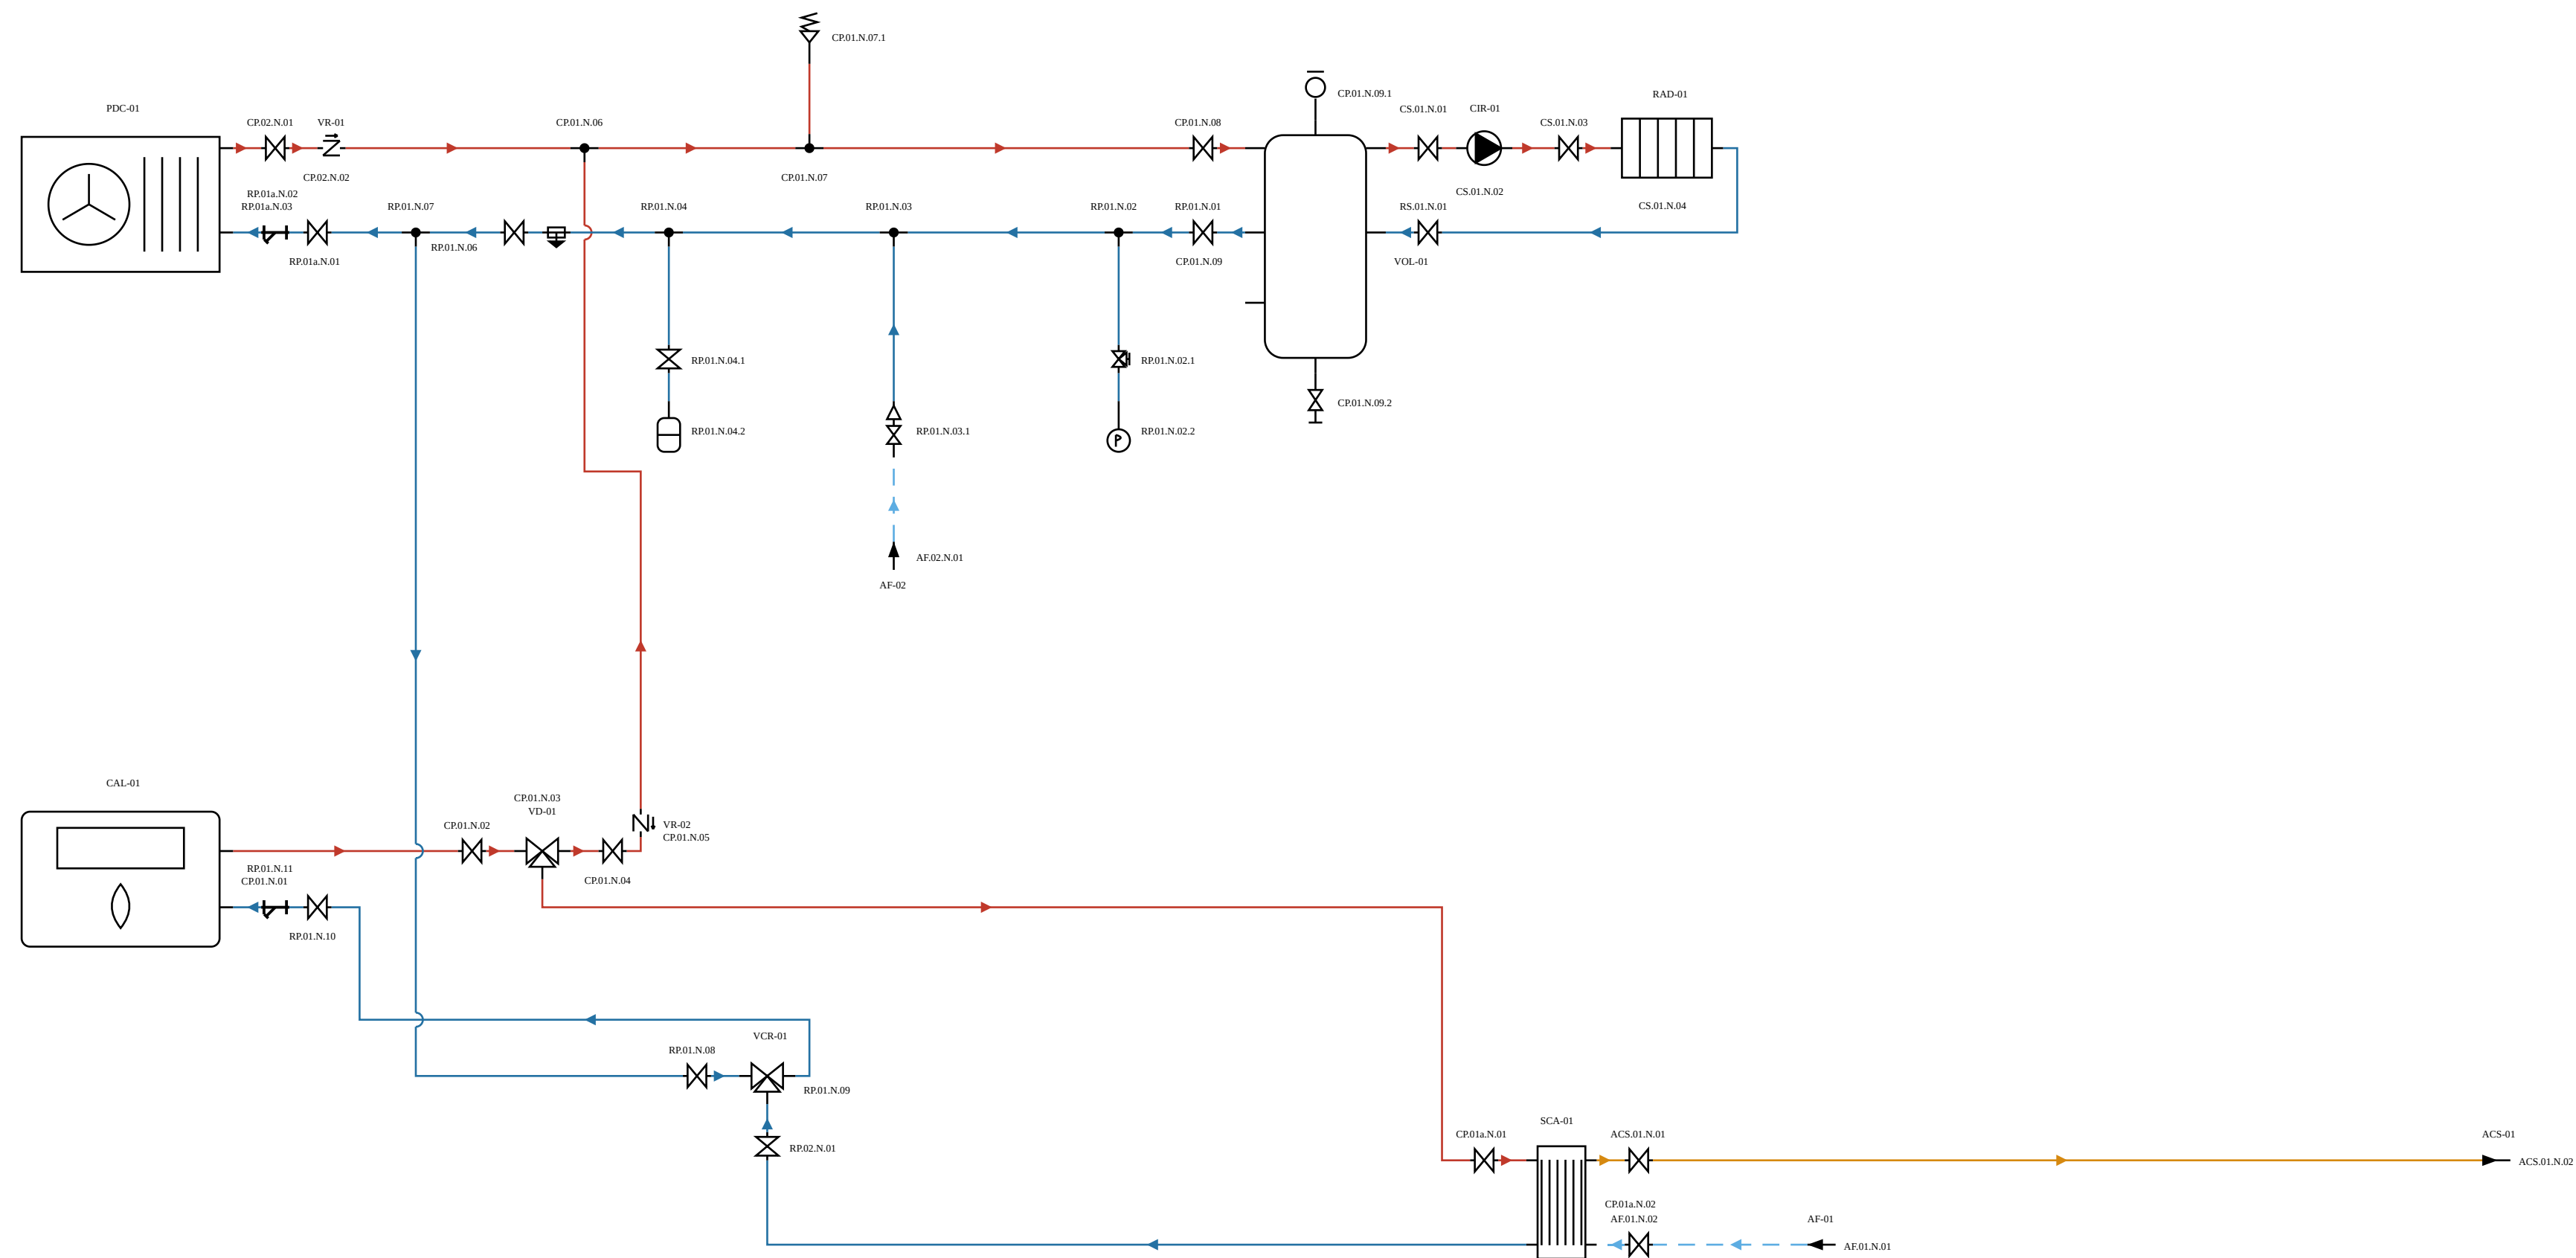

- | | |
|---|------------------------------------|
|  | Valvola di sfiato aria |
|  | Valvola termica a quattro attacchi |
|  | Defangatore |
|  | Valvola deviatrice a tre vie |
|  | Attacco di scarico |
|  | Vaso di espansione |
|  | Gruppo di riempimento |
|  | Caldia a condensazione |
|  | Pompa di calore aria-acqua |
|  | Confine di rete |
|  | Scambiatore a piastre |
|  | Manometro |
|  | Pompa di circolazione |
|  | Radiatore |
|  | Filtro a Y |
|  | Valvola commutatrice a tre vie |
|  | Derivazione a T |
|  | Raccordo a T |
|  | Valvola di ritegno |
|  | Rubinetto portamanometro a tre vie |
|  | Valvola di intercettazione |
|  | Valvola di sicurezza |

- Acqua fredda sanitaria — andata
- Acqua fredda sanitaria — ritorno
- Acqua calda sanitaria — andata
- Acqua calda sanitaria — ritorno
- Acqua di riscaldamento — andata
- Acqua di riscaldamento — ritorno